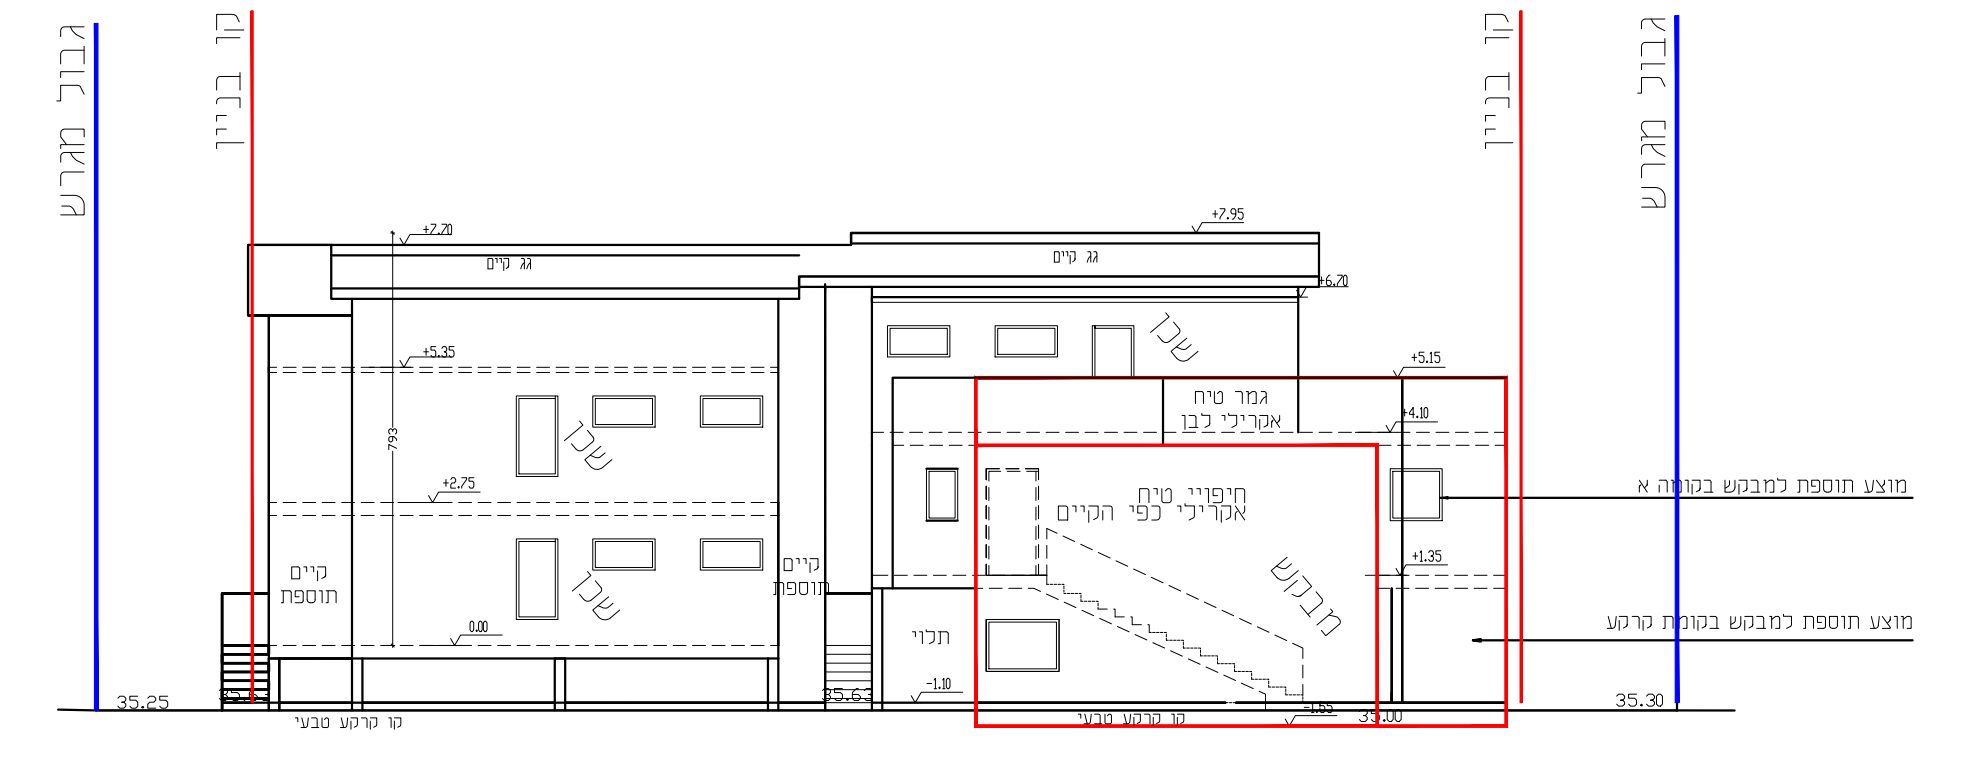
גבול מגרש
קו בניין
שכן
מבוקש
קיים תוספת
מוצע תוספת למבוקש בקומה א
מוצע תוספת למבוקש בקומת קרקע
חזית אחורית -מערב- קנמ 1:100

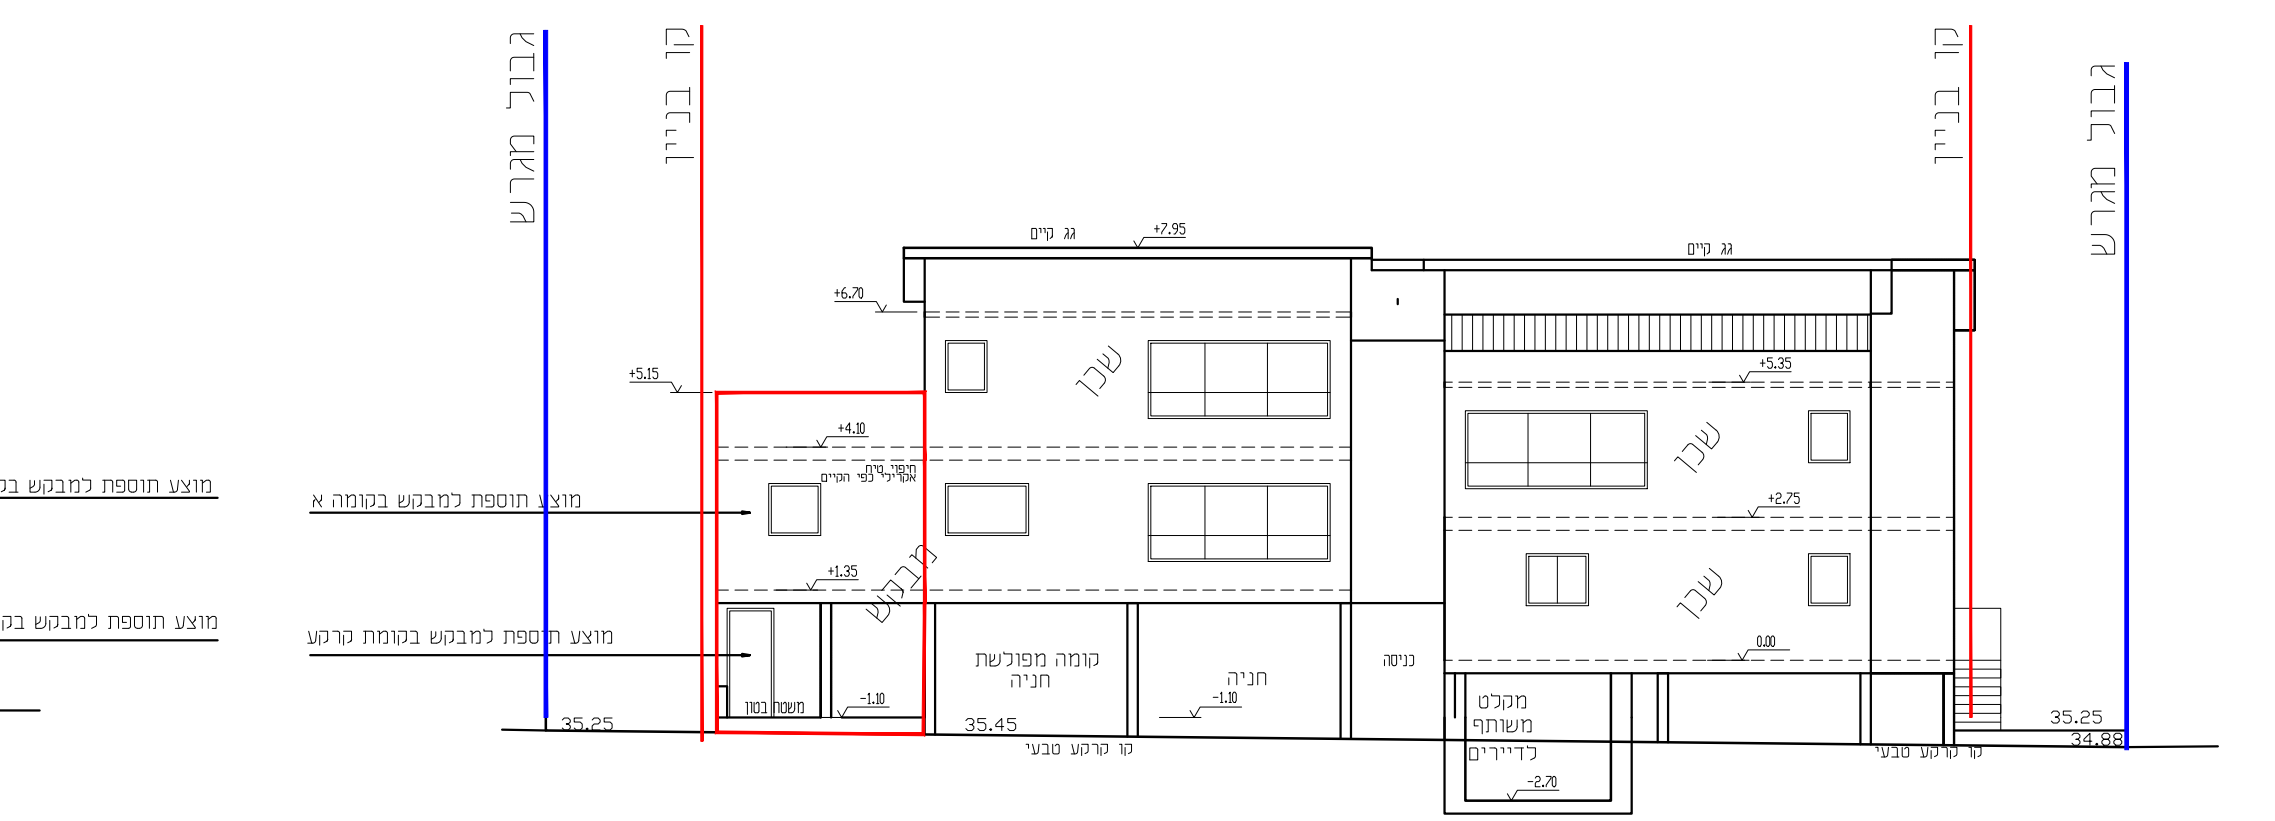
גבול מגרש
קו בניין
שכן
מבוקש
קומה מפולשת
חניה
מוצע תוספת למבוקש בקומה א
מוצע תוספת למבוקש בקומת קרקע
חזית קדמית -מזרח- פונה לרחוב - קנמ 1:100

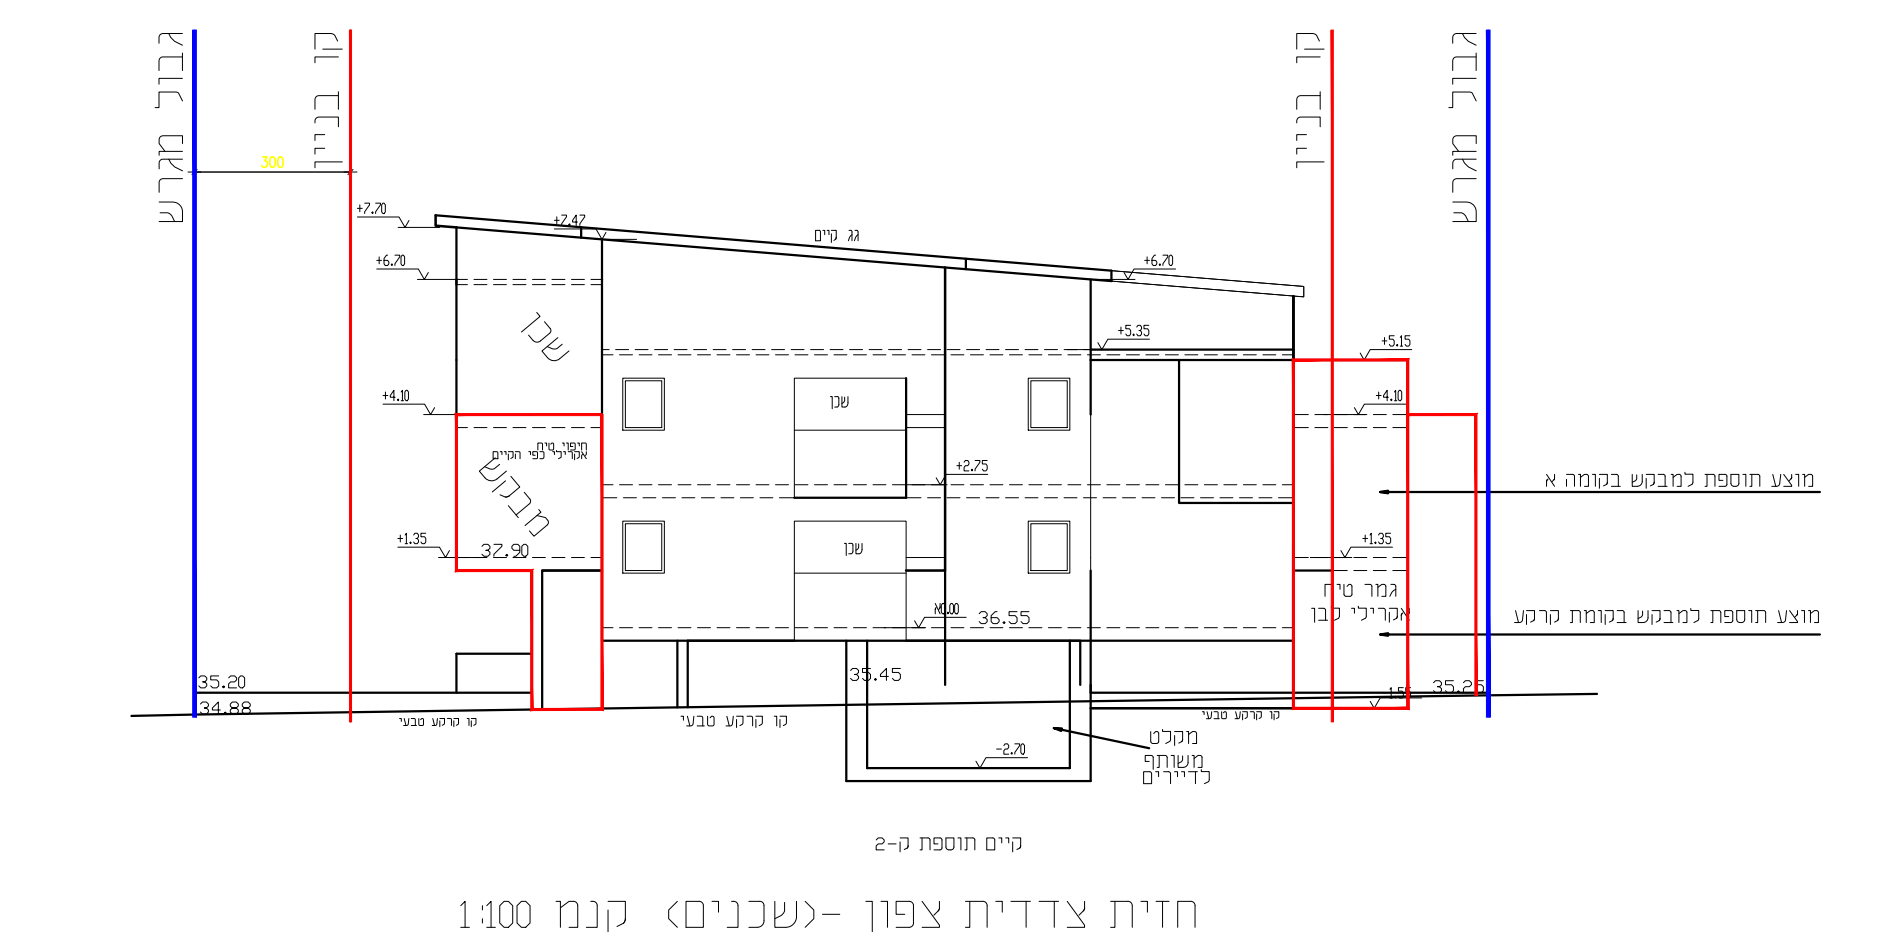
גבול מגרש
קו בניין
שכן
מבוקש
מוצע תוספת למבוקש בקומה א
מוצע תוספת למבוקש בקומת קרקע
חזית צדדית צפון -(שכנים) קנמ 1:100

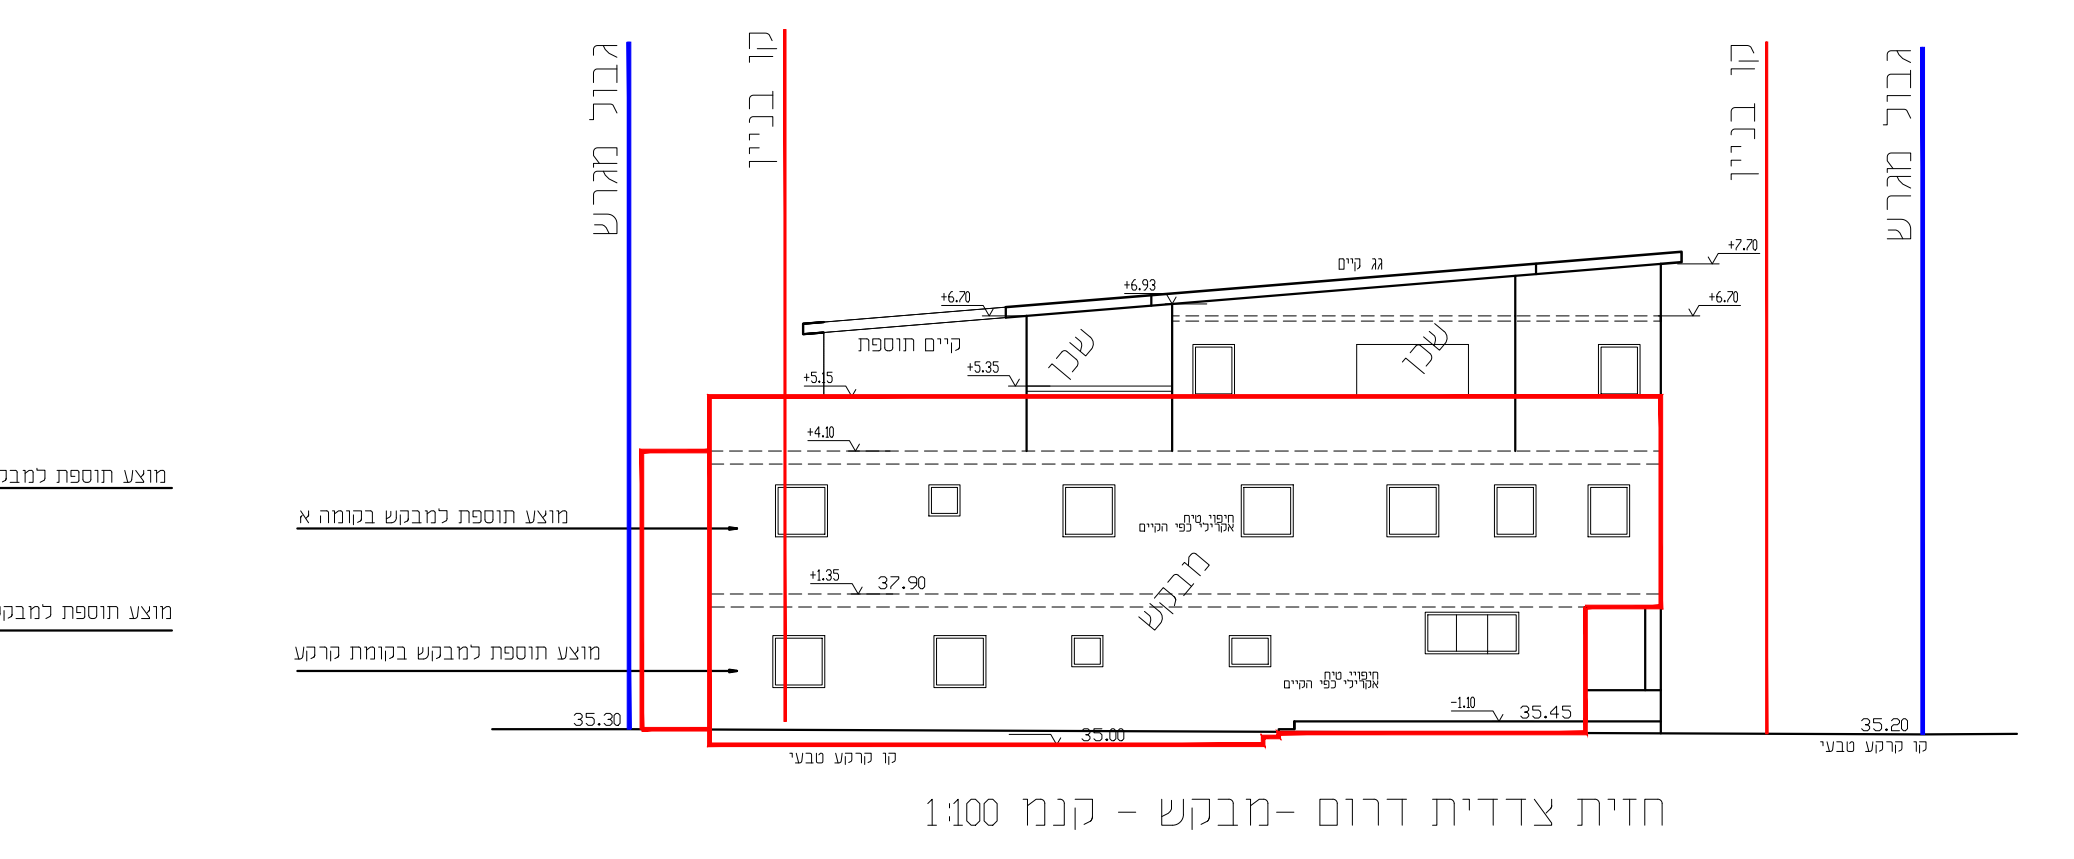
גבול מגרש
קו בניין
שכן
מבוקש
מוצע תוספת למבוקש בקומה א
מוצע תוספת למבוקש בקומת קרקע
חזית צדדית דרום -מבקש - קנמ 1:100

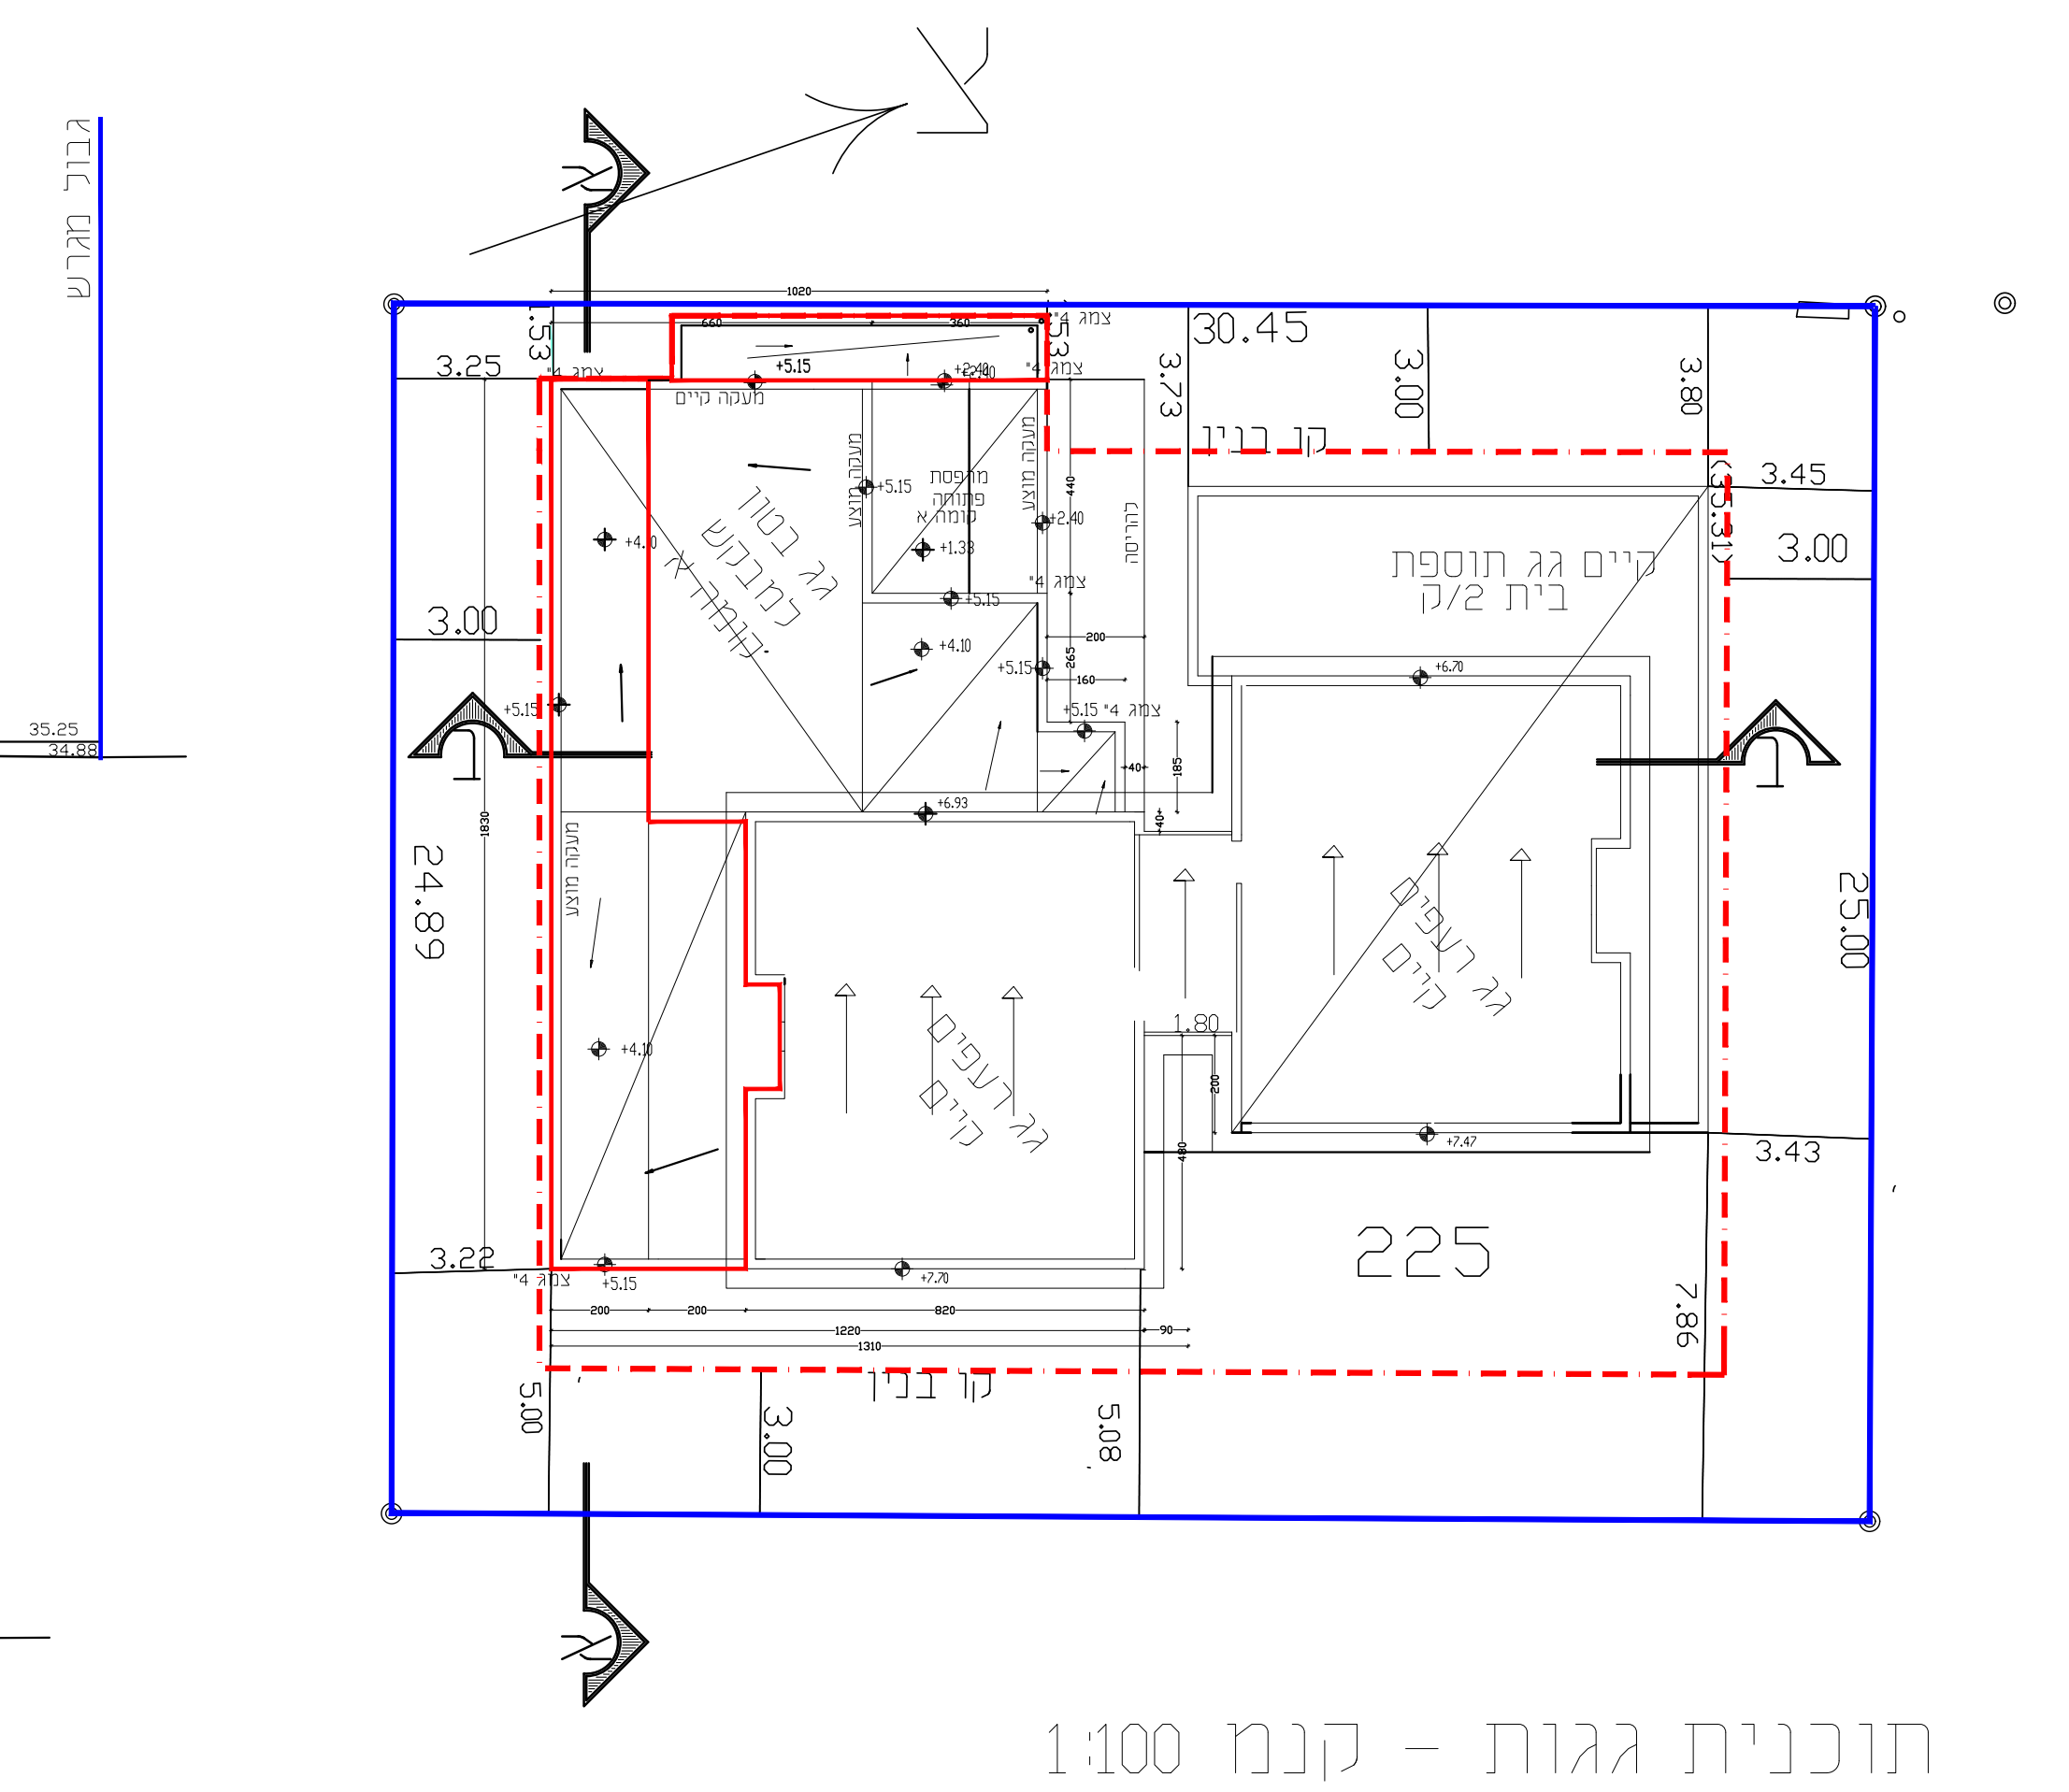
צ
30.45
3.00
3.80
3.73
3.25
קו בניין
קיים גג תוספת בית 2/ק
גג רעפים קיים
3.45
3.00
24.89
25.00
3.43
3.22
7.86
225
5.00
3.00
5.08
תוכנית גגות - קנמ 1:100

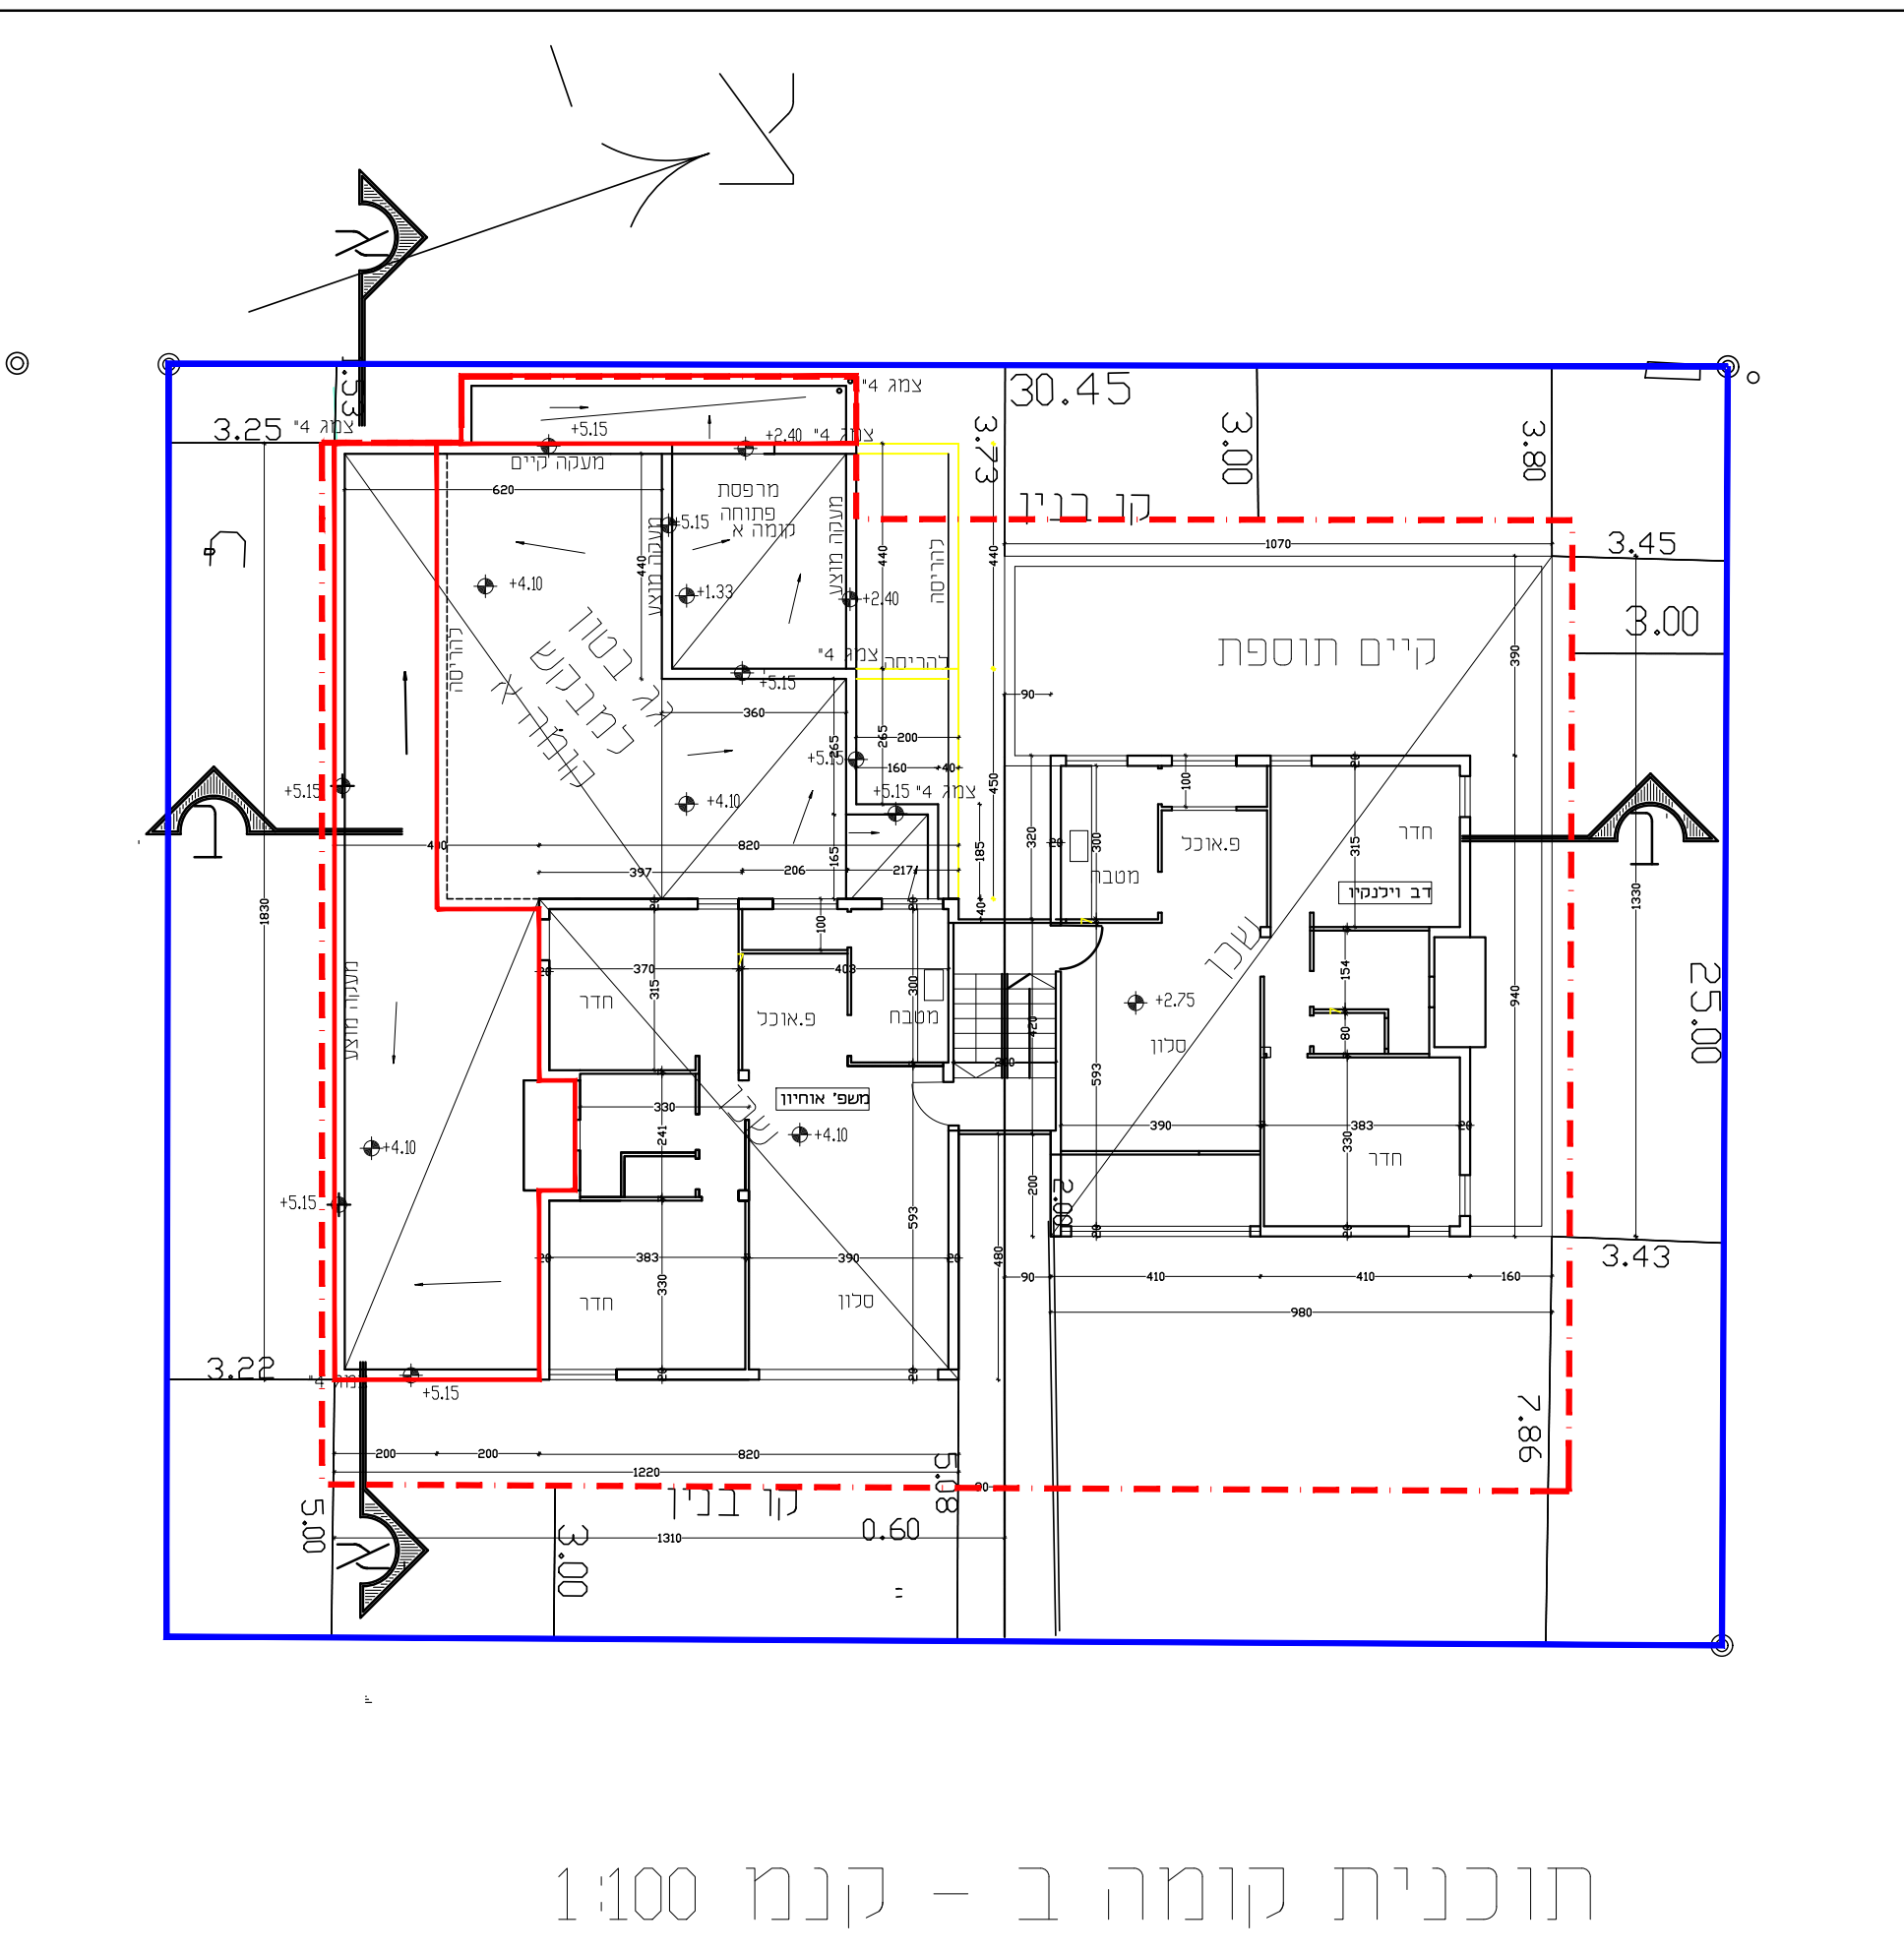
צ
30.45
3.25
3.00
קו בניין
קיים תוספת
3.45
3.00
25.00
3.43
3.22
7.86
0.60
5.00
תוכנית קומה ב - קנמ 1:100

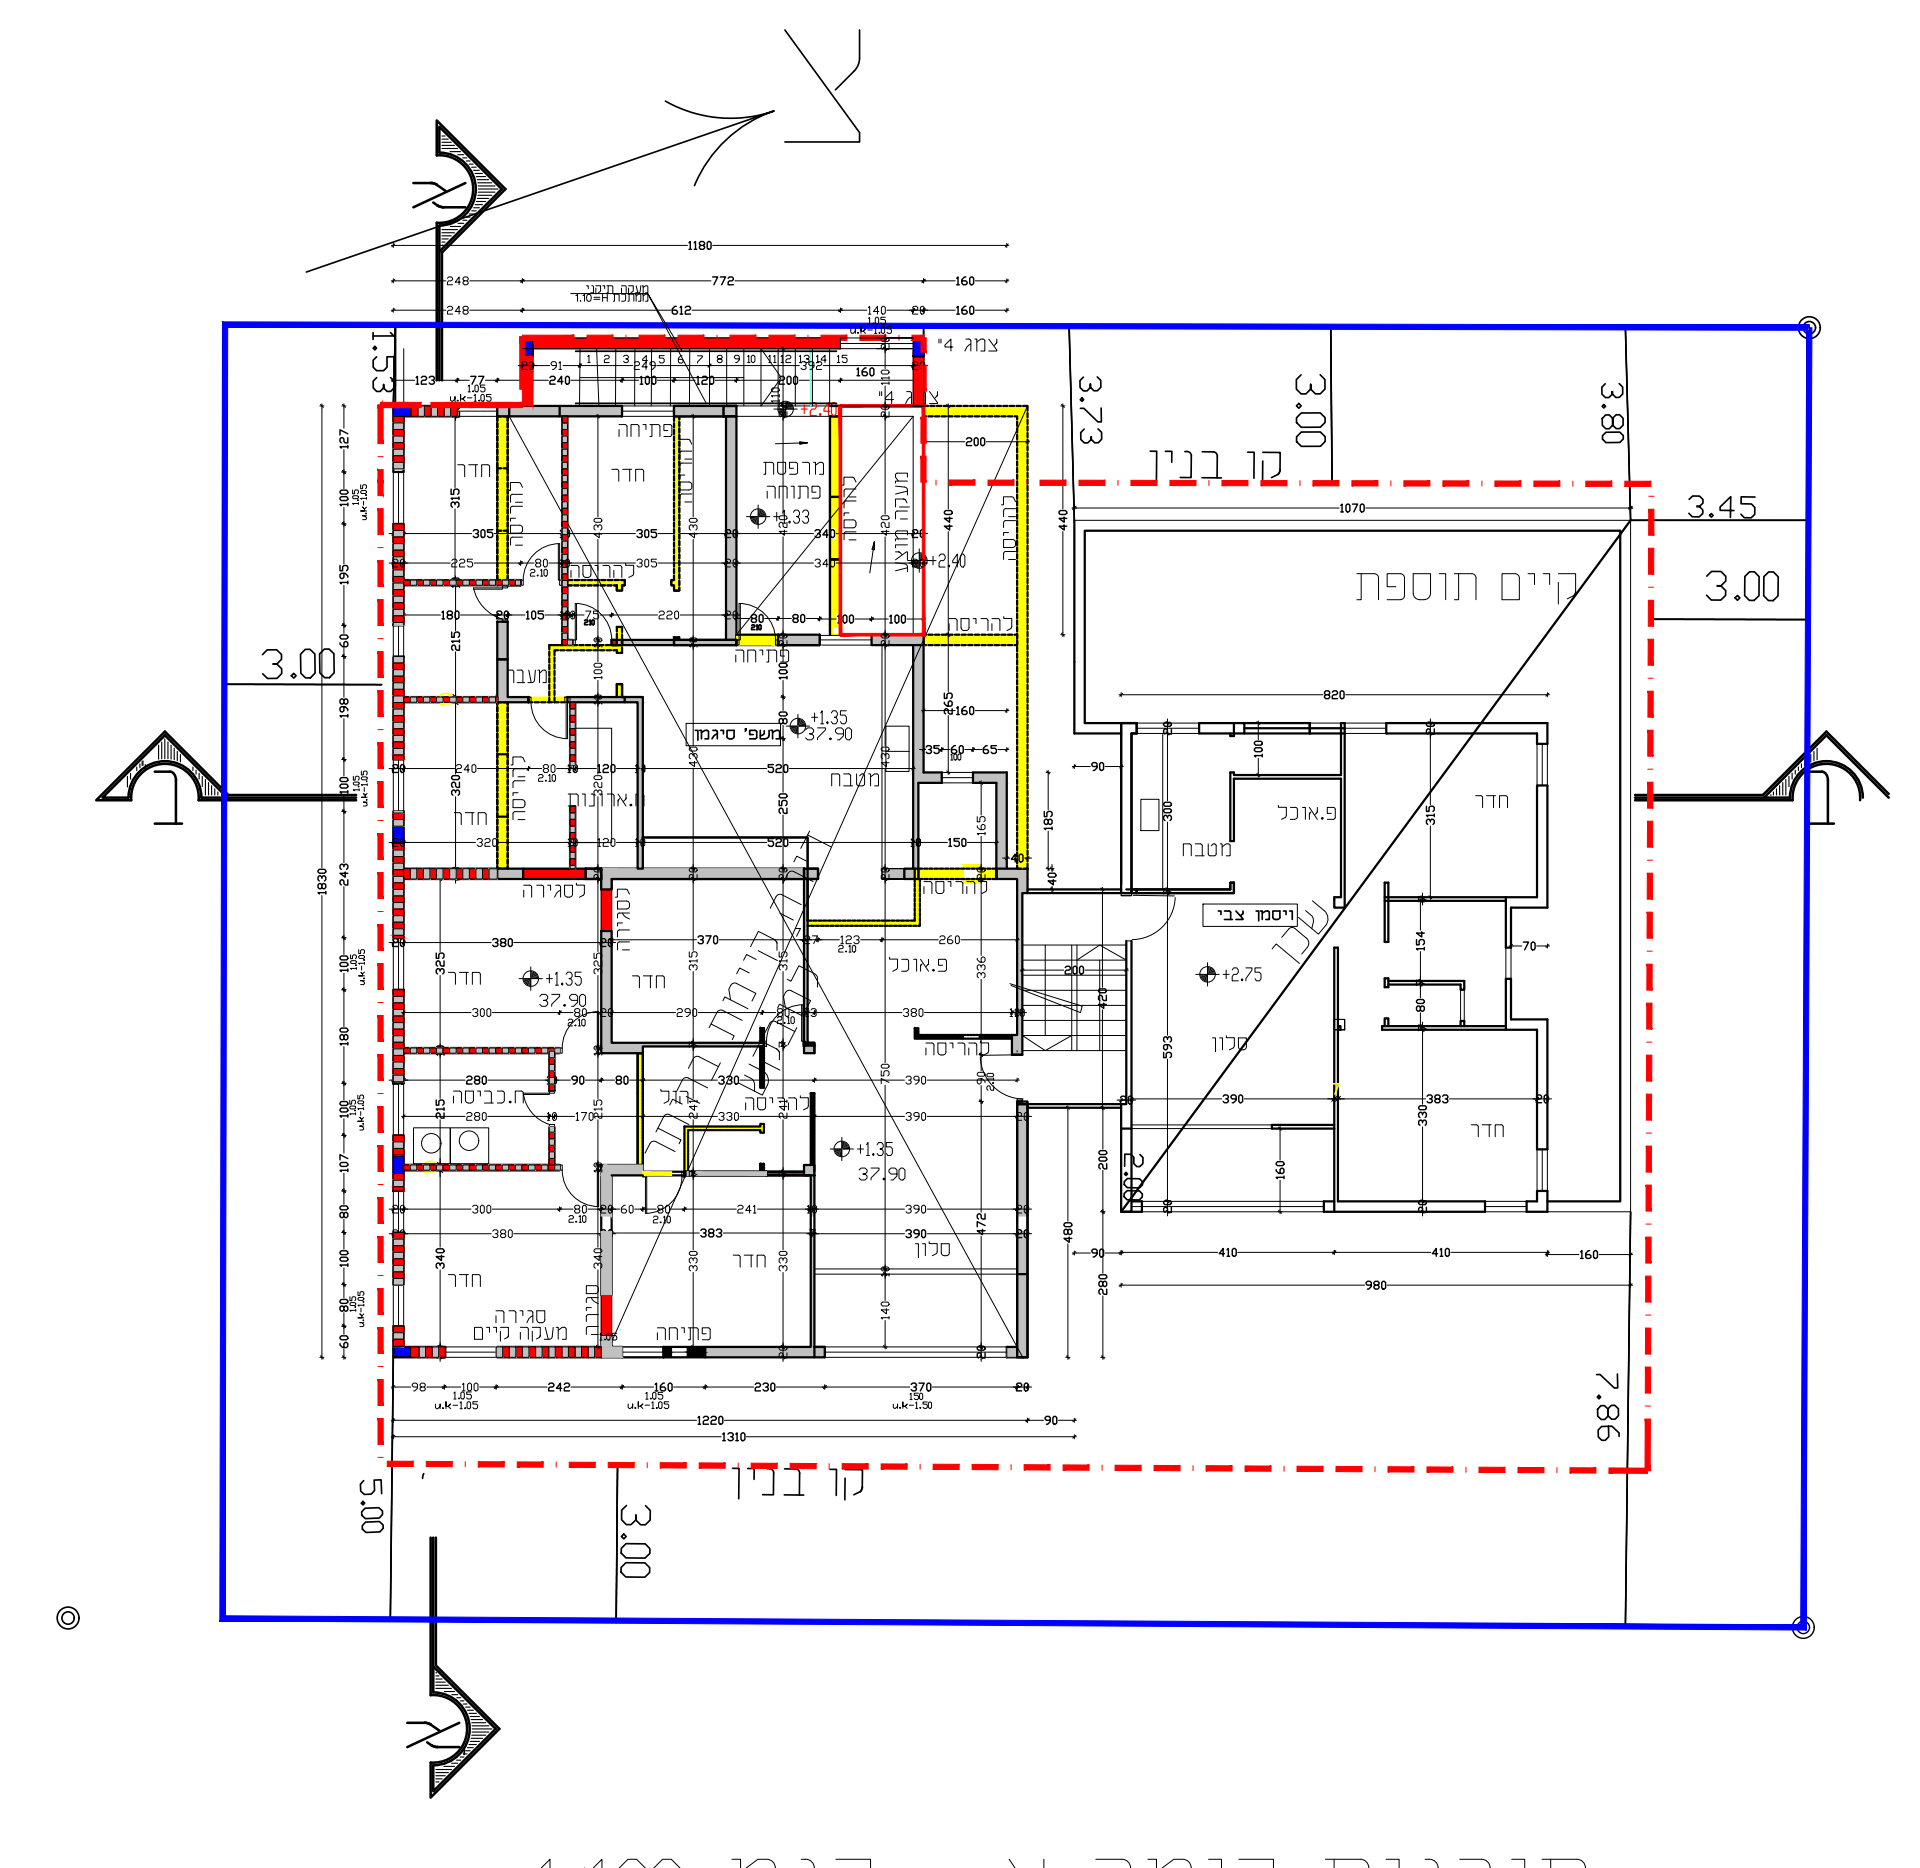
צ
3.00
קו בניין
3.80
3.45
3.00
3.43
7.86
5.00
תוכנית קומה א - קנמ 1:100

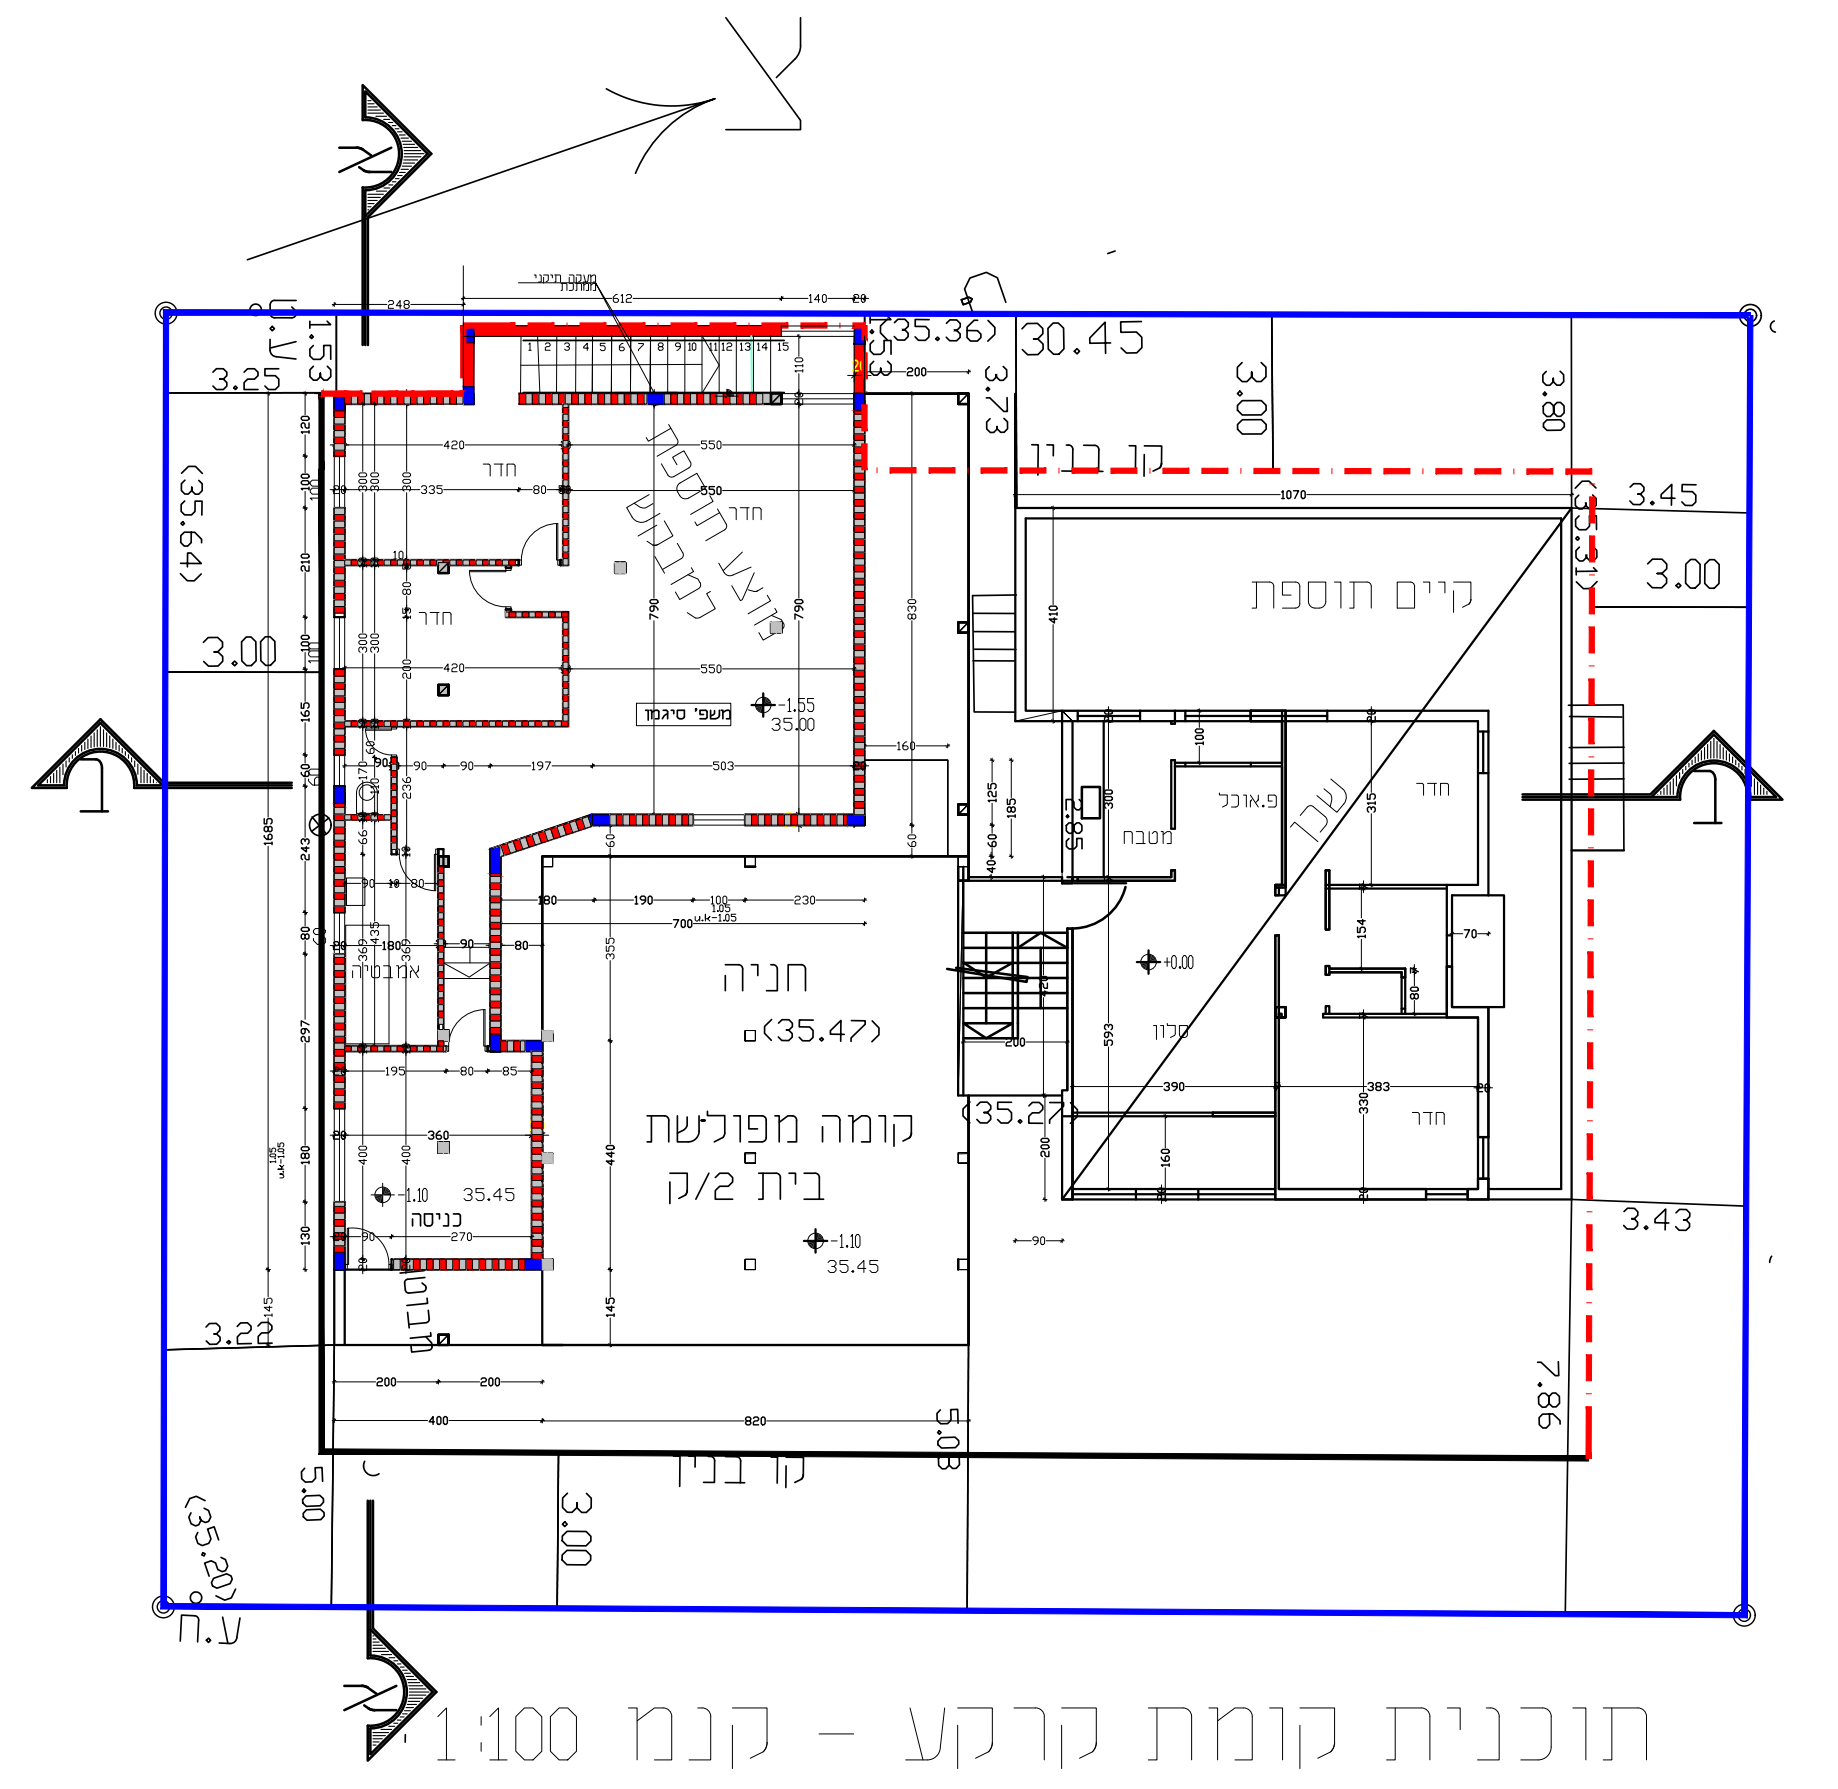
צ
30.45
3.25
3.00
קו בניין
קיים תוספת
חניה
(35.47)
קומה מפולשת
בית 2/ק
(35.36)
(35.24)
3.45
3.00
3.43
3.22
7.86
5.00
3.00
ע.ח
תוכנית קומת קרקע - קנמ 1:100

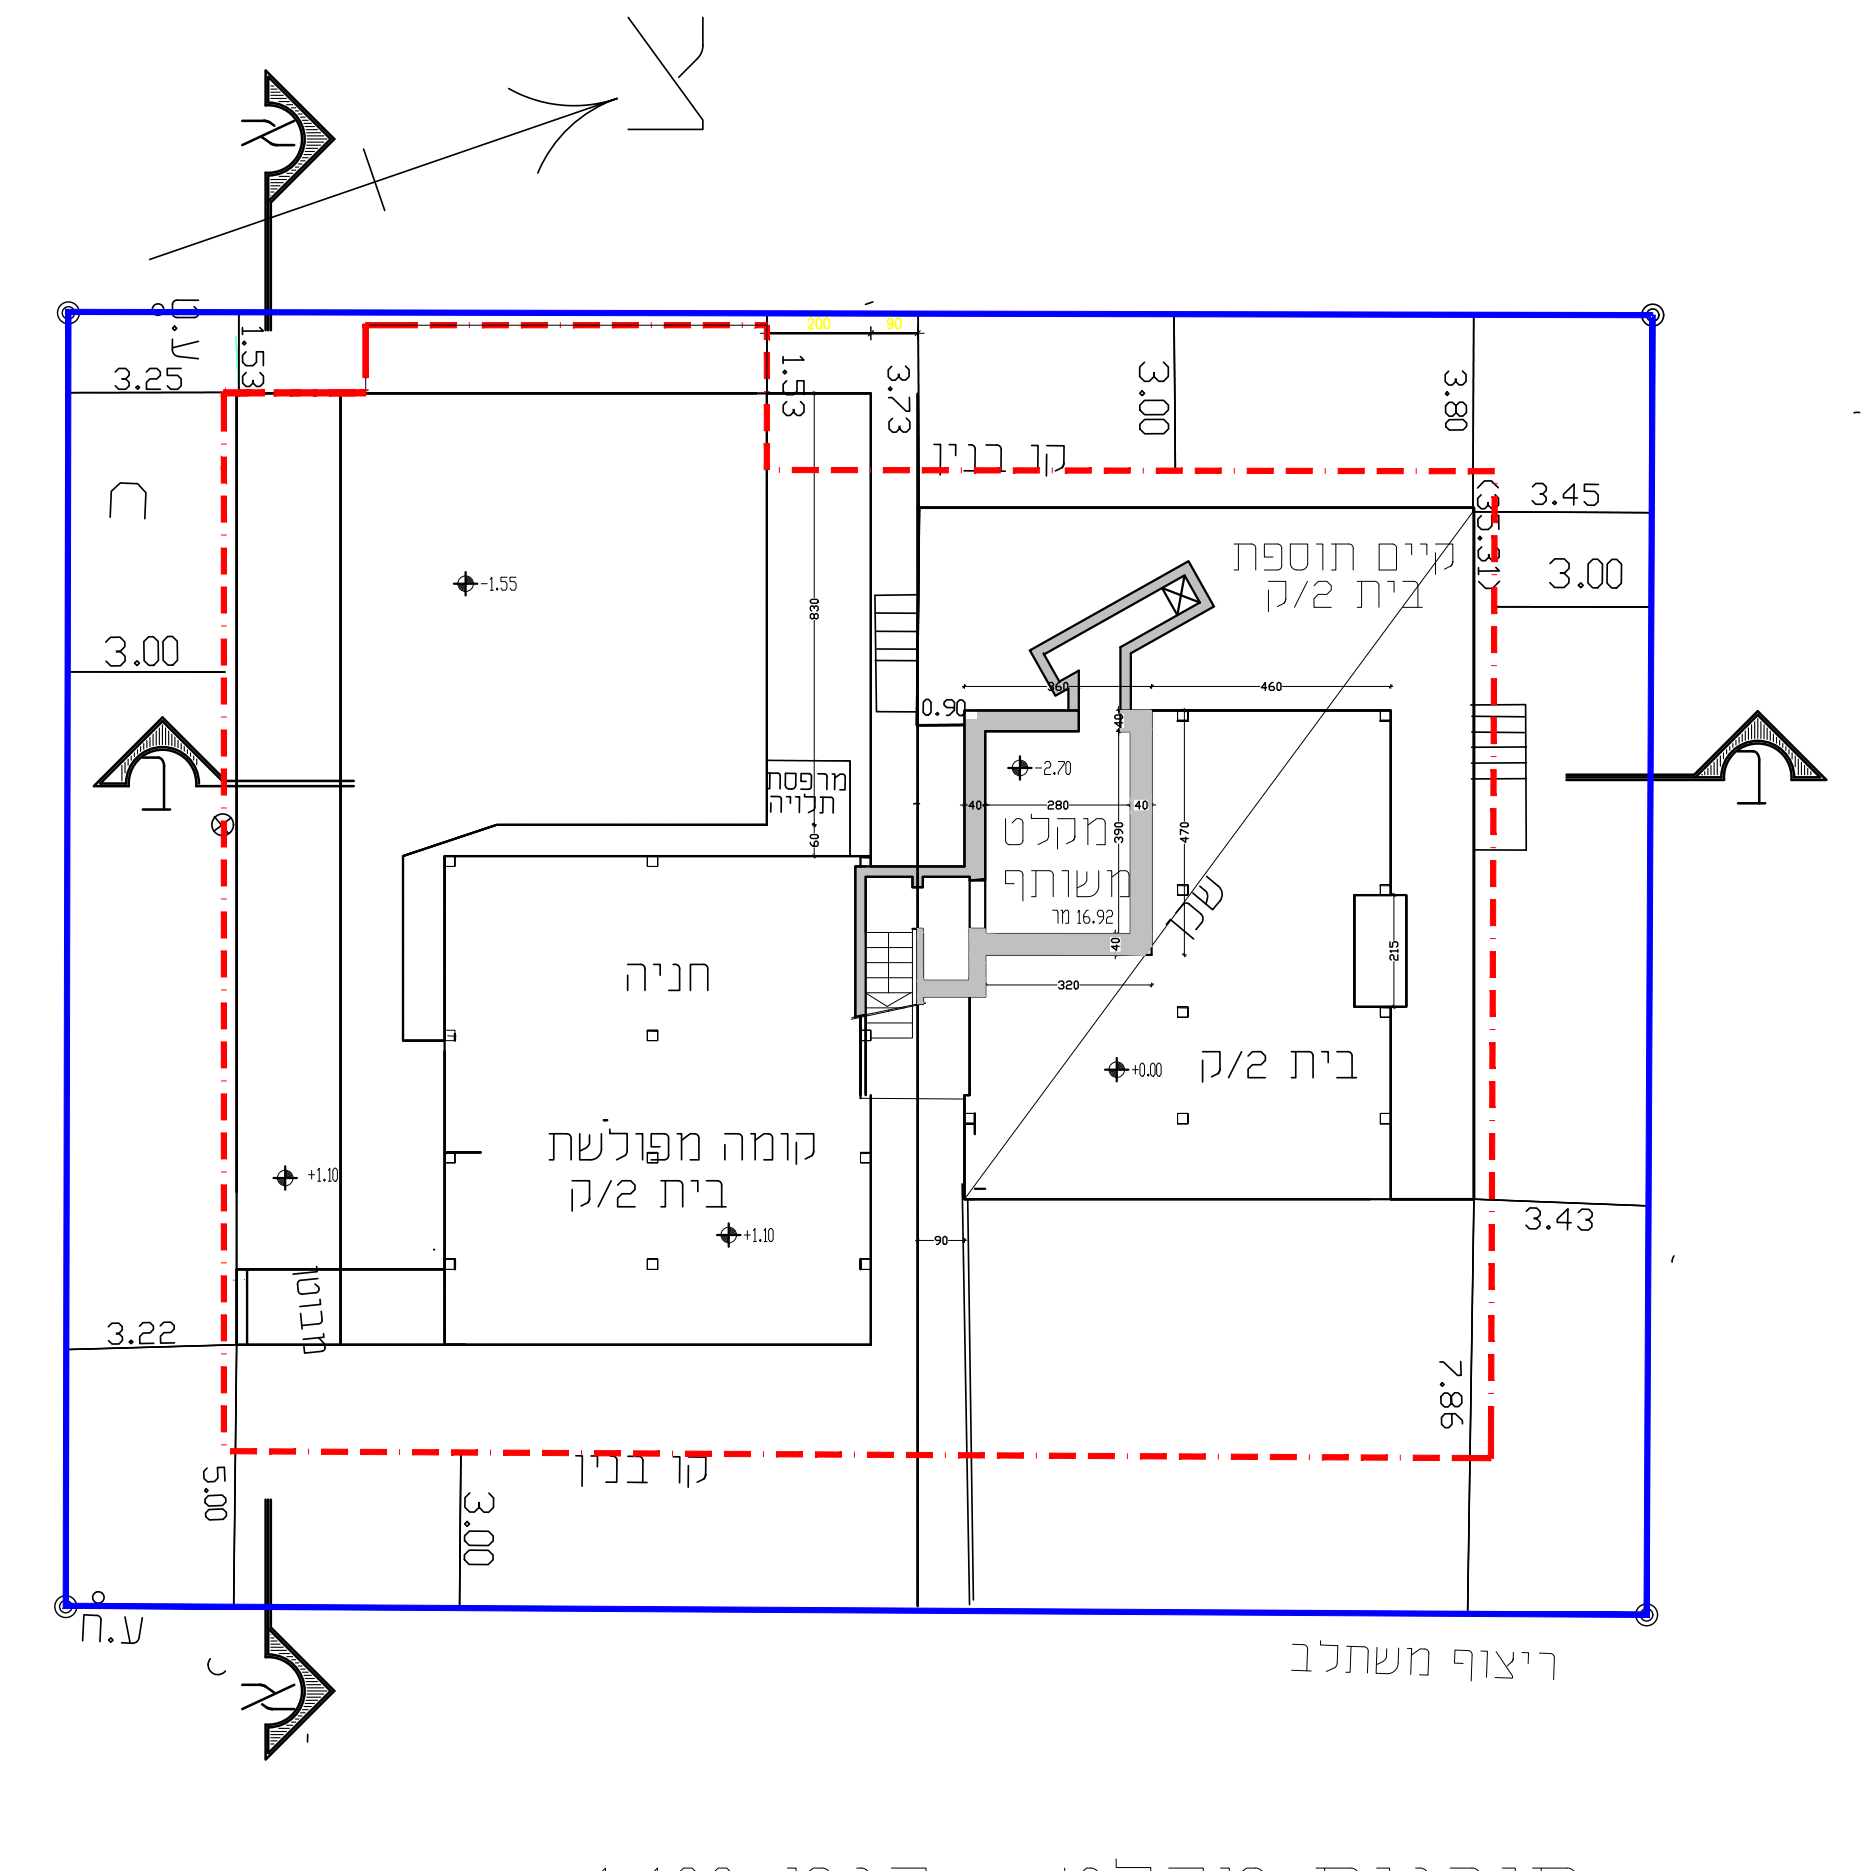
צ
3.00
קיים תוספת
בית 2/ק
חניה
קומה מפולשת
בית 2/ק
מקלט משותף
3.45
3.00
3.43
3.22
7.86
5.00
3.00
ע.ח
ריצוף משתלב
תוכנית מקלט - קנמ 1:100

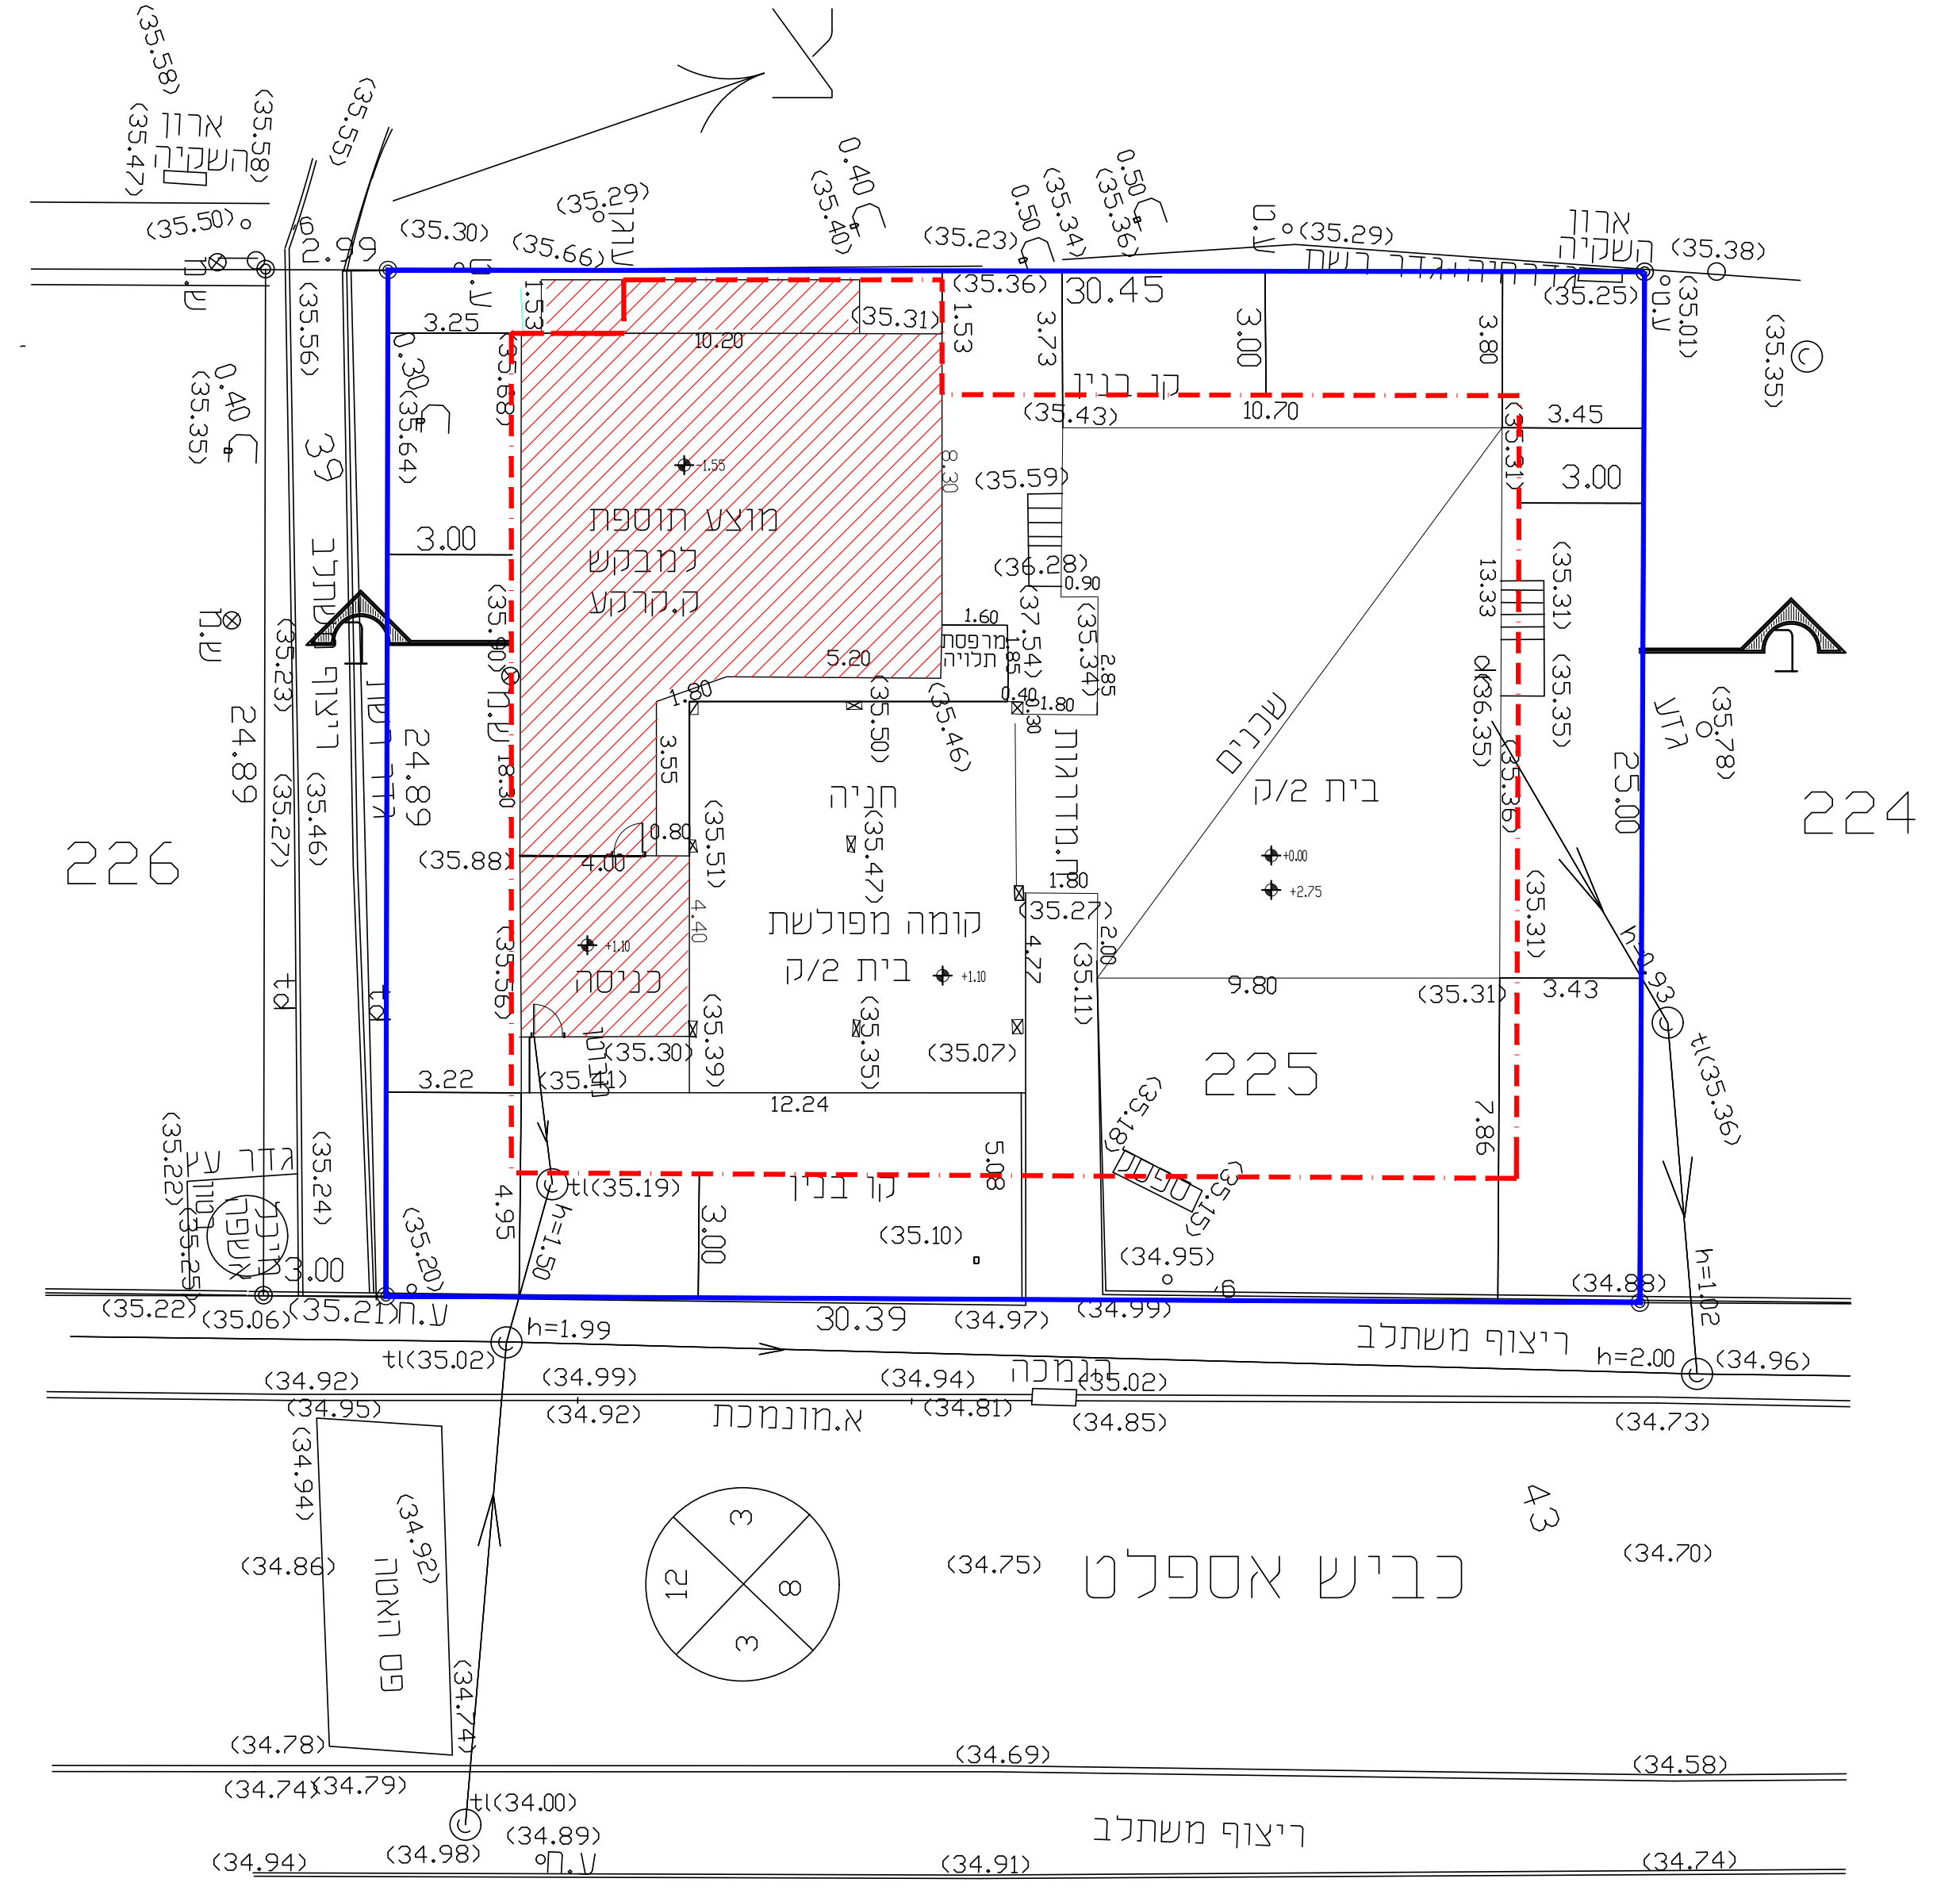
צ
ארון תקשורת
ארון חשמל
226
224
225
24.89
30.45
3.00
קו בניין
מוצע תוספת למבוקש ק.קרקע
חניה
קומה מפולשת
בית 2/ק
כניסה
שכנים
בית 2/ק
30.39
12.24
9.80
3.45
3.43
7.86
ריצוף משתלב
א.מונמכת
כביש אספלט
ריצוף משתלב
60 מ"מ
(35.10)
(34.95)
(34.75)
(34.70)
(34.69)
(34.58)
(34.74)
h=1.99
h=2.00
תוכנית פיתוח מגרש - קנמ 1:100

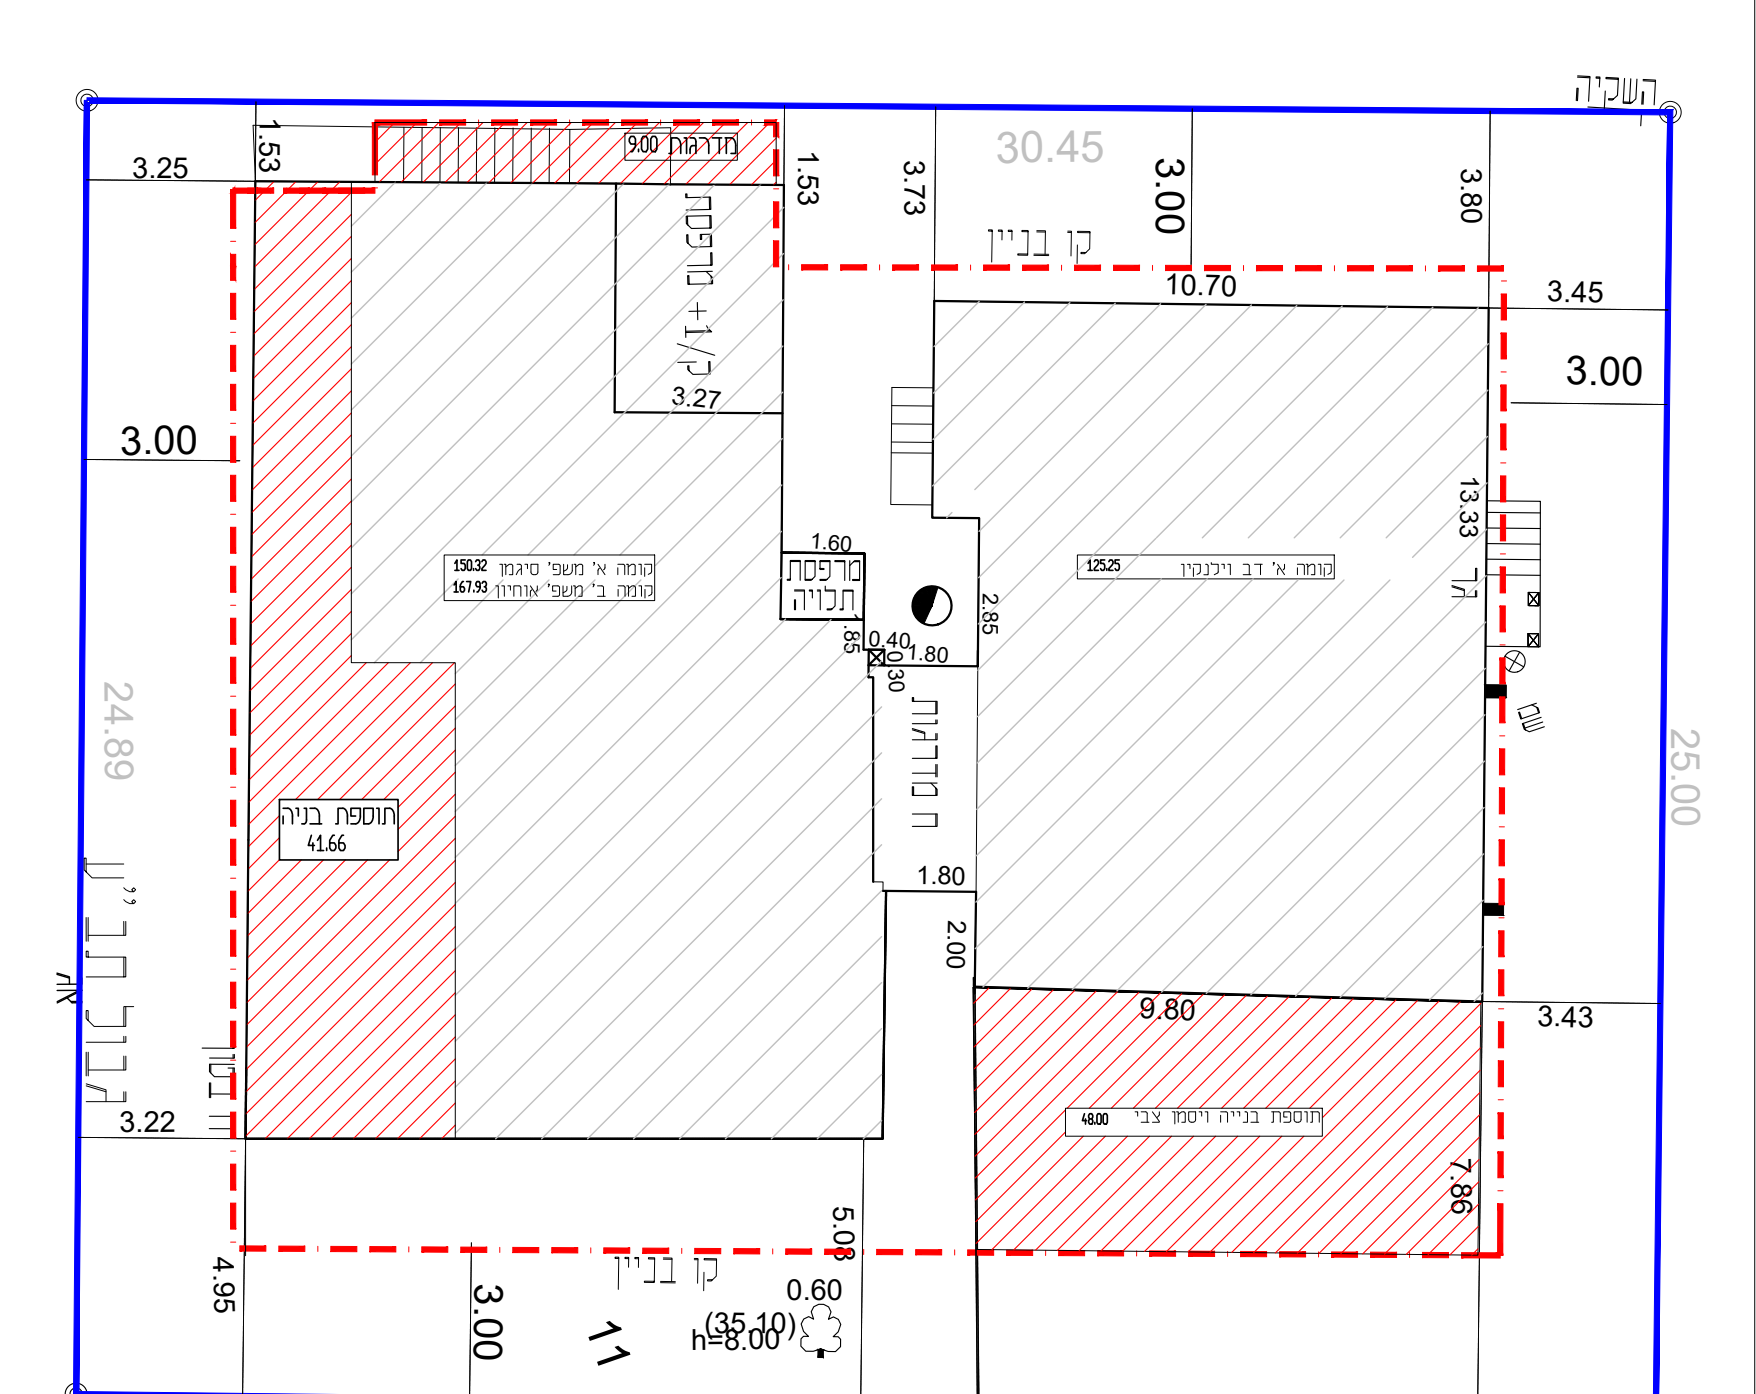
השקיה
30.45
3.00
קו בניין
מרפסת
10.70
3.45
3.00
3.00
24.89
9.80
3.43
3.22
7.86
4.95
3.00
11
0.60
(35.10)
h=8.00
h=1.99
תוכנית בינוי מוצעת קנ"מ 1:100
תוכנית קומה א'

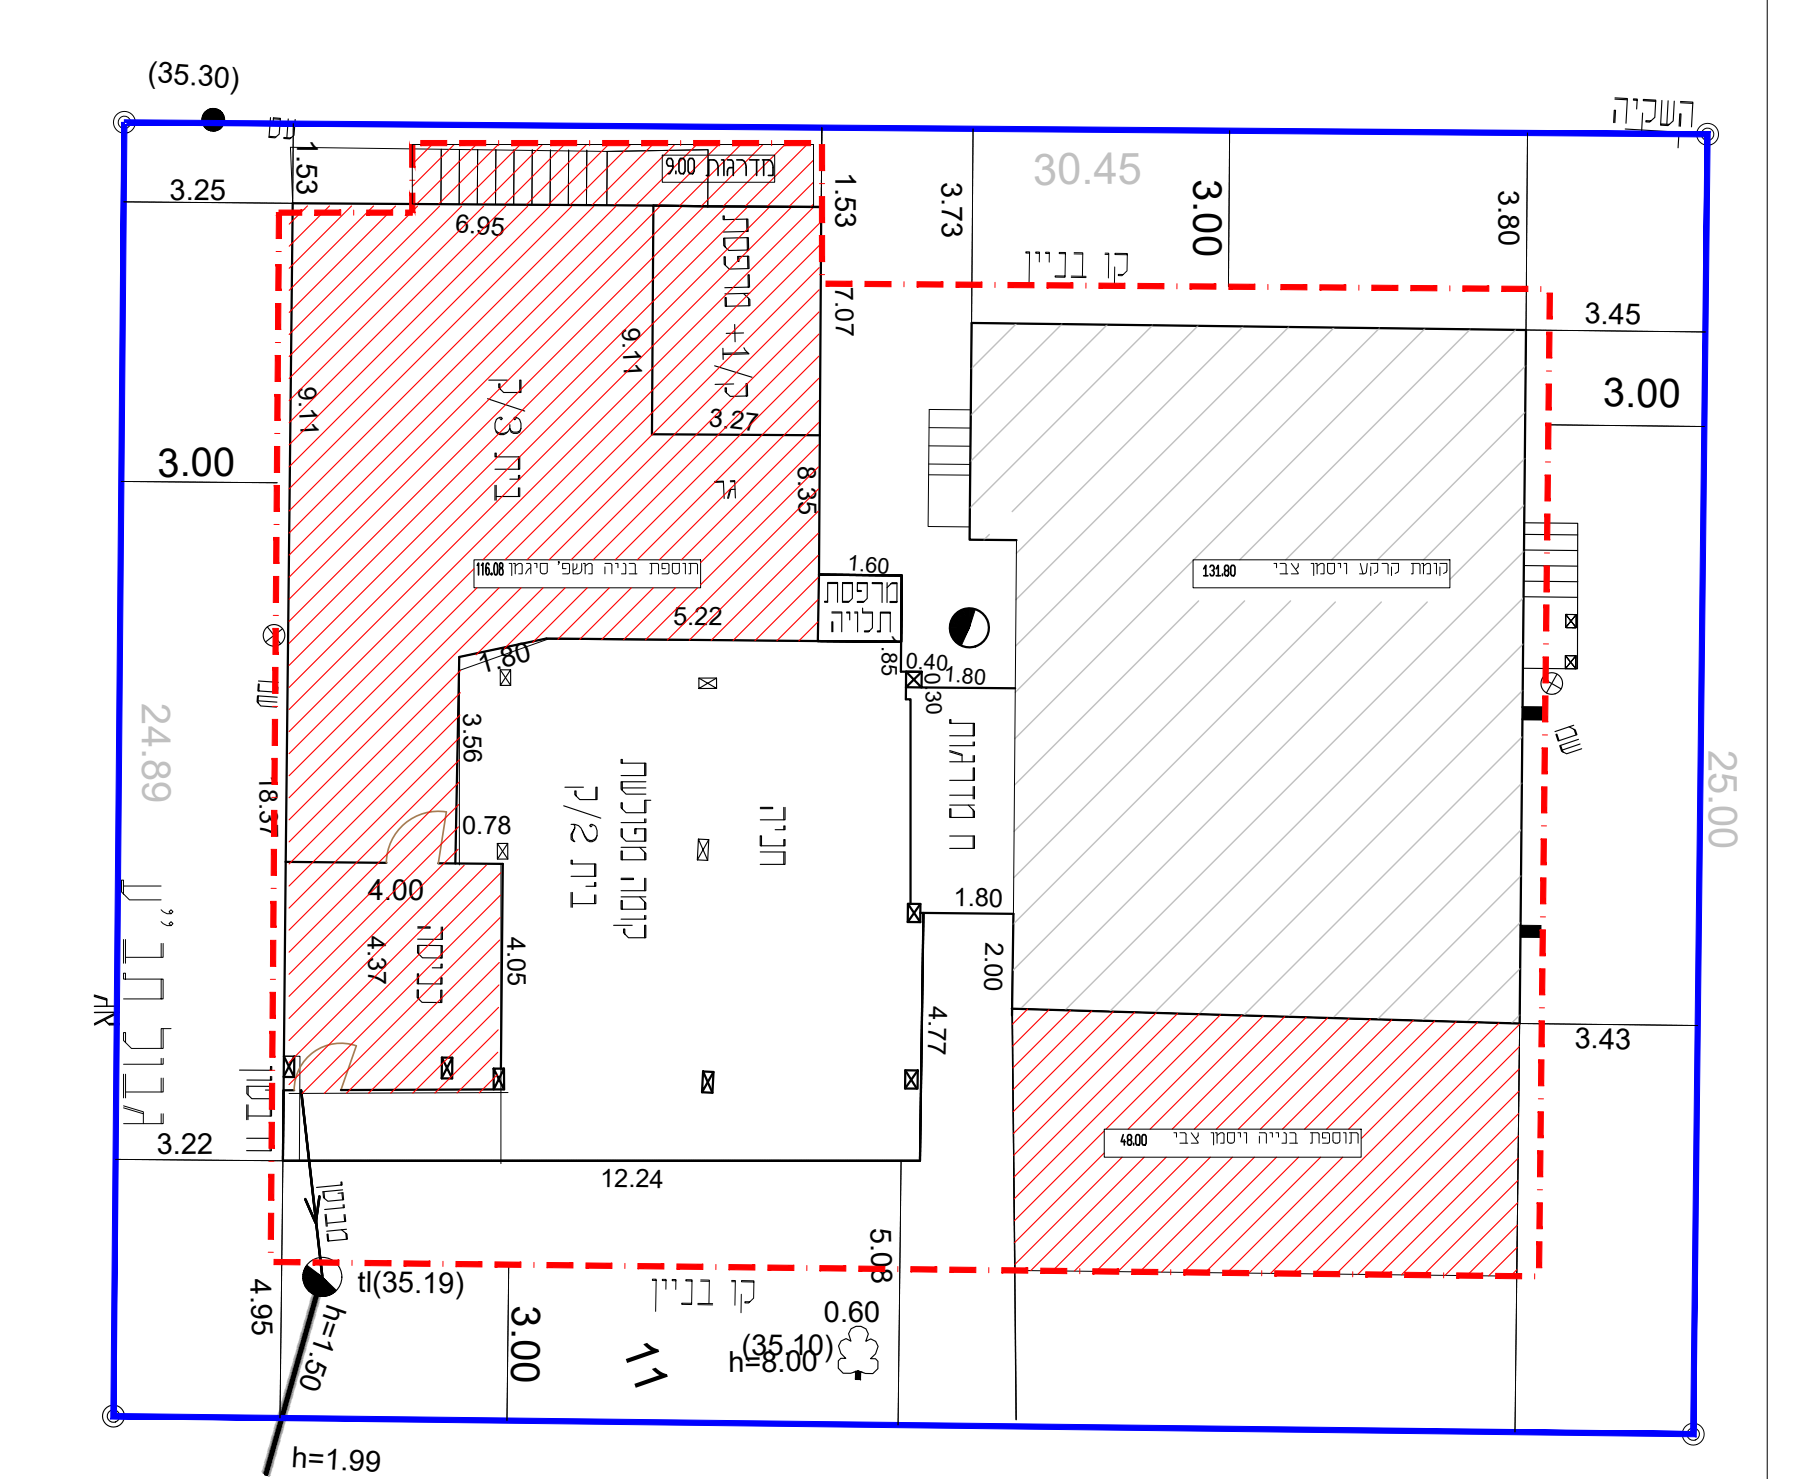
(35.30)
השקיה
30.45
3.00
קו בניין
בית 2/ק
חניה
קומה מפולשת
בית 2/ק
כניסה
12.24
9.80
3.43
3.22
7.86
4.95
3.00
11
0.60
(35.19)
(35.10)
h=1.50
h=8.00
h=1.99
תוכנית מצב קיים קנ"מ 1:100
תוכנית קומת קרקע

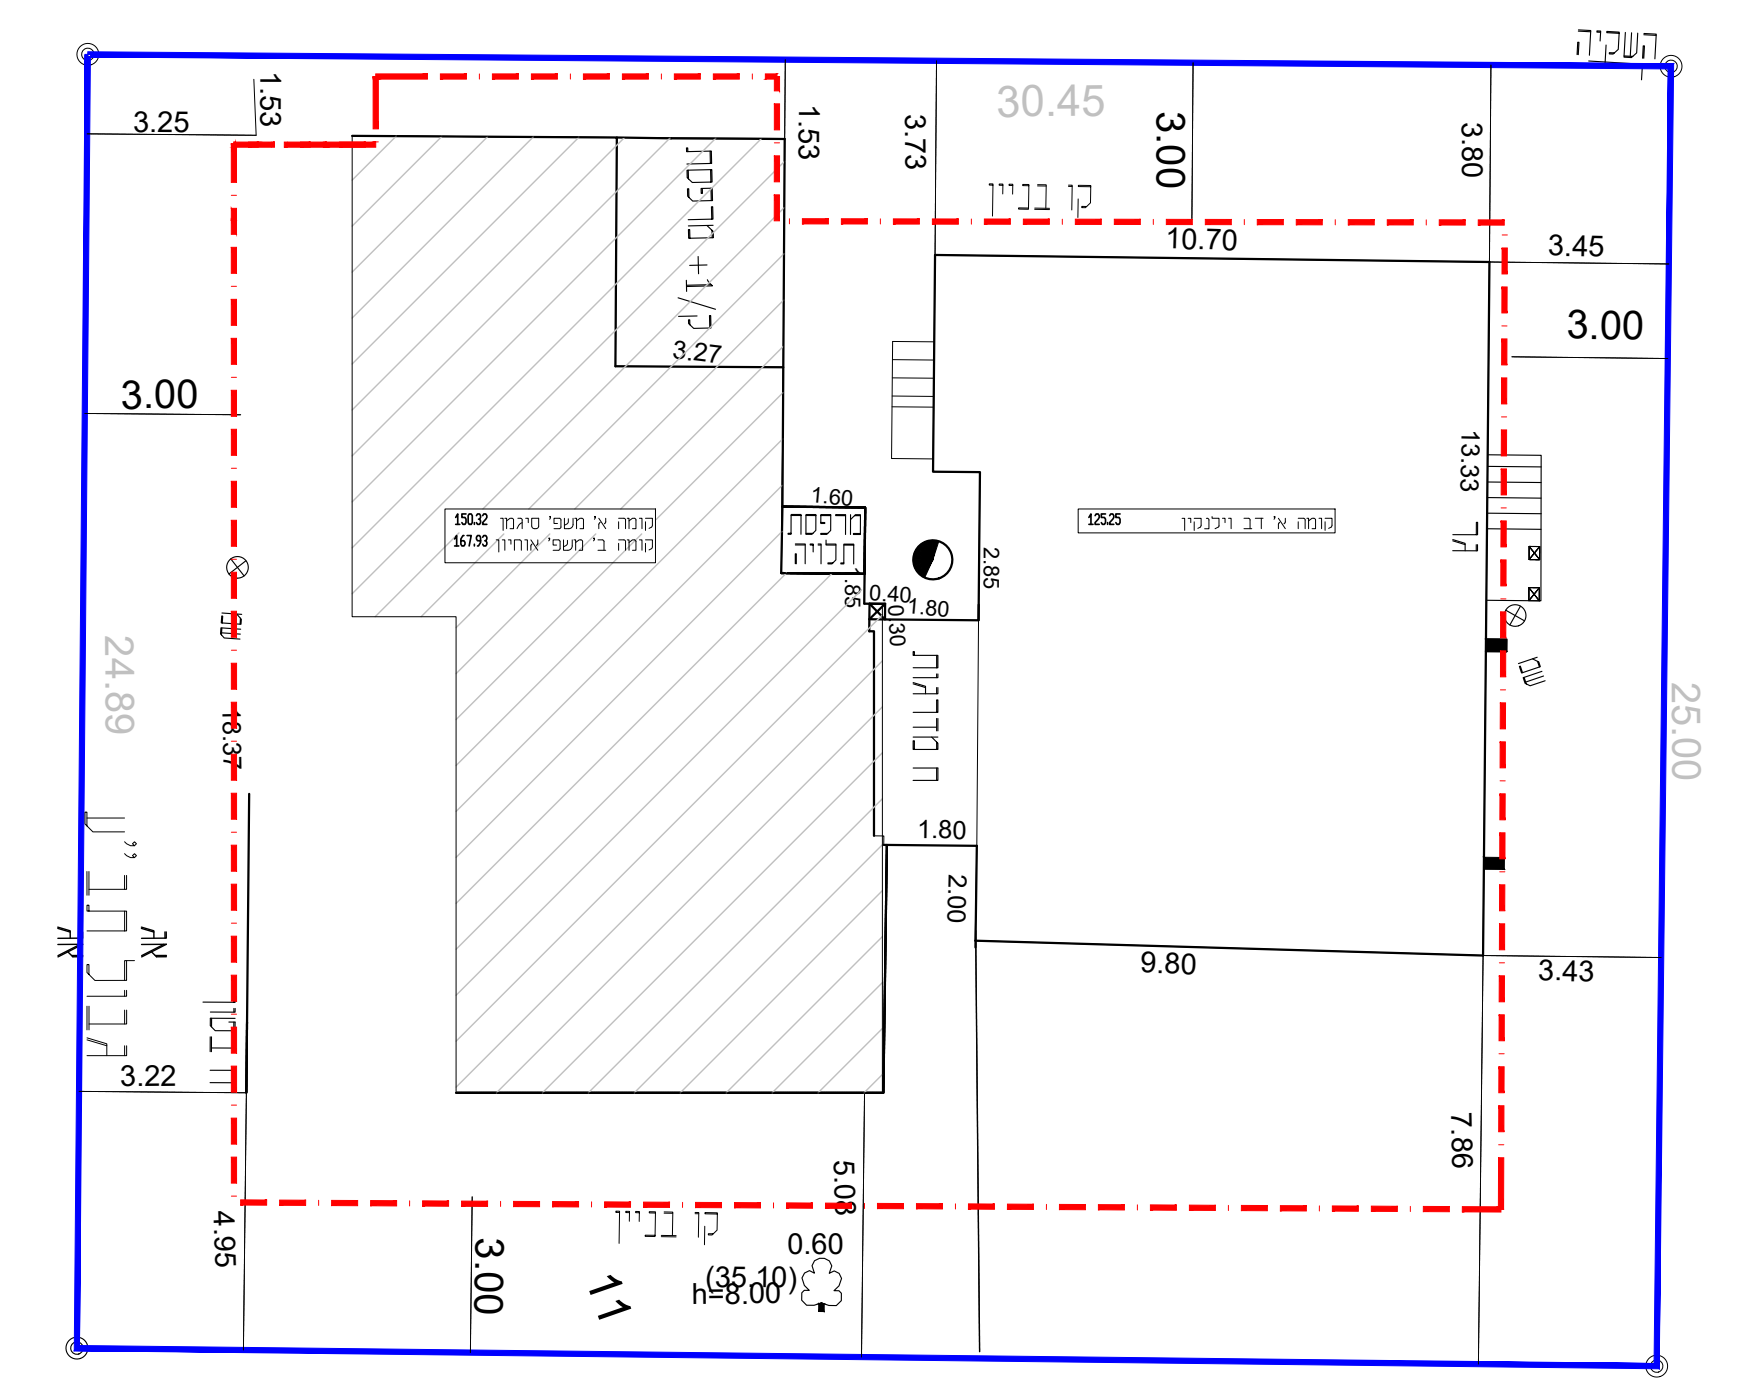
השקיה
30.45
3.00
קו בניין
10.70
3.45
3.00
3.00
24.89
9.80
3.43
3.22
7.86
4.95
3.00
11
0.60
(35.10)
h=8.00
תוכנית מצב קיים קנ"מ 1:100
תוכנית קומה א' וב'

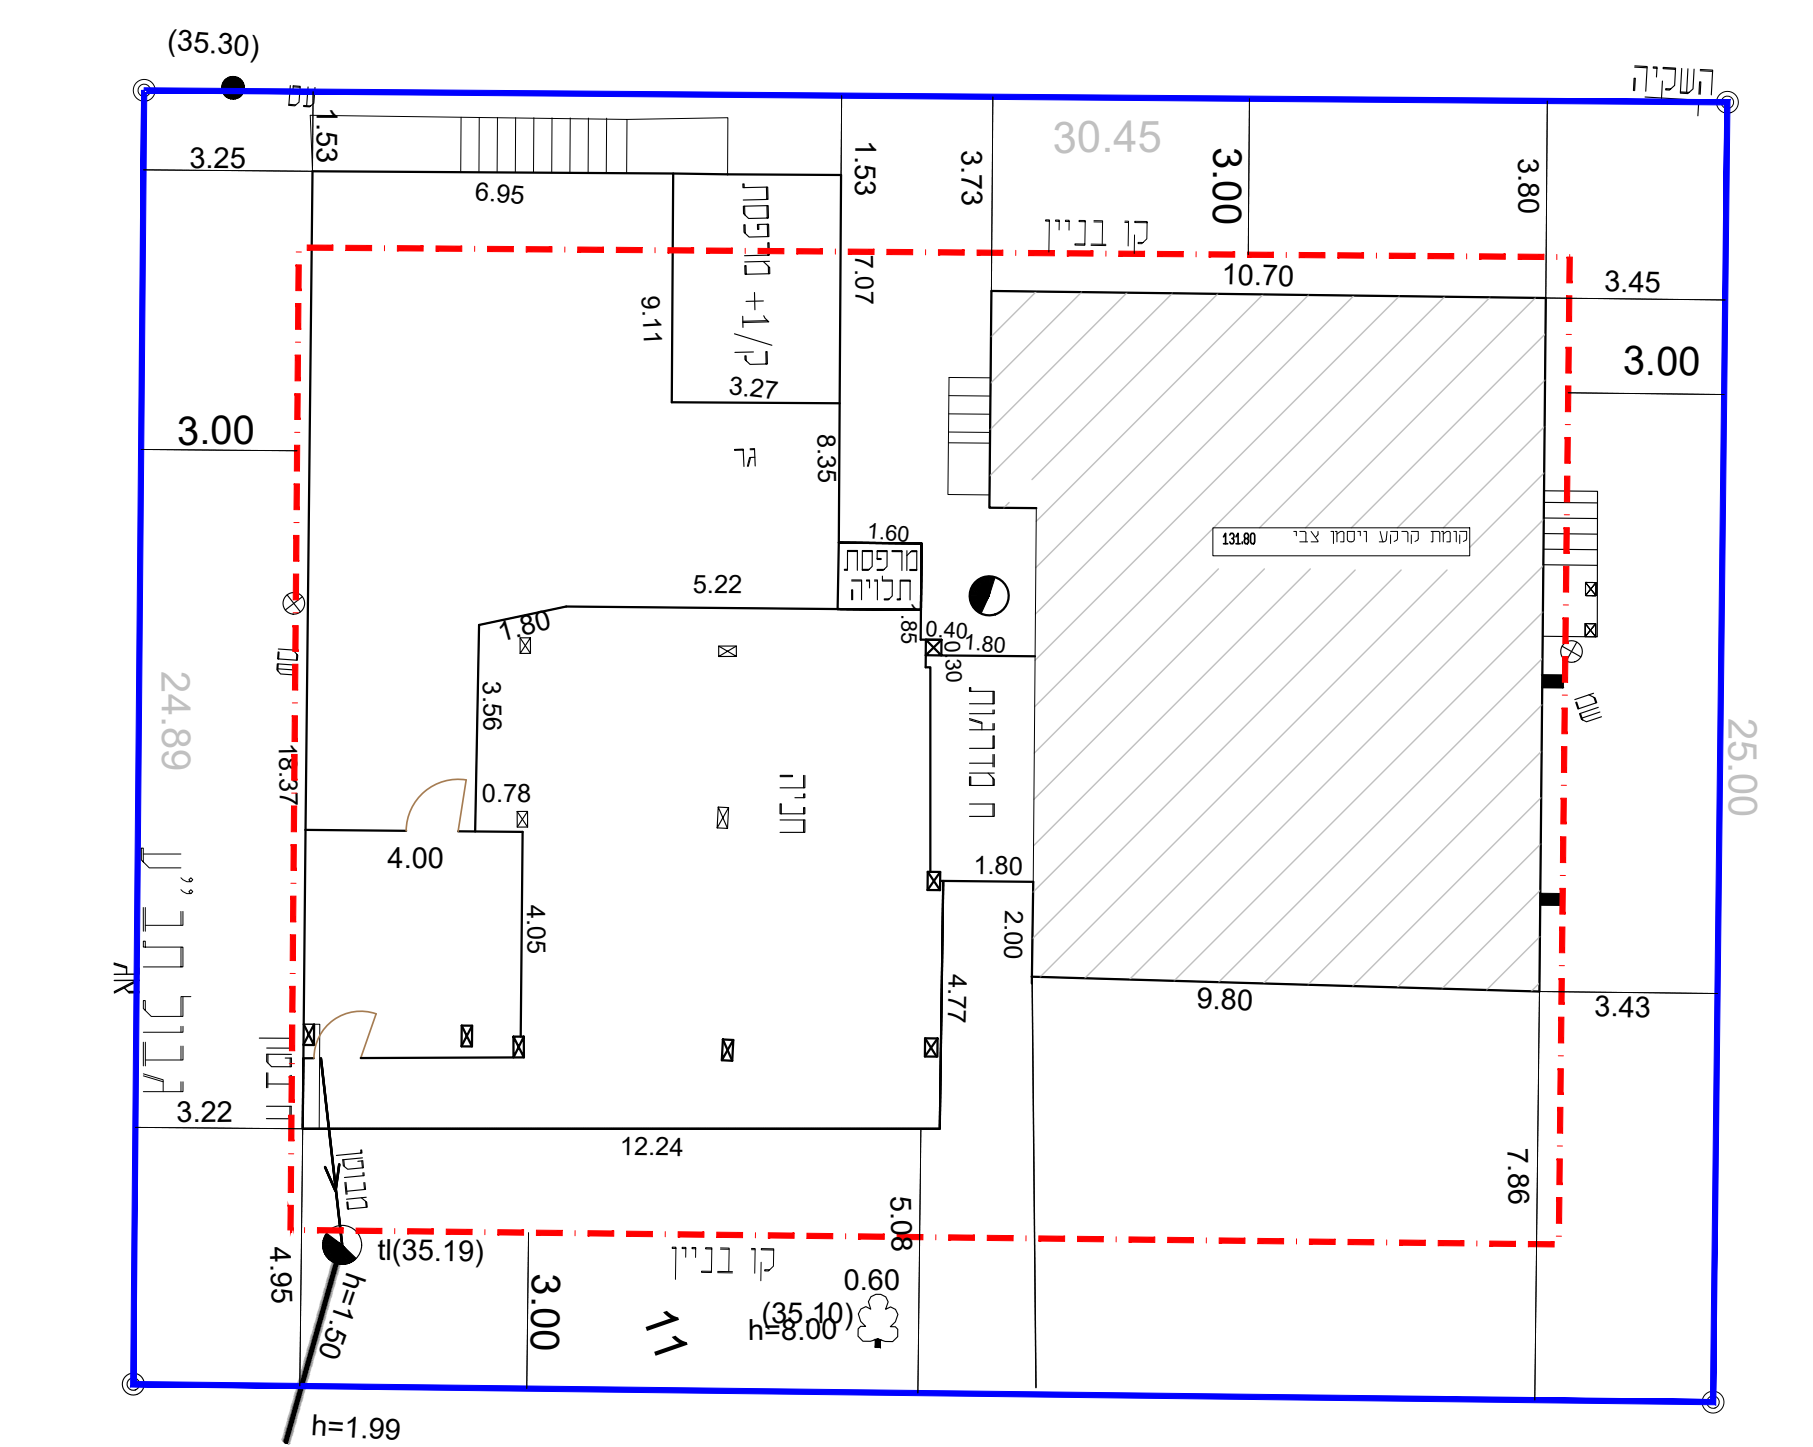
(35.30)
השקיה
30.45
3.00
קו בניין
חניה
4.00
12.24
9.80
3.43
3.22
7.86
4.95
3.00
11
0.60
(35.19)
(35.10)
h=1.50
h=8.00
h=1.99
תוכנית מצב קיים קנ"מ 1:100
תוכנית קומת קרקע

חוק התכנון והבנייה,התשכ"ה–1965
תכנית מתאר מקומית

מס' 425-0800557

שינוי קו בניין אחורי ותוספת קומה מגרש 225
כפר חבד

[redacted]

מחוז	מרכז
מרחב תכנון מקומי	עמק לוד
רשות מקומית	עמק לוד
ישוב	כפר חב"ד
תכנית בסמכות	מקומית
איחוד וחלוקה	ללא איחוד וחלוקה
היתרים או הרשאות	תכנית שמכוחה ניתן להוציא היתרים או הרשאות
מונה תדפיס התשריט	9
מועד הפקה	03/11/2019 00:27
שלב	הגשה / מהדורה 1
שטח התכנית	0.76 דונם / קנה מידה 1:250

אישורים

הפקדה	מתן תוקף
חותמת הועדה המקומית	חותמת הועדה המקומית
שם ותפקיד החותם	שם ותפקיד החותם

שמות וחתימות*

מגיש התכנית	סיגמן יוסף וסימה	חתימה:
עורך ראשי	אמזל הדסה	חתימה:

*לפירוט נוסף יש לפנות להוראות התכנית

טבלאות גושים וחלקות*

מספר גוש	חלק/כל הגוש	מספרי חלקות בשלמותן	מספרי חלקות בחלקיותן
7187	חלק	11	

*לפירוט נוסף יש לפנות להוראות התכנית

הנני מצהיר בזאת כי המפה הטפוגרפית/המצבית המהווה רקע לתכנית זאת,נערכה על ידי ביום_____והיא הוכנה לפי הוראות נוהל מבא"ת ובהתאם להוראות החוק ולתקנות המודדים שבתוקף.דיוקהקו הכחול והקדסטר:
מדידה אנליטית ברמת תצ"ר

שם המודד ________ מספר הרשיון ________ חתימה ________ תאריך ________