
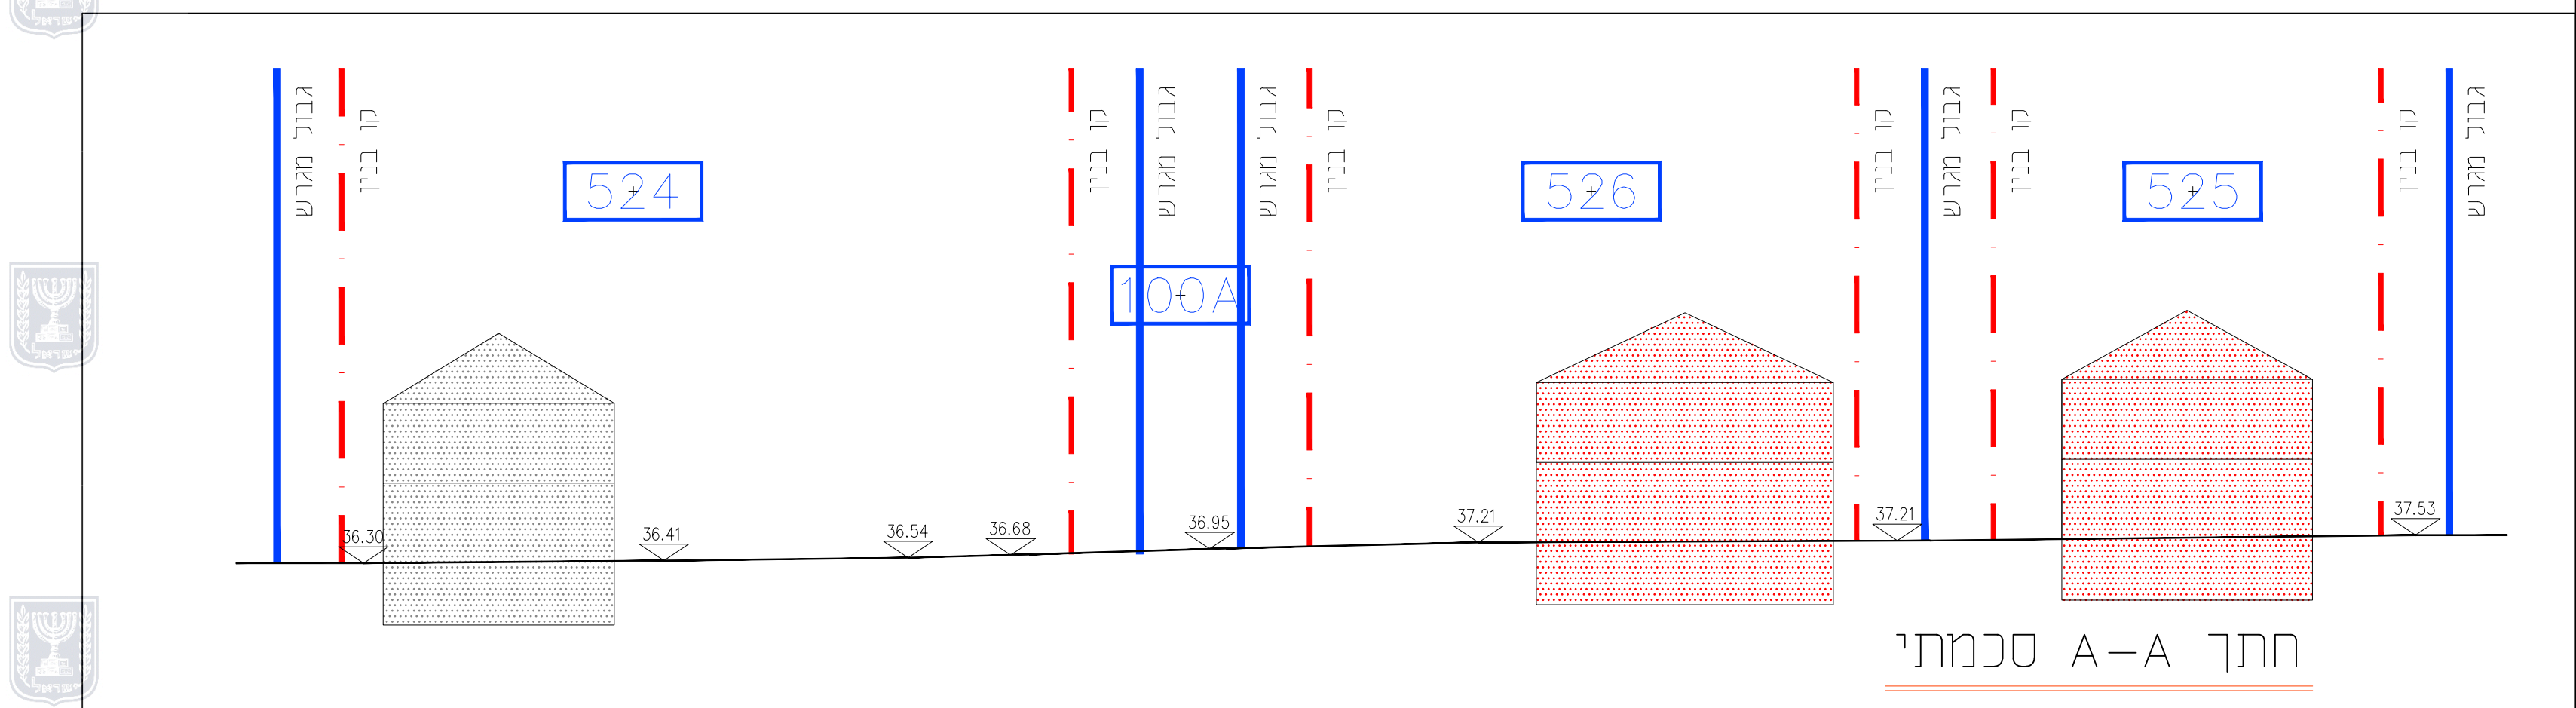


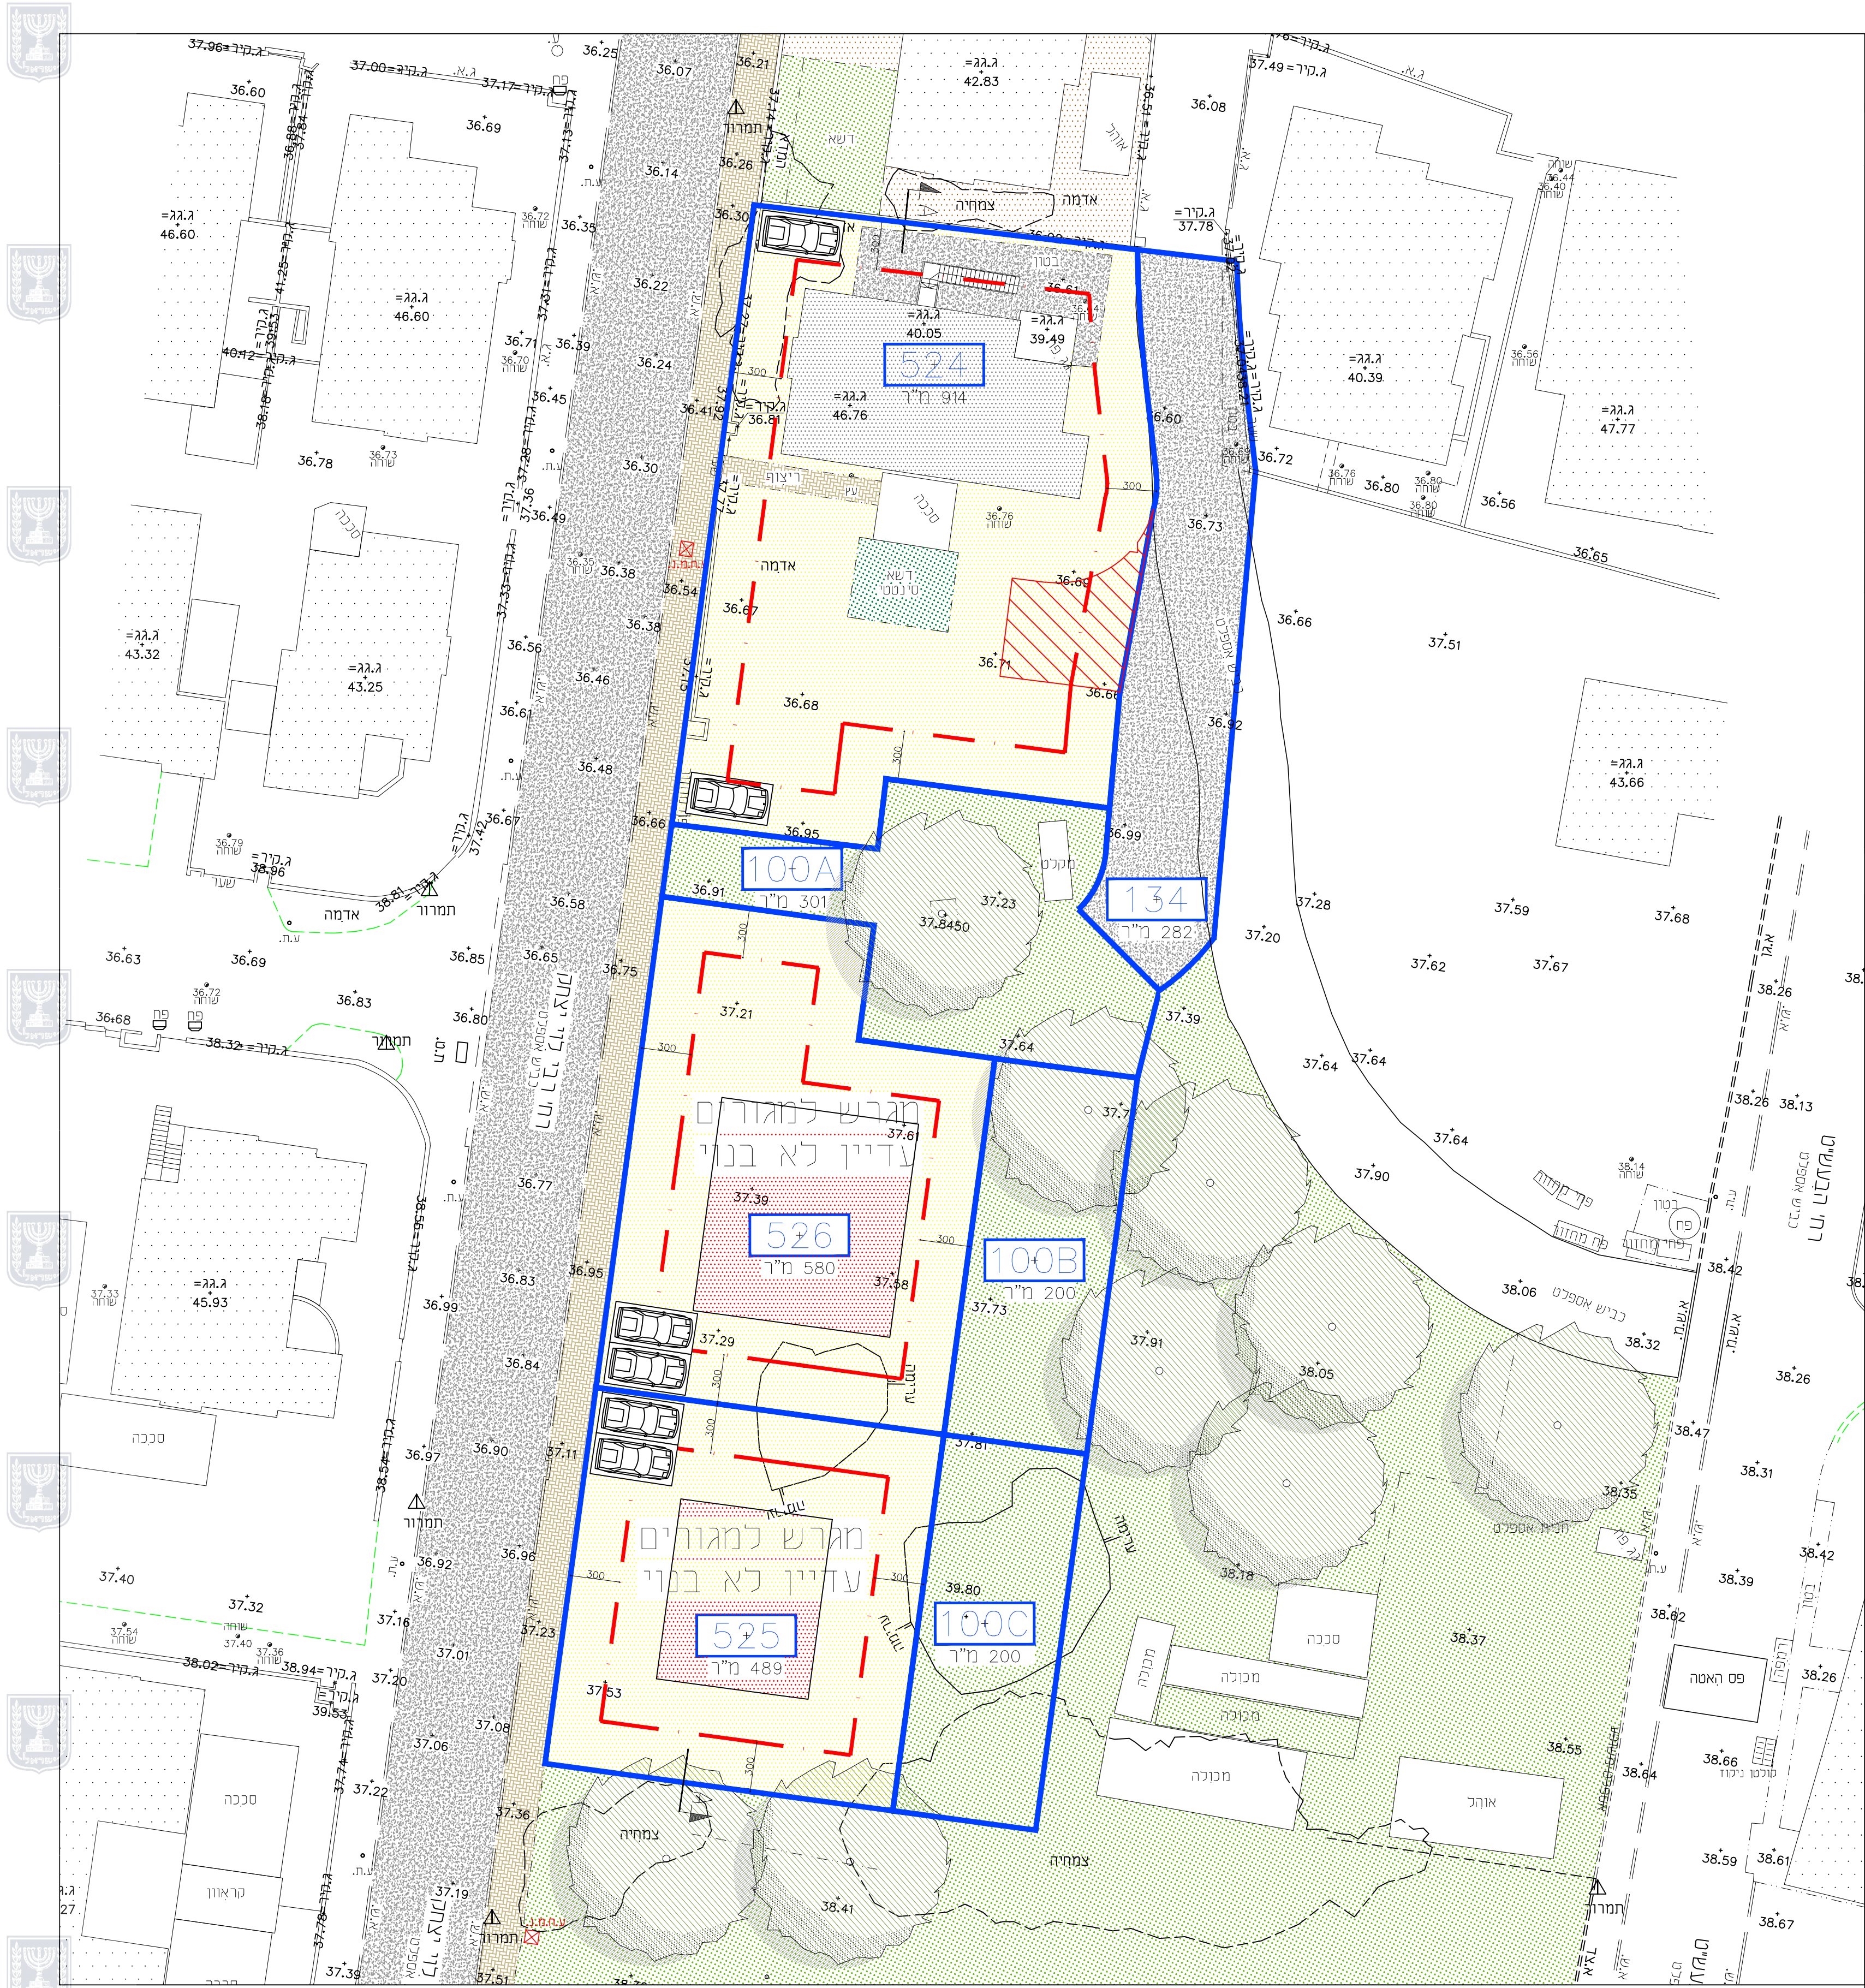

תכנית בינוי

תכנית מס' 425-1279793

איחוד וחלוקה באיזון ל-4 מגרשים
שכונת לוי יצחק כפר חב"ד

נספח מספר 1		גיליון 1 מתוך 1	
תחולה		מנחה	
תיאור תאריך עריכת הנספח		08.09.24	
קנ"מ		1:250	
תרשימים נוספים		קנ"מ	
תכנית כללית		1:250	
חתך A-A		1:250	

שמות וחתימות		שם: רות גרנר	
עורך הנספח		תאגיד: מרומ אדריכלים	



מקרא:

- גבול תכנית
- תא שטח
- מבנה קיים
- מבנה מוצע
- דרך
- שצ"פ
- מגורים מיוחד
- דרך לביטול
- חניה