



1: 100

1: 250

GAA-PRO 17.06



מספר התא בקרה
או נקודה בקו
מרחק בין התאים
או בין נקודות
מרחק מסוכס
רום פני המיכסה (TL)
או פני הקרקע (GL)
רום תחתית הצינור (OL)
עומק תחתית הצינור (H)




שפוט, חומר וקוטר הצינור
File: E:\My Drive\work\2025\5269\hot5269\1
Drawing: E:\My Drive\work\2025\5269\hot5269.dwg
Date: 11/02/25

בית המבקש
חלקה 40


בית שכן
חלקה 41

חתך א א

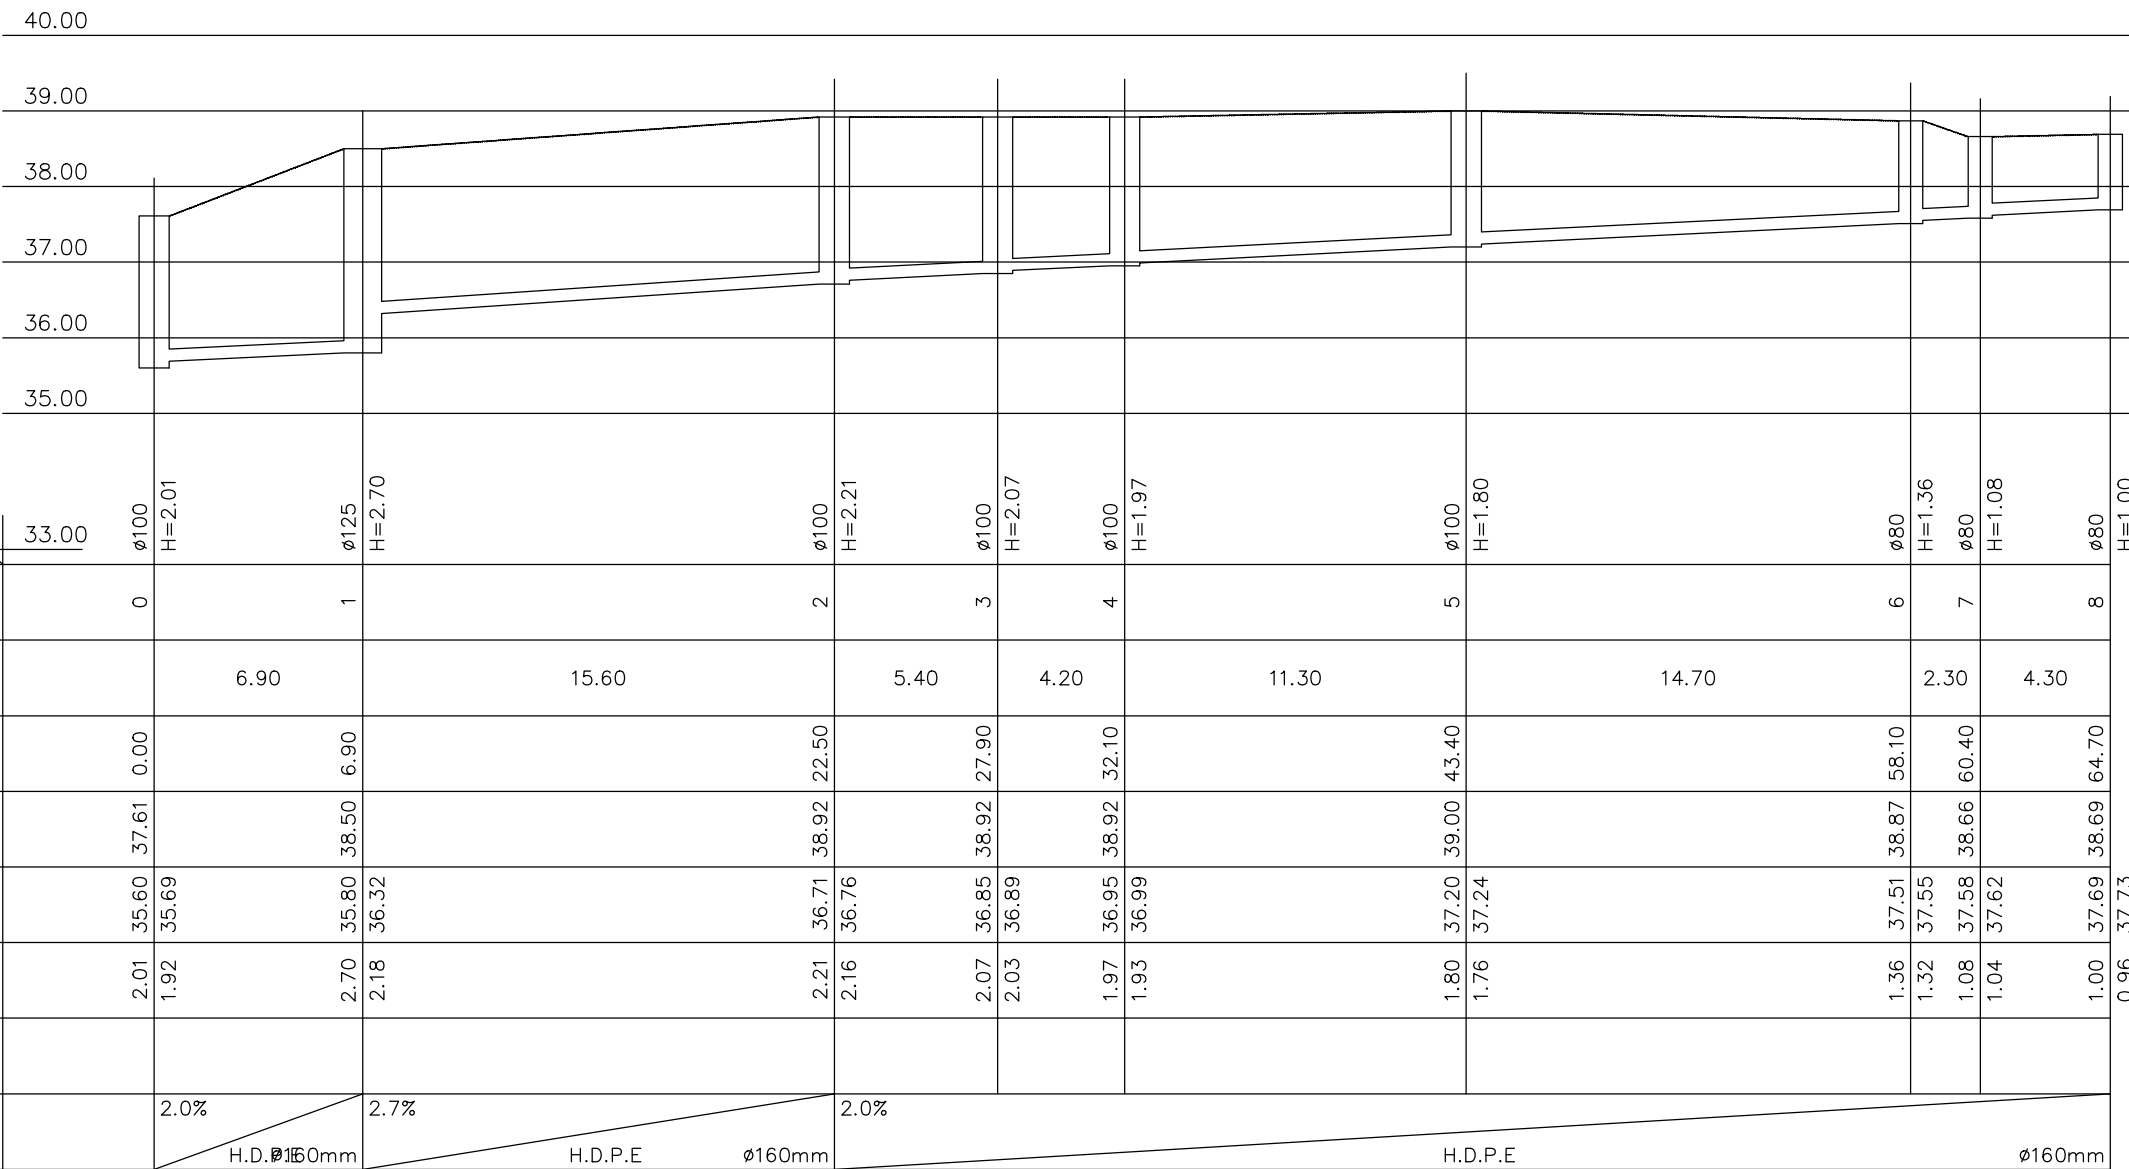


חתך לאורך הביוב

מס' סידורי : 313-2023-0

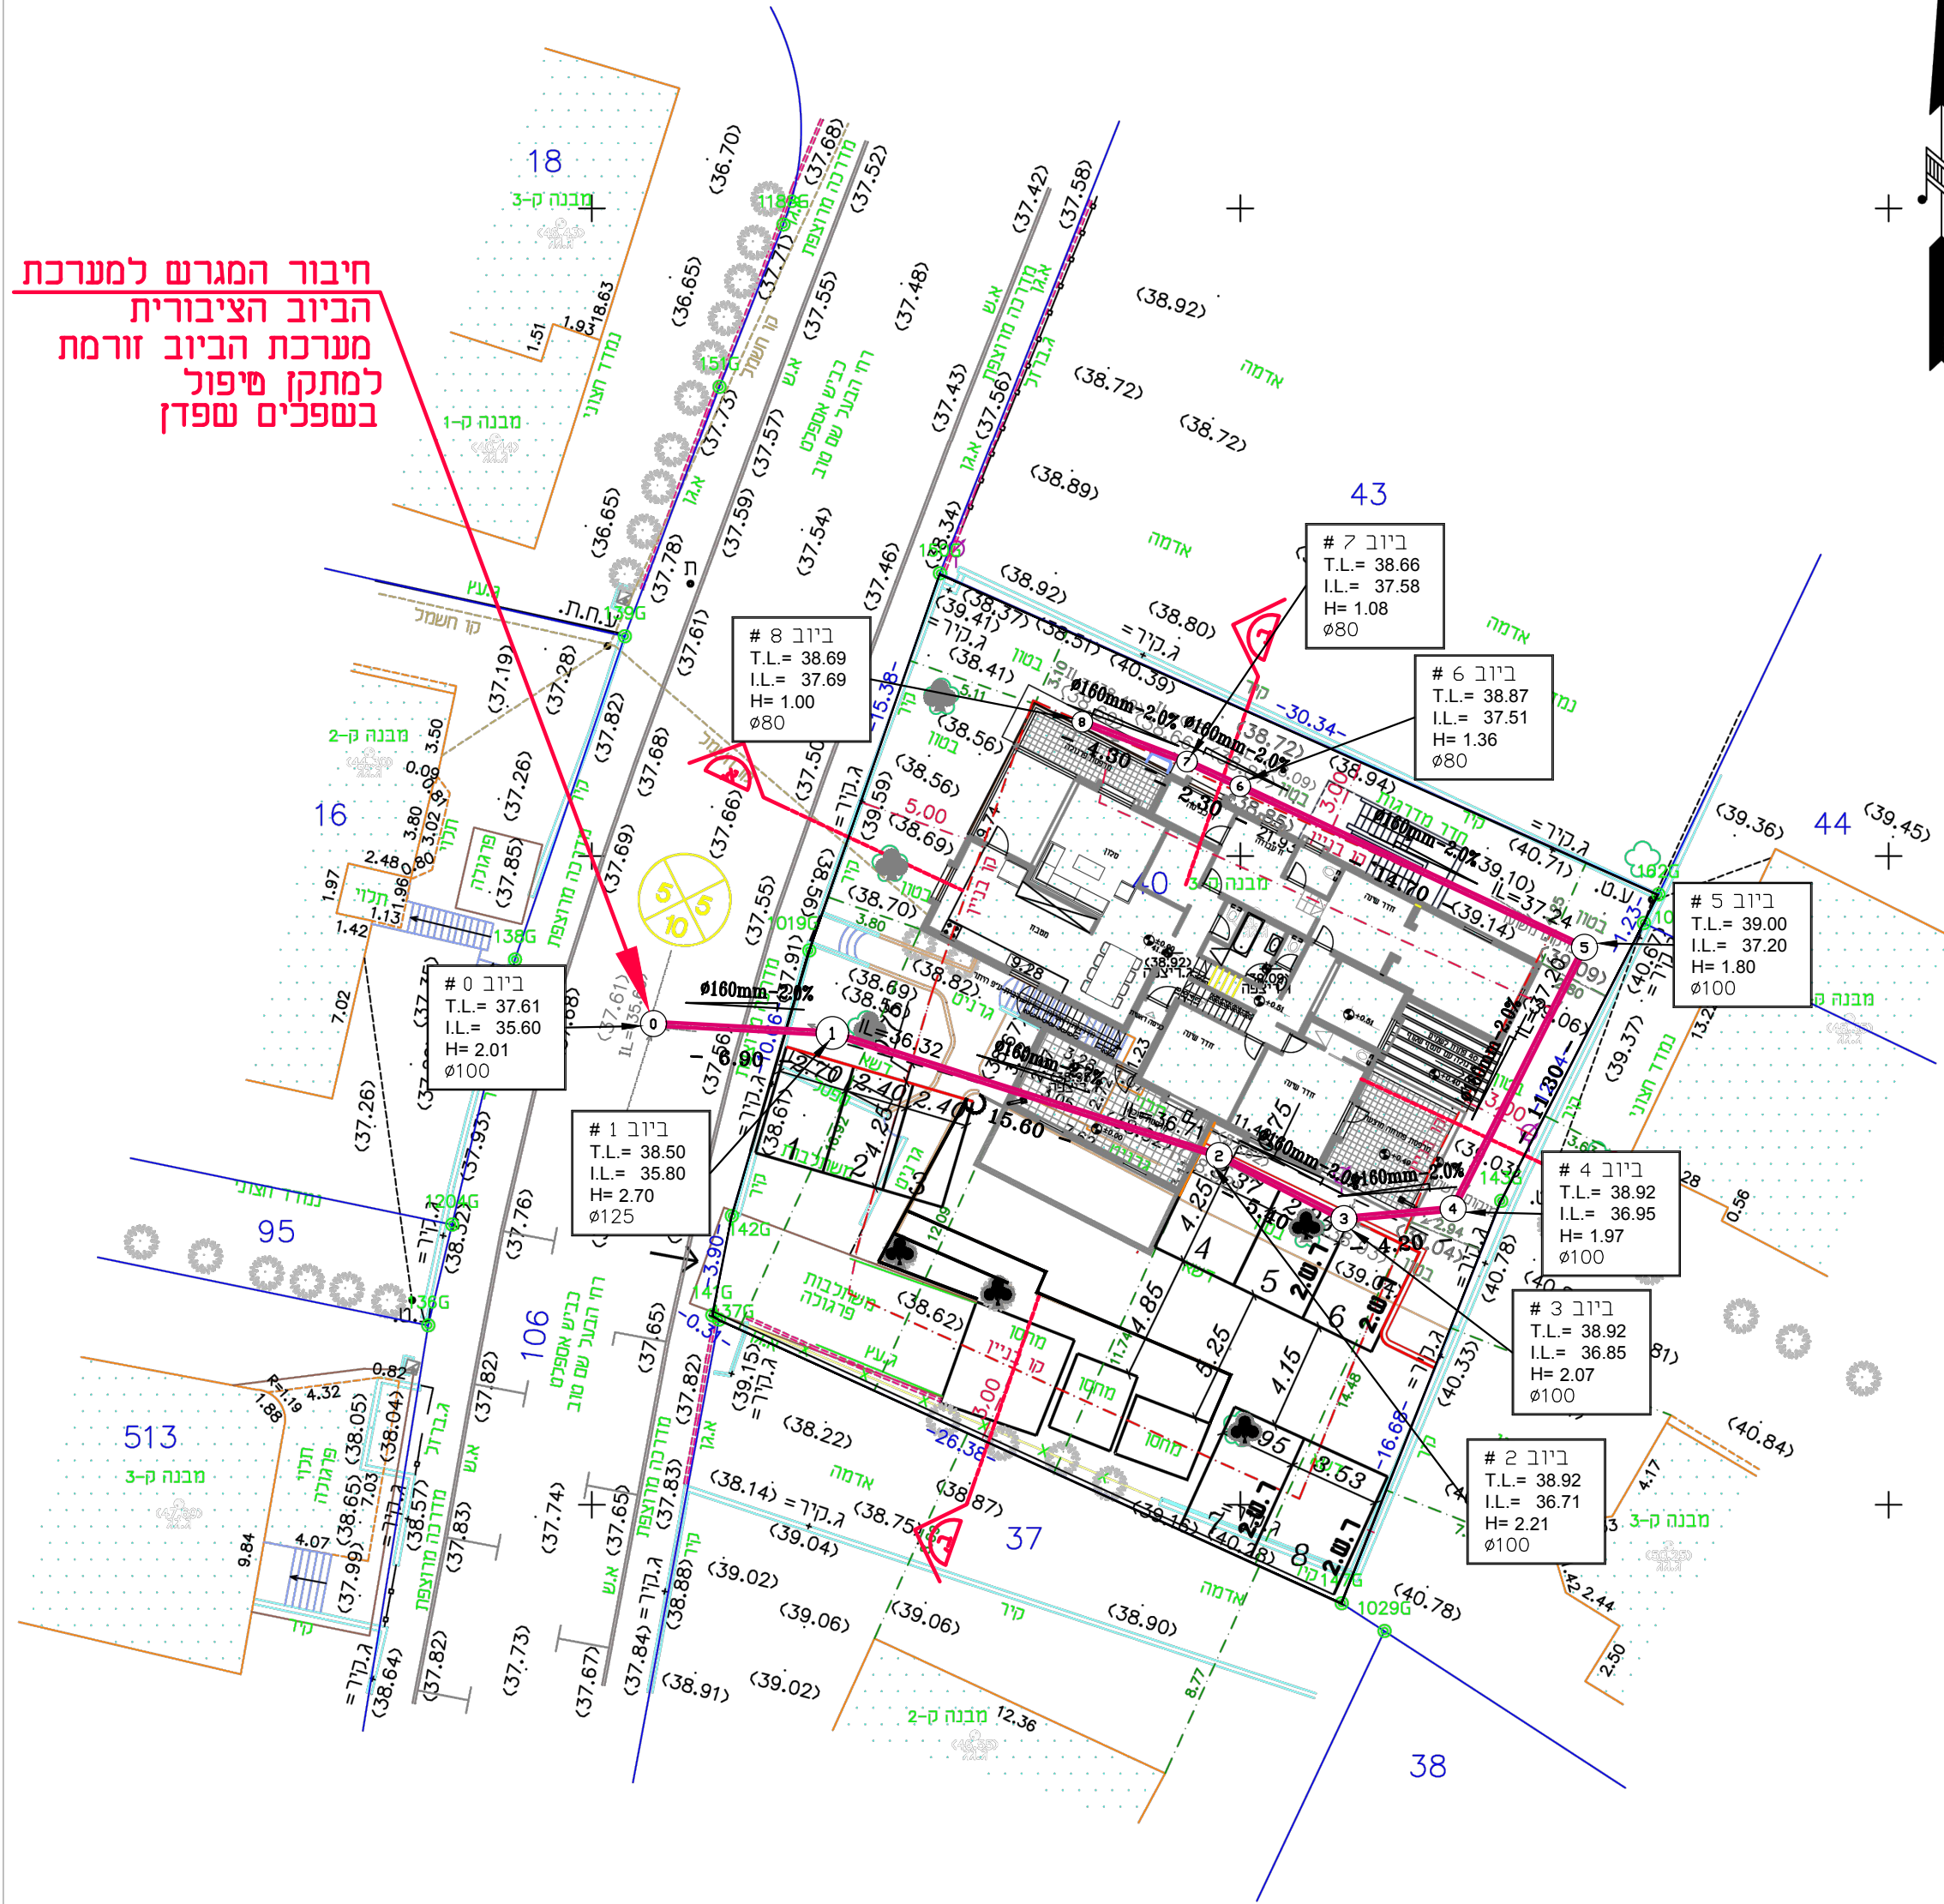

קנה מידה 1 : 250

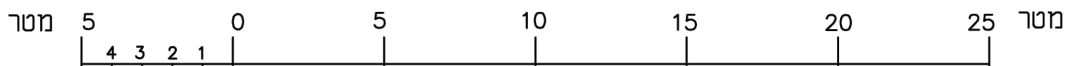

תכנית ביוב

נספח לתכנית מס' 425-1306505

גליון 1 מתוך 1

מנחה

29.01.25

שם: אביחי גולדברג

חתימה

שם:

חתימה: