
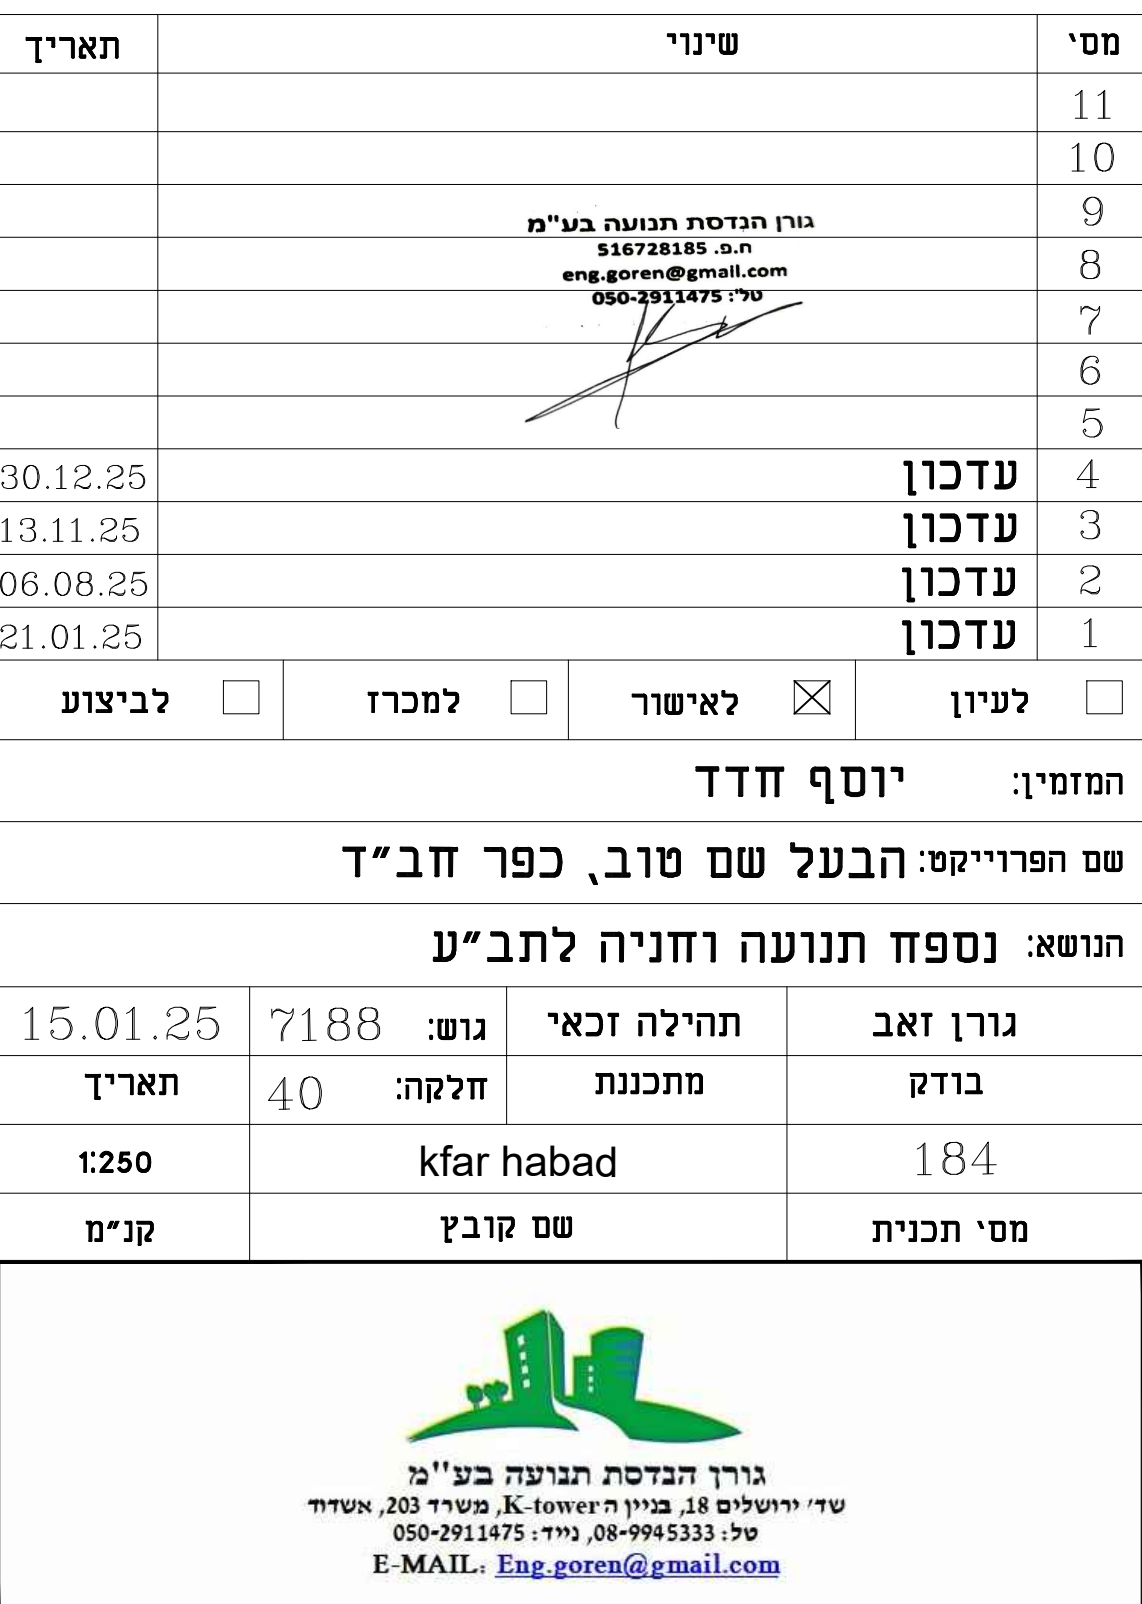


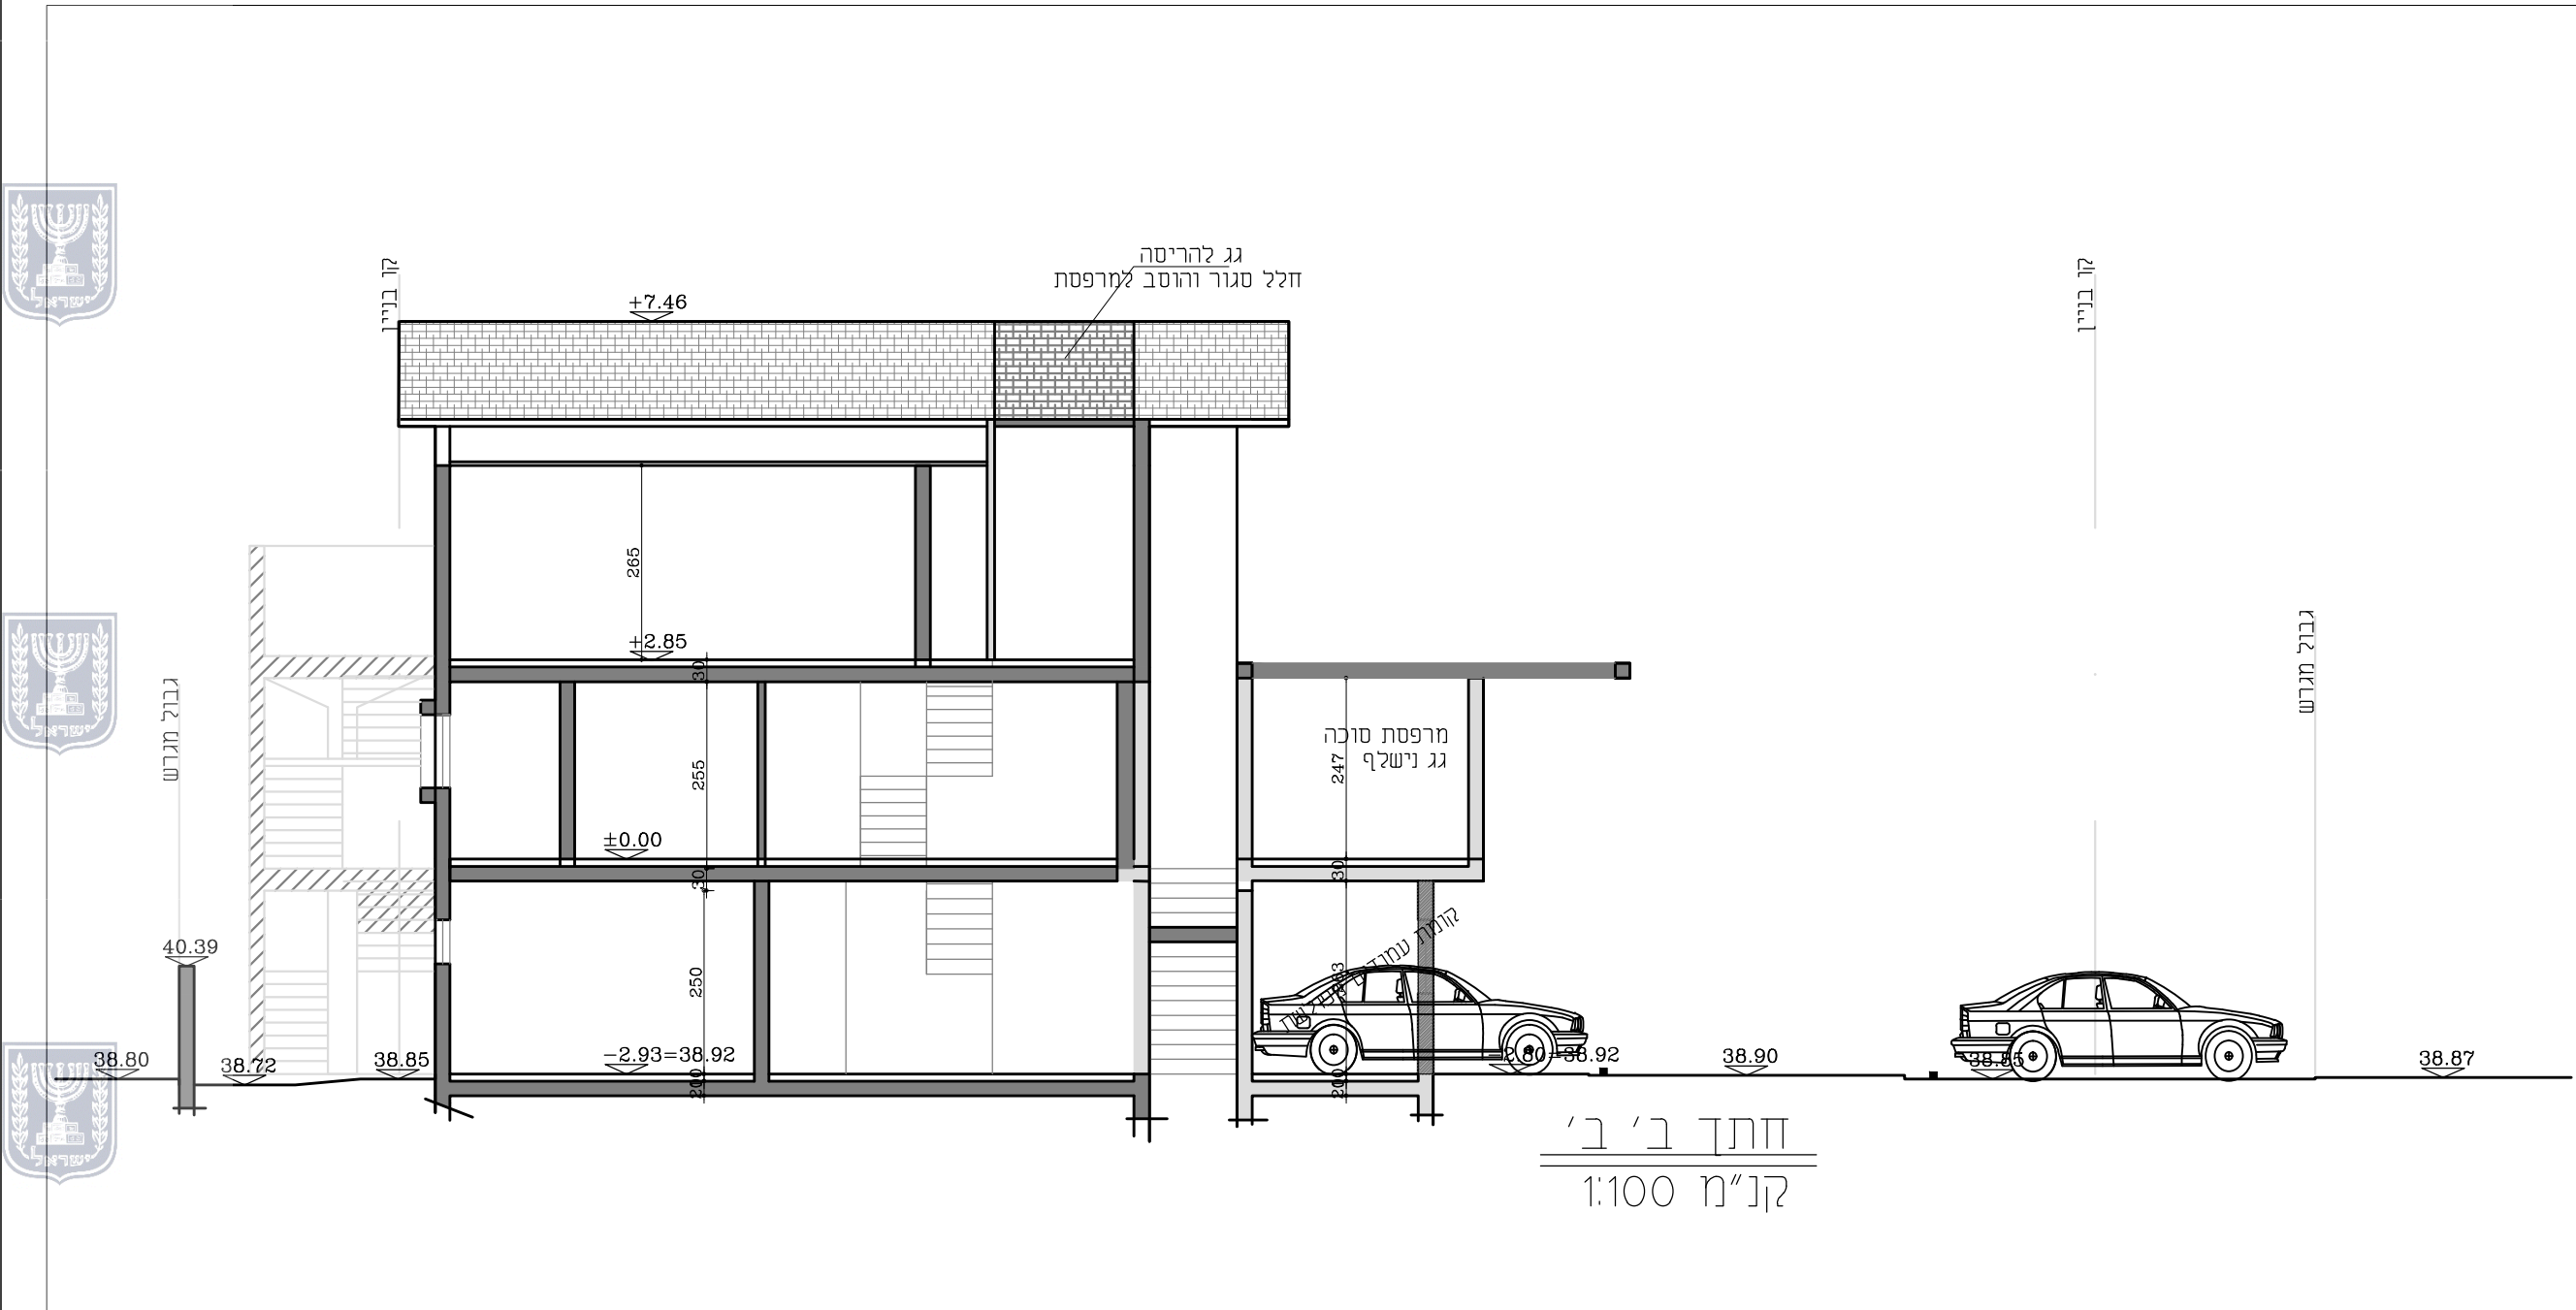

נספח תנועה וחניה	
נספח לתכנית מס' 1306505-425	
הגדלת אחוזי בניה בחלקה 40 מגרש 29 בכפר חב"ד	
גליון 1 מתוך 1	
מנחה	תחולה
	תיאור
13.11.2025	תאריך עריכת הנספח
1:250	קנ"מ
שם: אינג' זאב גורן	עורך הנספח
חתימה אינג' גורן זאב מהנדס תחבורה מ.ר. 55508261	
שם:	
חתימה:	