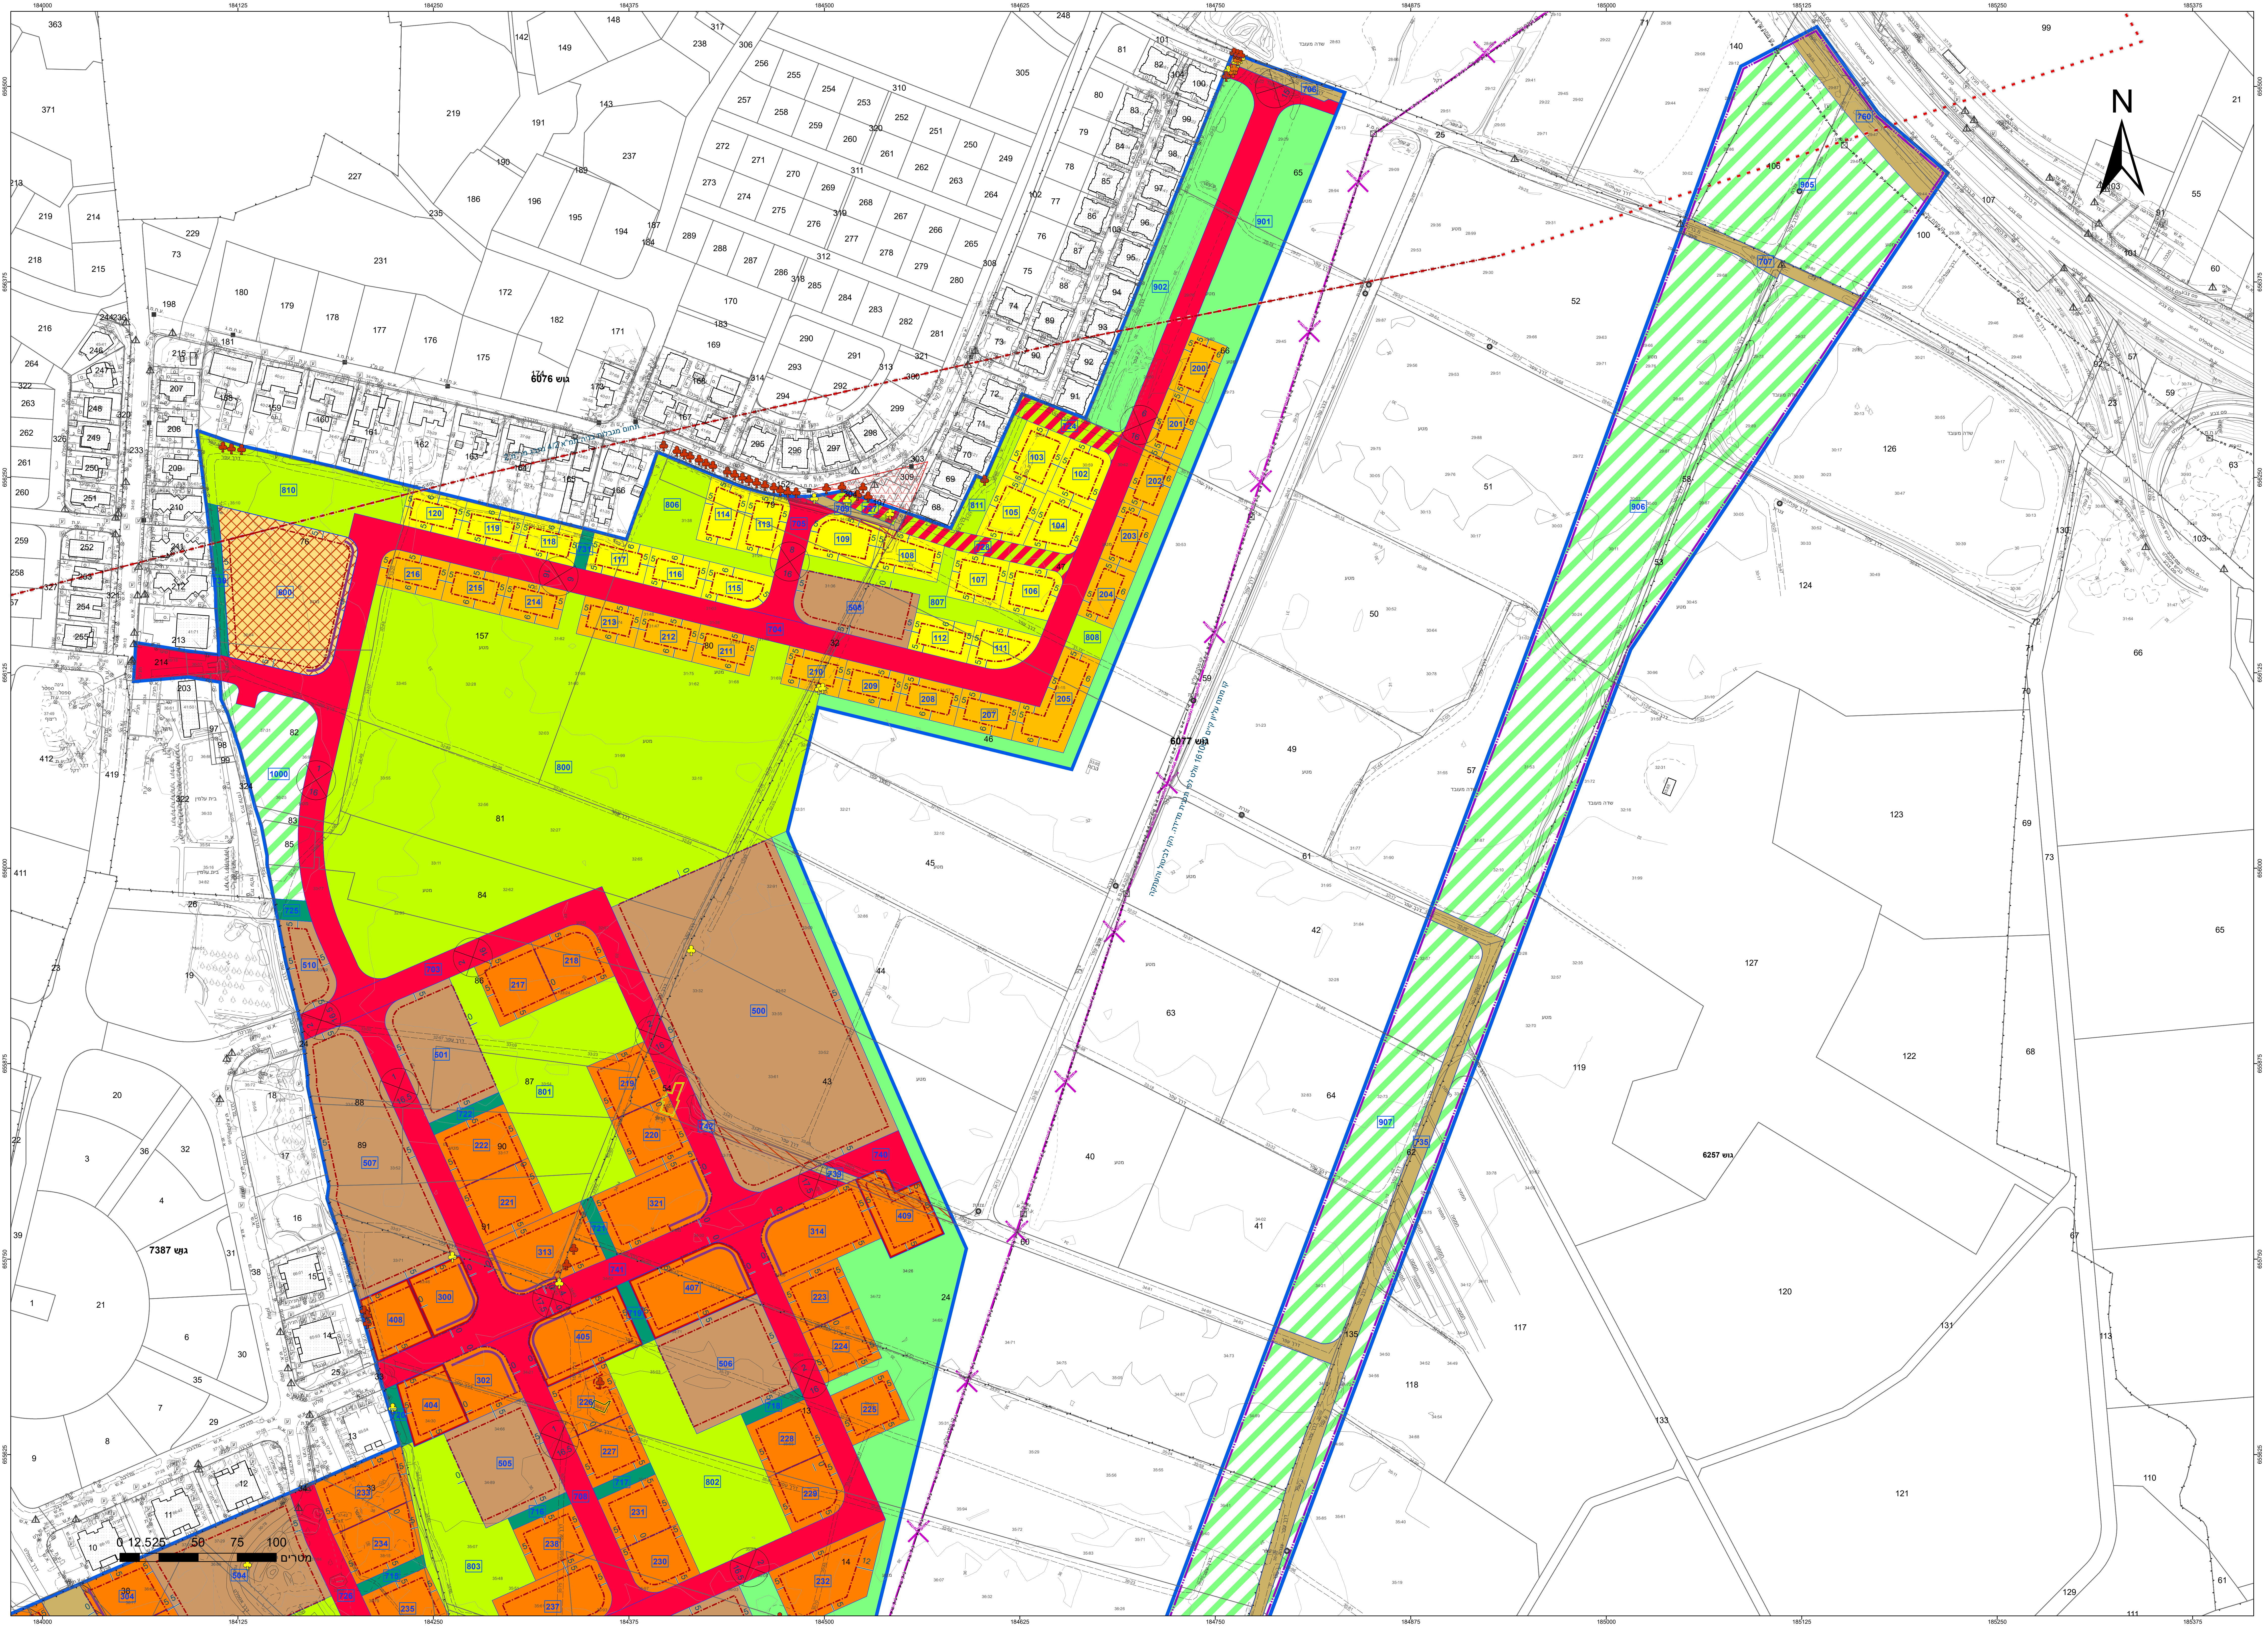

מקרא

▭	גבול תכנית
140	תא שטח ומספרו
גוש 1234	גבול גוש ומספרו
5	גבול חלקה ומספרה
🟨	מגורים א
🟧	מגורים ב
🟧	מגורים ג
🟥	מגורים ד
▨	דיור מיוחד
🟫	מבנים ומוסדות ציבור
🟩	שטחים פתוחים
▨	קרקע חקלאית
🟩	שטח ציבורי פתוח
🟫	דרך מאושרת
🟥	דרך מוצעת
▨	דרך משולבת
🟩	שביל
▨	חורשה לשימור
▭	גבול מגבלות בניה
▨	הנחיות מיוחדות
▨	דרך/מסילה לביטול
▭	גבול מסדרון תשתיות עילי
—	קו-בנין
—	חזית מסחרית
—	להריסה
— עליון	קו חשמל מתח עליון
—	מידות
♣	עץ/עצים לשימור
♣	עץ/עצים להעתקה
♣	עץ/עצים לכריתה

תרשים התמצאות - קנ"מ 1:36000

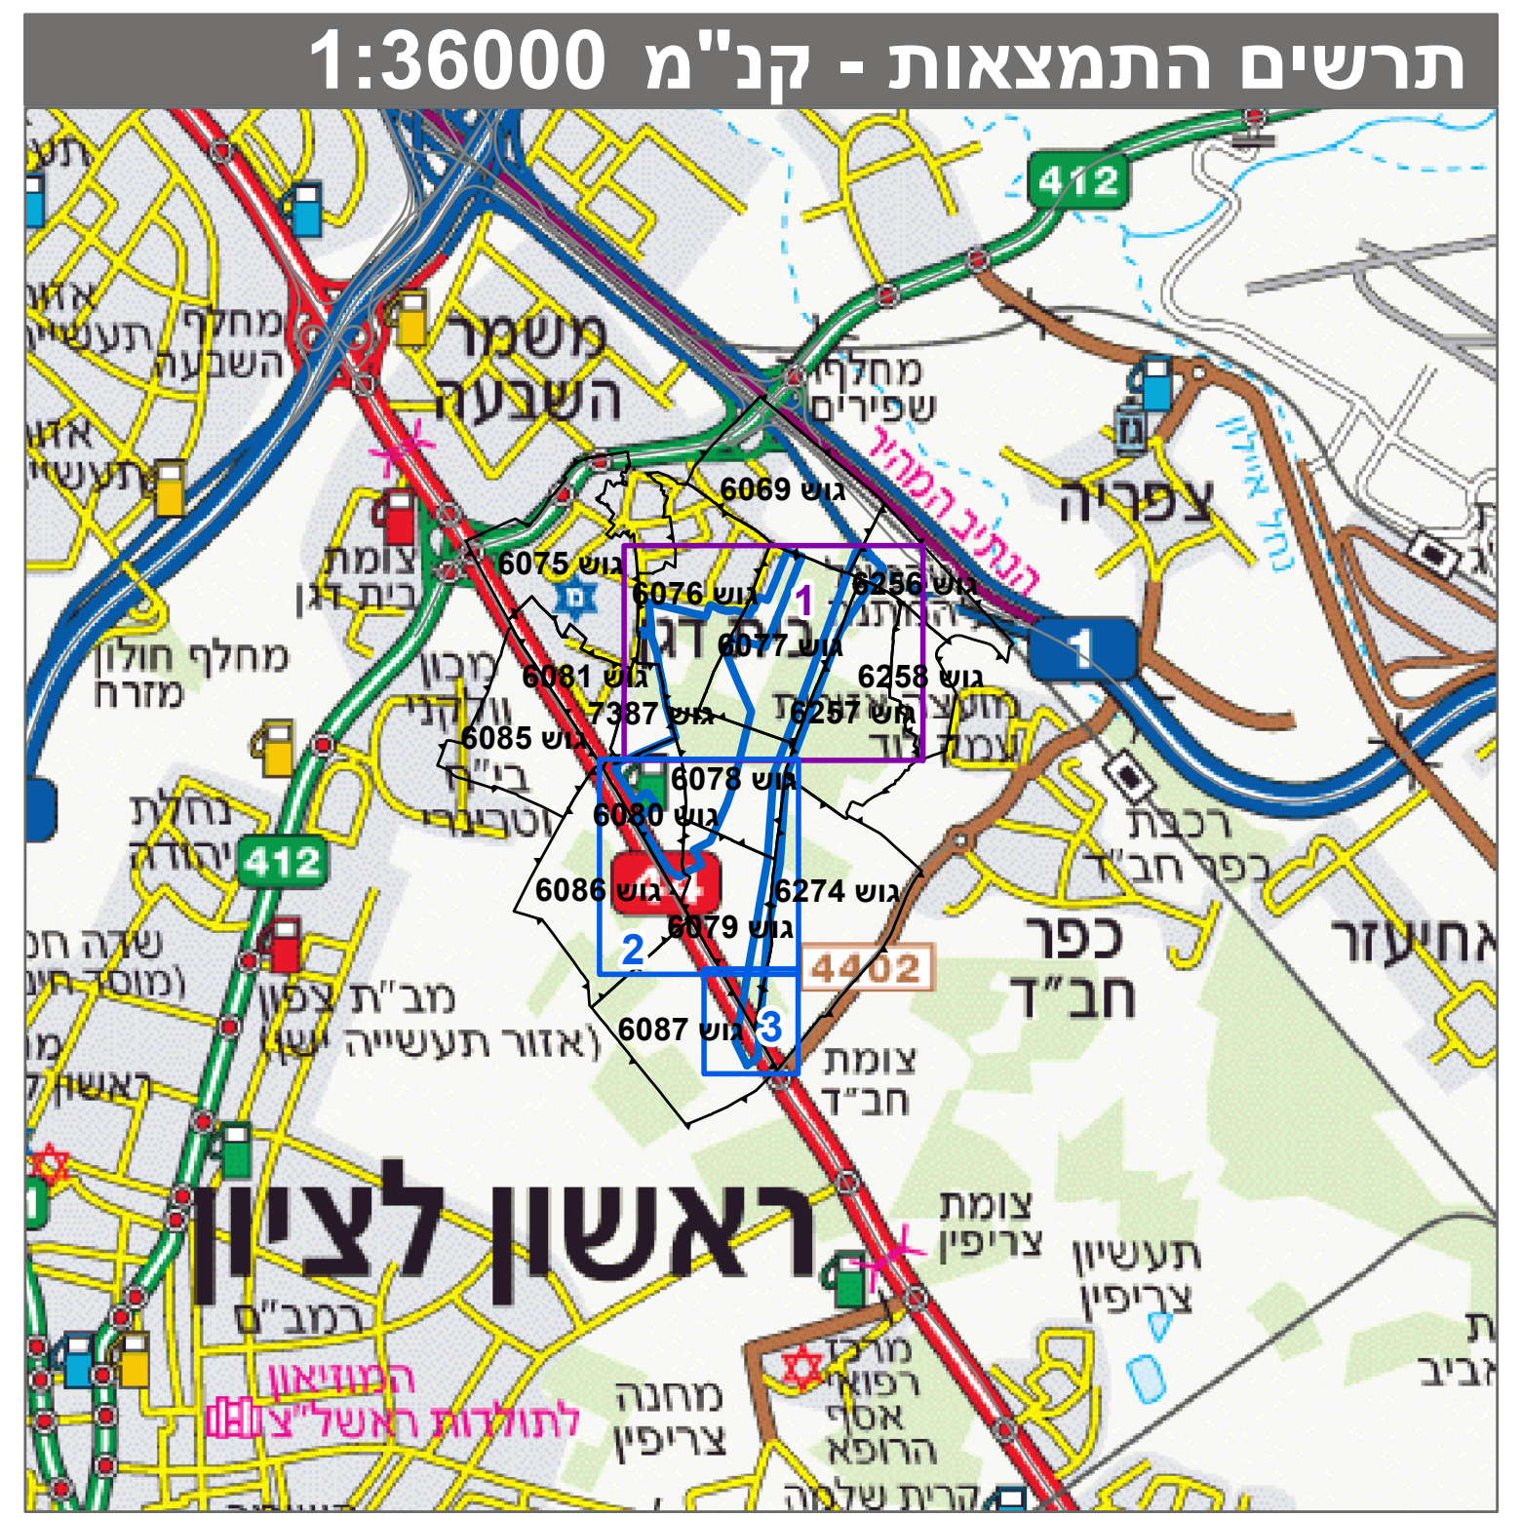

שנת צילום אויר: 2019

תרשים סביבה - קנ"מ 1:9000

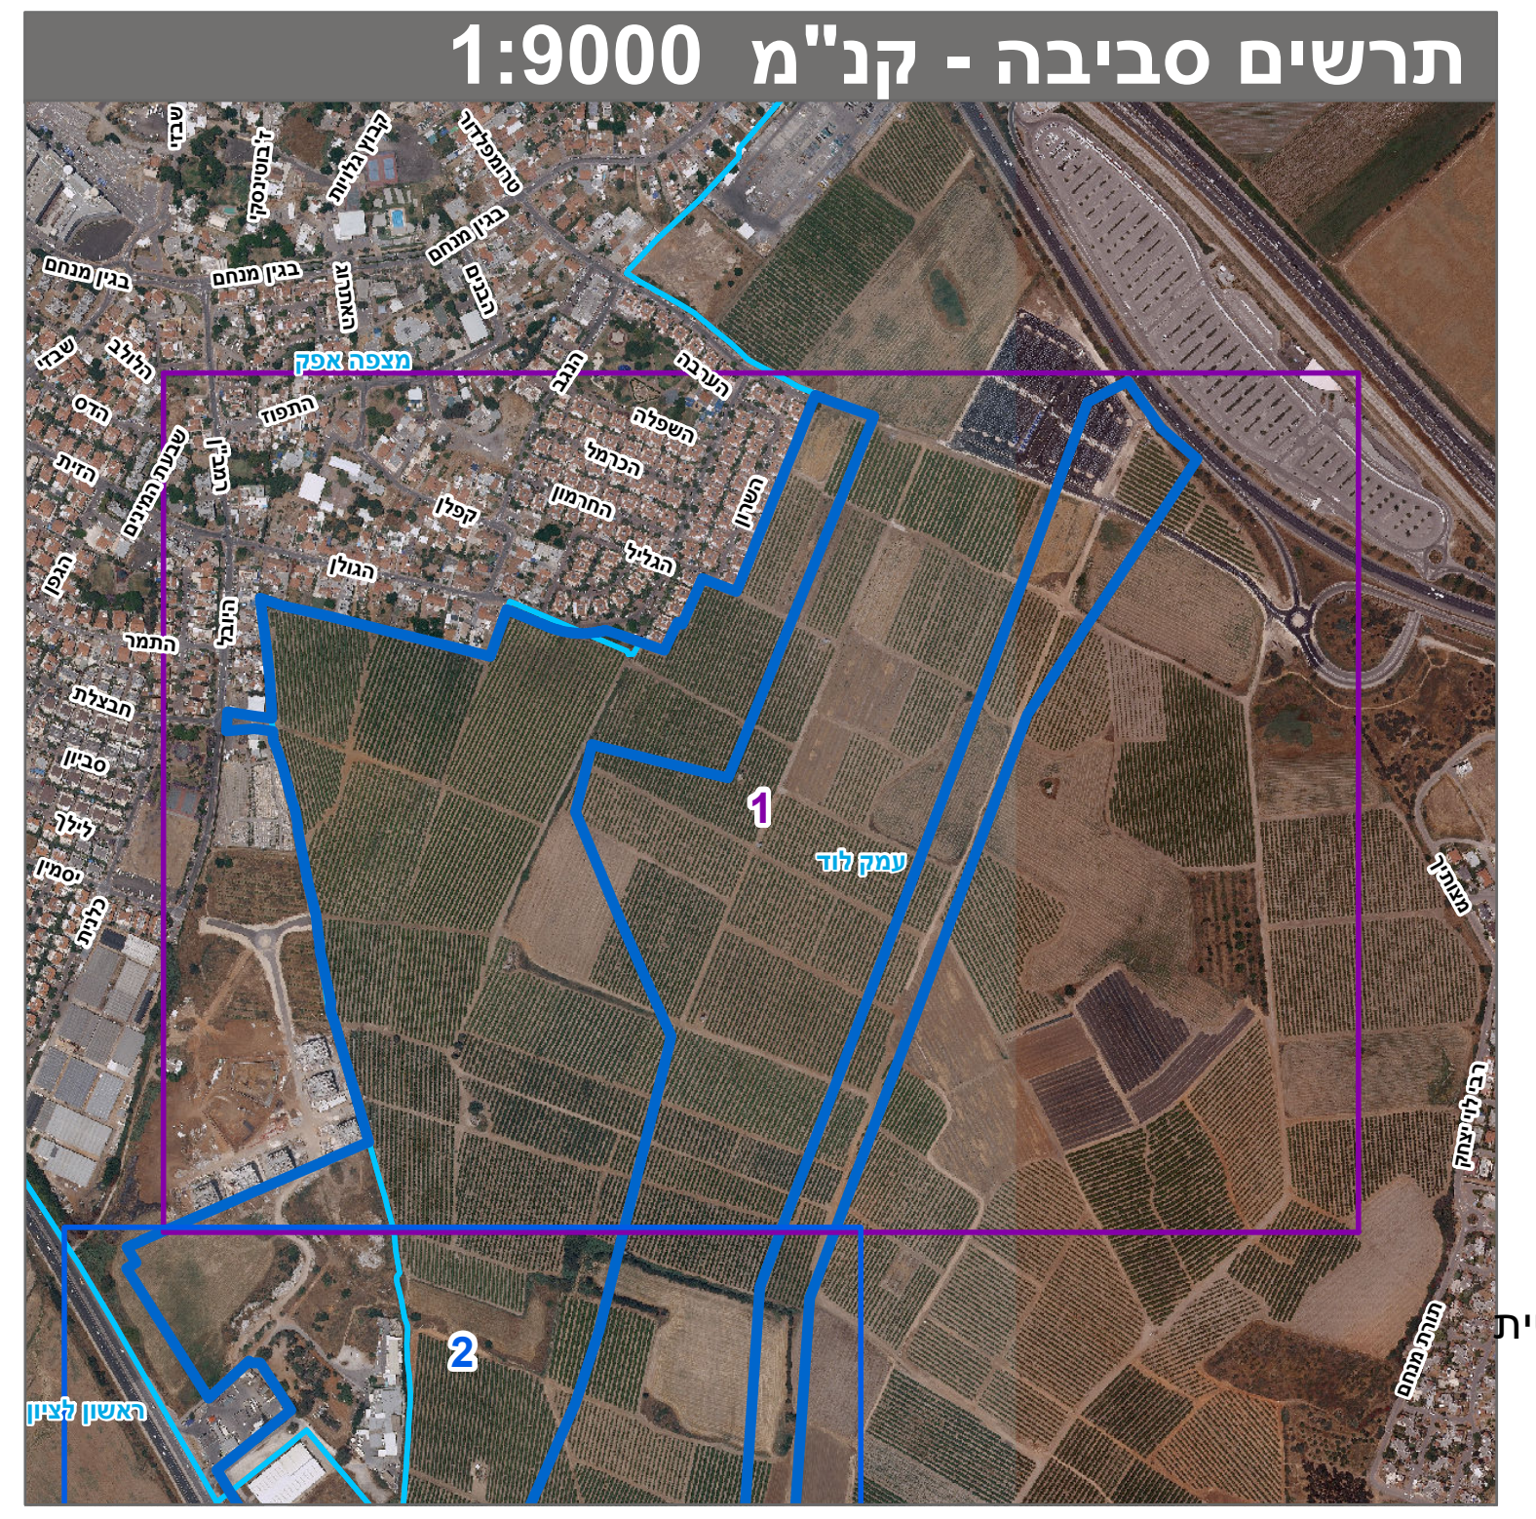

חוק התכנון והבניה, התשכ"ה - 1965
תכנית מתאר מקומית

מס' 455-0812289

בית דגן שכונת האתרוג

תשריט מצב מוצע	גיליון 1 מתוך 3
מחוז	מרכז
מרחב תכנון מקומי	מצפה אפק, ראשון לציון, שדות דן
רשות מקומית	בית דגן, ראשון לציון, שדות דן
ישוב	בית דגן
תכנית בסמכות	מחוזית
איחוד וחלוקה	איחוד ו/או חלוקה ללא הסכמת כל הבעלים בכל תחום התכנית/בחלק מתחום התכנית
היתרים או הרשאות	תכנית שמכוחה ניתן להוציא היתרים או הרשאות
מונה תדפיס התשריט	35
מועד הפקה	04/11/2024 16:10
שטח התכנית	706.568 דונם — קנה מידה 1:1250

אישורים

מינהל התכנון
חוק התכנון והבניה, התשכ"ה - 1965
מחוז מרכז
הוועדה המחוזית החליטה ביום :
07/02/2024
לאשר את התוכנית
07/11/2024
תאריך יו"ר הוועדה המחוזית

שמות*

מגיש התכנית	משרד הבינוי והשיכון תאגיד: משרד הבינוי והשיכון
עורך ראשי	יחיאל קורין תאגיד: יחיאל קורין אדריכלים בע"מ
יזם	משרד הבינוי והשיכון תאגיד: משרד הבינוי והשיכון

טבלת גושים וחלקות*

מספר גוש	חלק/ כל הגוש	מספרי חלקות בשלמותן	מספרי חלקות בחלקיותן
6069	חלק		140
6076	חלק	76, 81-91, 157, 214	32, 79-80, 107, 152, 203, 213, 304, 324
6077	חלק	53-54, 58, 62	24-25, 41-47, 51-52, 57, 60-61, 64-66
6078	חלק	3-4, 18, 20, 22	13-14, 16-17, 19, 21, 23-25
6079	חלק	2, 25-26, 28-29	1, 3-6, 8-12, 14, 23-24, 27, 30
6080	חלק	6-8, 12-13, 15, 25-26, 33, 35, 38, 40, 42, 49	11, 16-24, 31, 45
6087	חלק		1, 6
6256	חלק		100, 106-107
6257	חלק		1, 116-119, 124-127, 133-135
6274	חלק	135	97-99, 104-105, 117, 124-125, 127, 130-131, 134

* הרשימה המלאה מפורטת בהוראות התכנית / בהודעה שפורסמה בעיתונות וברשומות

הריני מצהיר בזאת כי המפה הטופוגרפית/המצבית המהווה רקע לתכנית זו, נערכה על ידי ביום 03.08.2024 והיא הוכנה לפי הוראות נוהל מבא"ת ובהתאם להוראות החוק ולתקנות המודדים שבתוקף. דיוק הקו הכחול והקדסטר: קו כחול (בלבד) ברמה אנליטית

שם המודד	מספר רשיון	חתימה	תאריך
אלדב נטוביץ`	1004		

מספר תכנית: 455-0812289, מספר גירסת תשריט: 35