חוק התכנון והבנייה, התשכ"ה – 1965
תכנית מתאר ארצית

מסי תמא\4\2\א\2

מחלף כניסה מערבי לנמל התעופה בן גוריון

נספח ה' - חתכי רוחב נופיים אופייניים גליון 2 מתוך 2

מחוז	מרכז
מרחב תכנון מקומי	עמק לוד
רשות מקומית	מ.א. עמק לוד
ישוב	כפר חב"ד
תכנית בסמכות 1	ארצית
איחוד וחלוקה	ללא איחוד וחלוקה
היתרים או הרשאות	תכנית שמכוחה ניתן להוציא היתרים או הרשאות
מונה תדפיס התשריט	8
מועד הפקה	23.07.2017
שלב	הגשה
מהדורה	8
שטח התכנית	532.699 דונם
קנה מידה	1:2,500 1:250

אישורים

שמות :

עורך ראשי אבי שרייבר
תאגיד: דגש הנדסה

יזם חברה ממשלתית
תאגיד: נתיבי ישראל בע"מ

בעלי ענין בקרקע
מדינת ישראל ואחרים

תרשים התמצאות-קנ"מ 1:60000

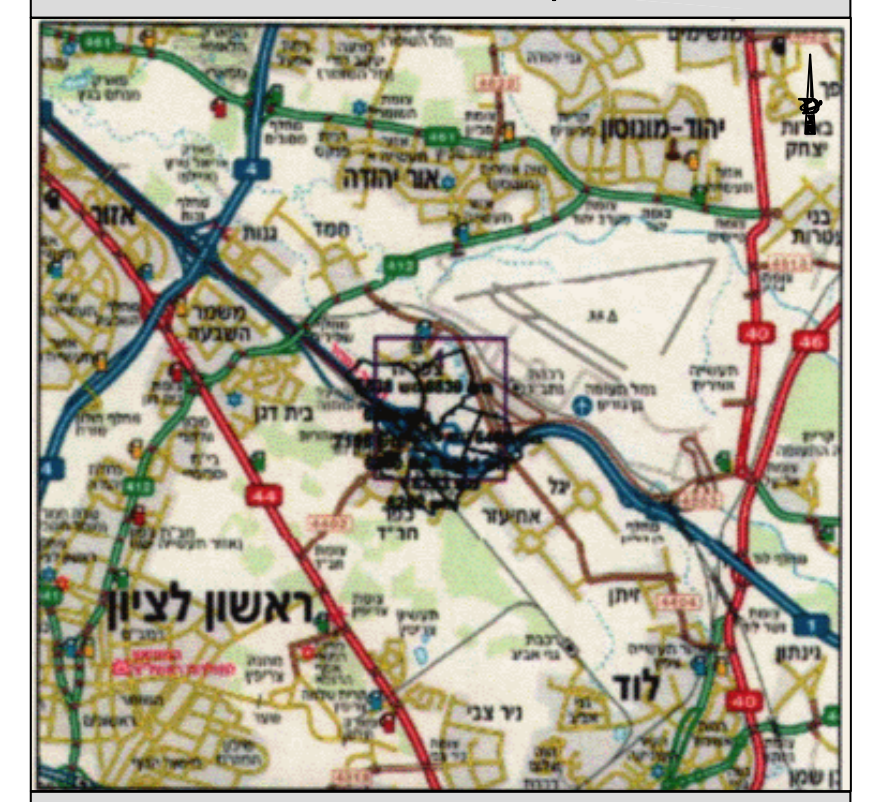

תרשים סביבה -קנ"מ 1:15000

עצי שדרה בוהיניות בצבע בין וורוד ללבן
עצים באזור הנחל כדוגמת תאנה, ערבה, תות
נטיעת עצים בתבנית פרדס כדוגמת חרוב, עצי זית
צמחיה לפי תכנית
קיר מסתור להריסה\חדש 3.50
קיר אקוסטי חדש 4.00
קיר תמך באזור נחל שפירים 1-8.00
אדמה
מילוי
קו טופוגרפיה טבעי
קו טופוגרפיה מתוכננת
גבול תוכנית

מקרא
- 🟥 קו זכות הדרך מוצע
- 🟦 גבול תוכנית
- גדר אזור אסור להתארגנות
- 🟩 טיפול נופי: צמחיה תואמת את סוג הצמחייה אשר במסגרת הקו המהיר
- תחום נחל שפירים
- ▨ פשט הצפה נחל שפירים
- ▨ שטח אסור להתארגנות
- גשר
- ▨ מעבר תת קרקעי
- רמפה לירושלים לתכנון עתידי
- דרך חקלאית/ שירות נחל
- ●● נטיעת עצים בתבנית פרדס כדוגמת חרוב, עצי זית
- ●● עצי שדרה בוהיניות בצבע בין וורוד ללבן
- קיר תמך באזור נחל משולב בקיר מסתור
- קיר אקוסטי
- קיר מסתור להעתקה
- קיר מסתור קיים
- קיר מסתור עתידי
- ● תחנת שאיבה

הריני מצהיר בזאת כי המפה הטופוגרפית\מצבית המהווה רקע לתכנית זו, נערכה על ידי ביום 22/06/2017 והיא הוכנה לפי הוראות נוהל מבא"ת ובהתאם להוראות החוק ולתקנות במודדים שבתוקף . דיוק בקו הכחול והקדסטר: מדידה גרפית

שם המודד	מספר רשיון	חתימה	תאריך
משה פלדס	442		

חתכים טיפוסיים קנ"מ 1:250

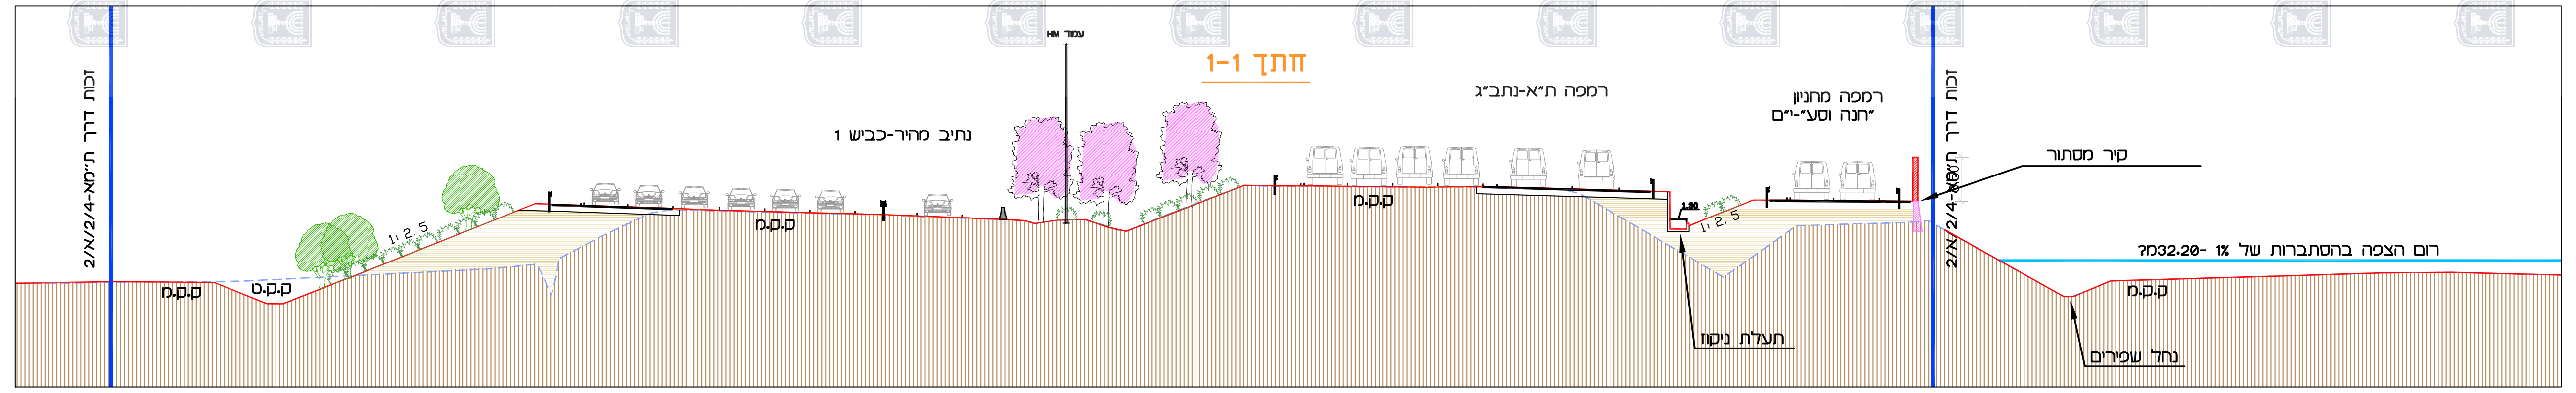
חתך 1-1
רום הצפה בהסתברות של 1% 32.20-מ'
נחל שפירים
קיר מסתור
רמפה מחניון "יהנה וסע"-ים
תעלת ניקוז
רמפה ת"א-נתב"ג
נתיב מהיר-כביש 1
ק.ק.מ
ק.ק.ט
1:2.5
זכות דרך תמ"א-4/2/א/2

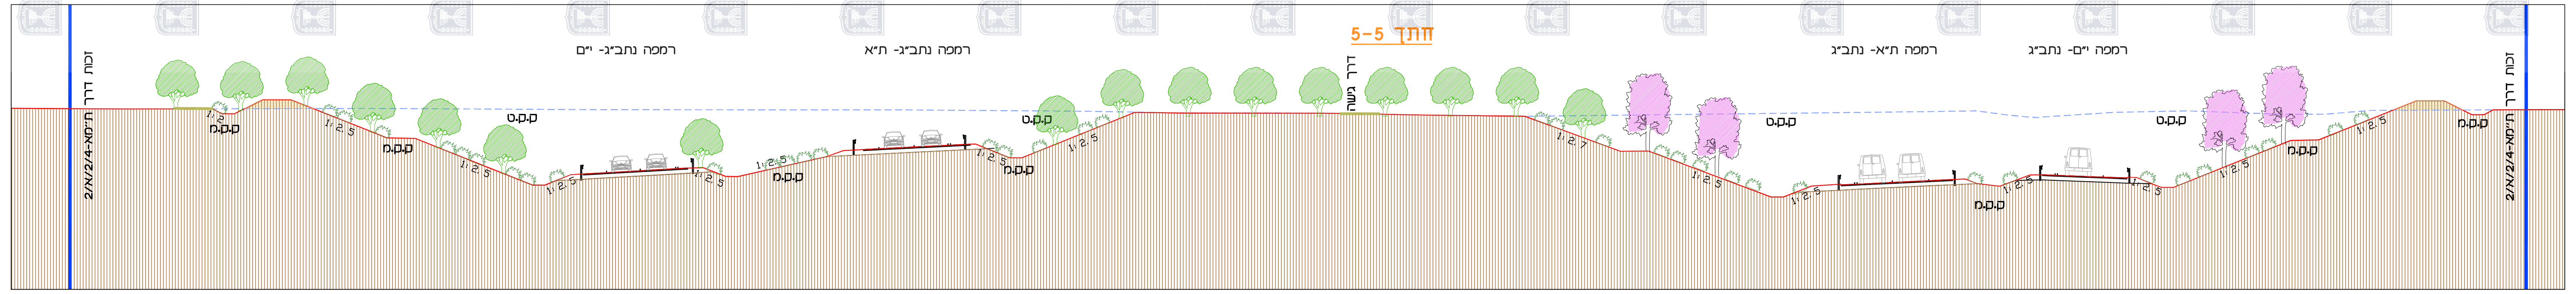
חתך 5-5
רמפה "ים- נתב"ג
רמפה ת"א- נתב"ג
רמפה נתב"ג- ת"א
רמפה נתב"ג- ים
ק.ק.מ
ק.ק.ט
1:2.5
1:2.7
זכות דרך תמ"א-4/2/א/2

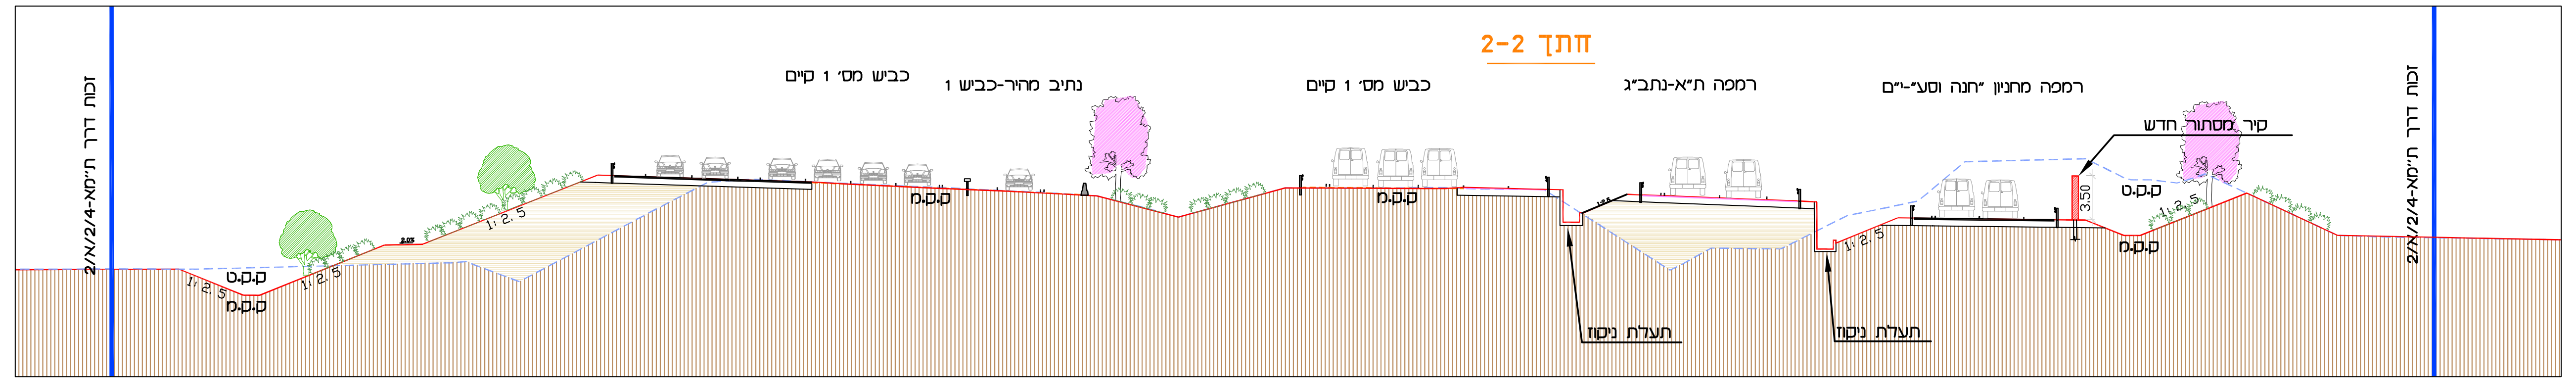
חתך 2-2
קיר מסתור חדש
3.50
רמפה מחניון "יהנה וסע"-ים
תעלת ניקוז
תעלת ניקוז
רמפה ת"א-נתב"ג
כביש מס' 1 קיים
נתיב מהיר-כביש 1
כביש מס' 1 קיים
ק.ק.מ
ק.ק.ט
1:2.5
זכות דרך תמ"א-4/2/א/2

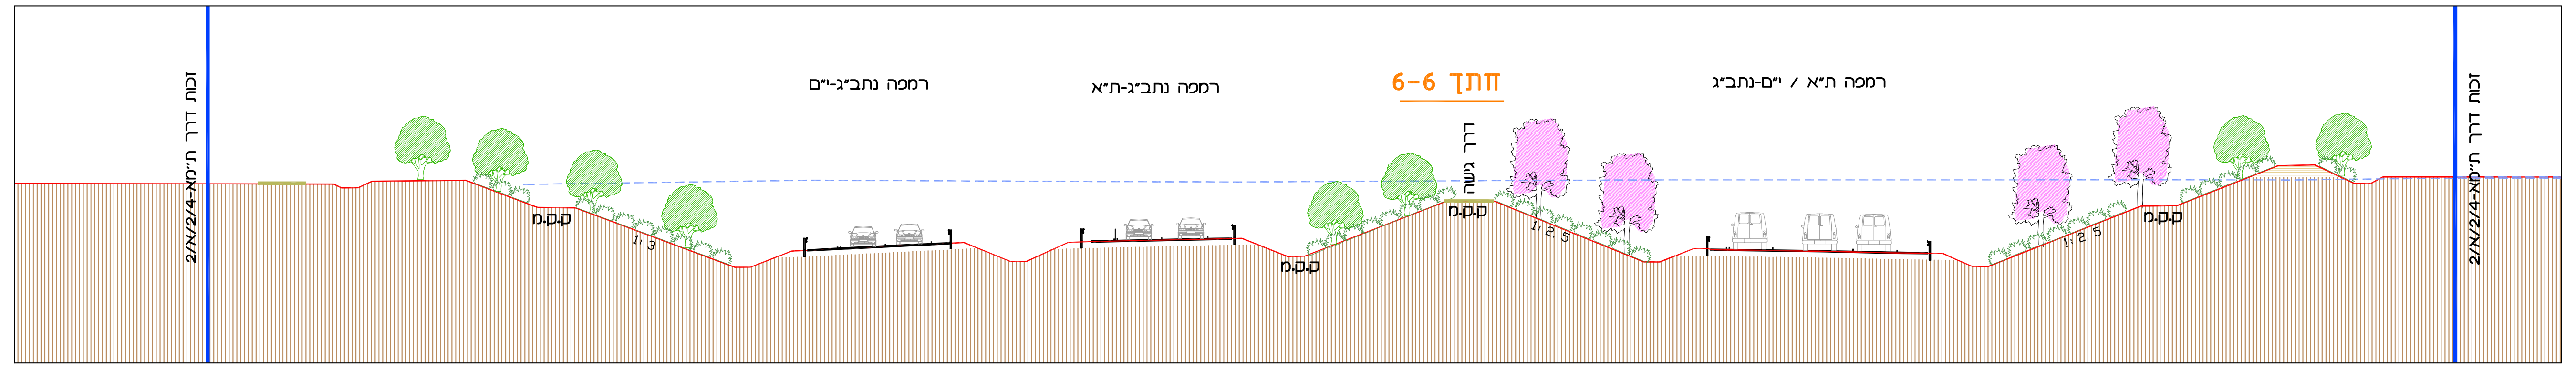
חתך 6-6
רמפה ת"א / ים-נתב"ג
רמפה נתב"ג-ת"א
רמפה נתב"ג-ים
ק.ק.מ
ק.ק.ט
1:2.5
1:3
זכות דרך תמ"א-4/2/א/2

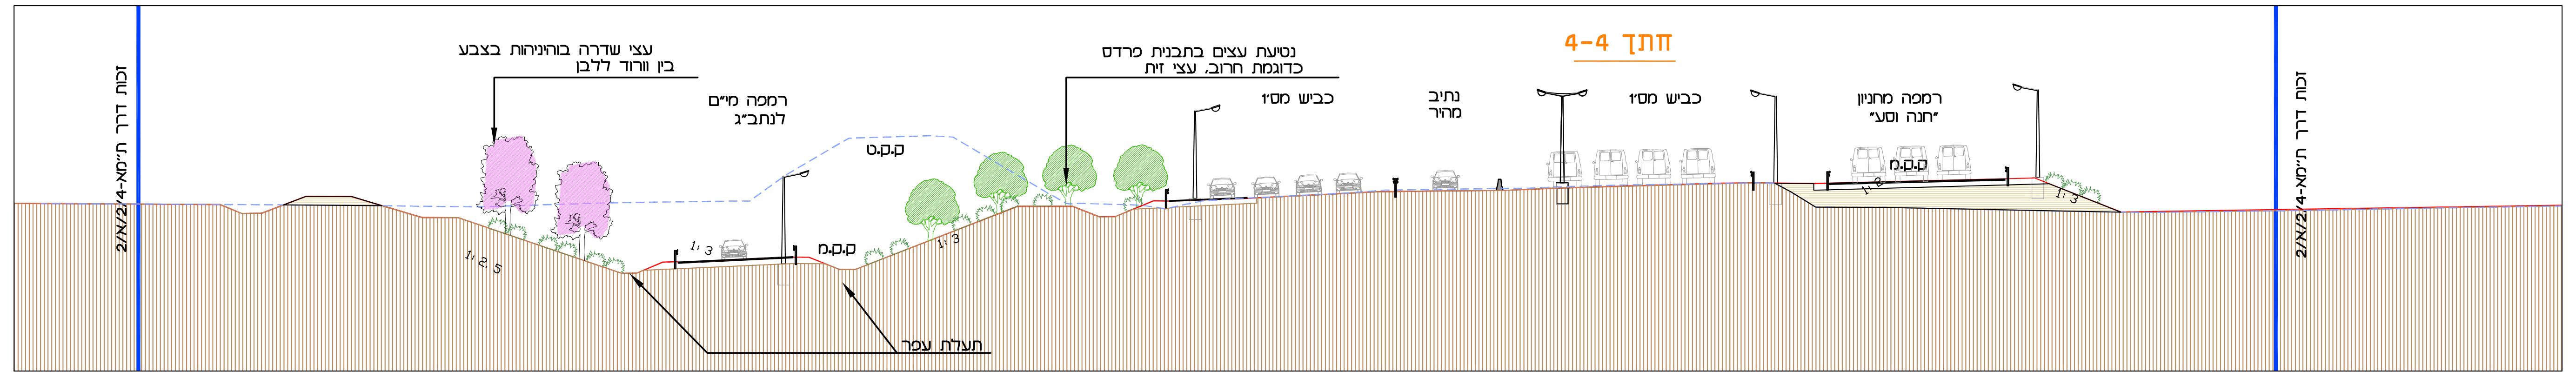
חתך 4-4
רמפה מחניון "יהנה וסע"
כביש מס'1
נתיב מהיר
כביש מס'1
נטיעת עצים בתבנית פרדס כדוגמת חרוב, עצי זית
רמפה קיים לנתב"ג
עצי שדרה בוהיניות בצבע בין וורוד ללבן
תעלת עפר
ק.ק.מ
ק.ק.ט
1:3
1:2.5
זכות דרך תמ"א-4/2/א/2

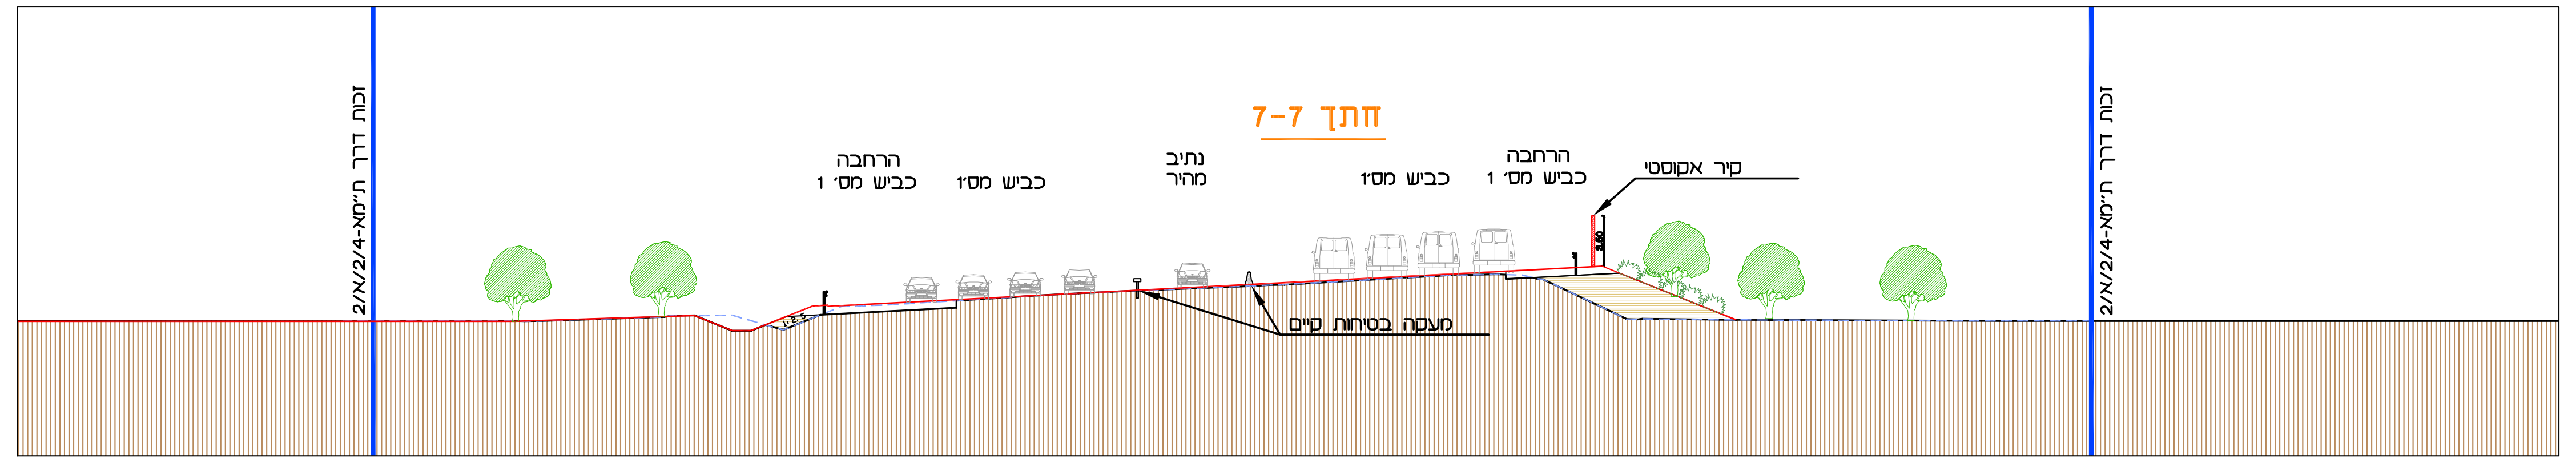
חתך 7-7
קיר אקוסטי
הרחבה כביש מס' 1
כביש מס'1
נתיב מהיר
מעקות בטיחות קיים
כביש מס'1
הרחבה כביש מס' 1
זכות דרך תמ"א-4/2/א/2

חתך 3-3
כביש מחבר כפר חב"ד-צפריה
רום הצפה בהסתברות של 1% 32.20-מ'
רמפה-נתב"ג-ים
רמפה מחניון "יהנה וסע"-ים
רמפה ת"א-נתב"ג
תעלת ניקוז
כביש מס'1
נתיב מהיר כביש 1
כביש מס' 1 קיים
רמפה נתב"ג-ת"א
רמפה נתב"ג-ים
כביש מחבר צפריה-בית רבקה
ק.ק.מ
ק.ק.ט
1:2.5
1:2.7
1:3
זכות דרך תמ"א-4/2/א/2

תכנית קנ"מ 1:2500

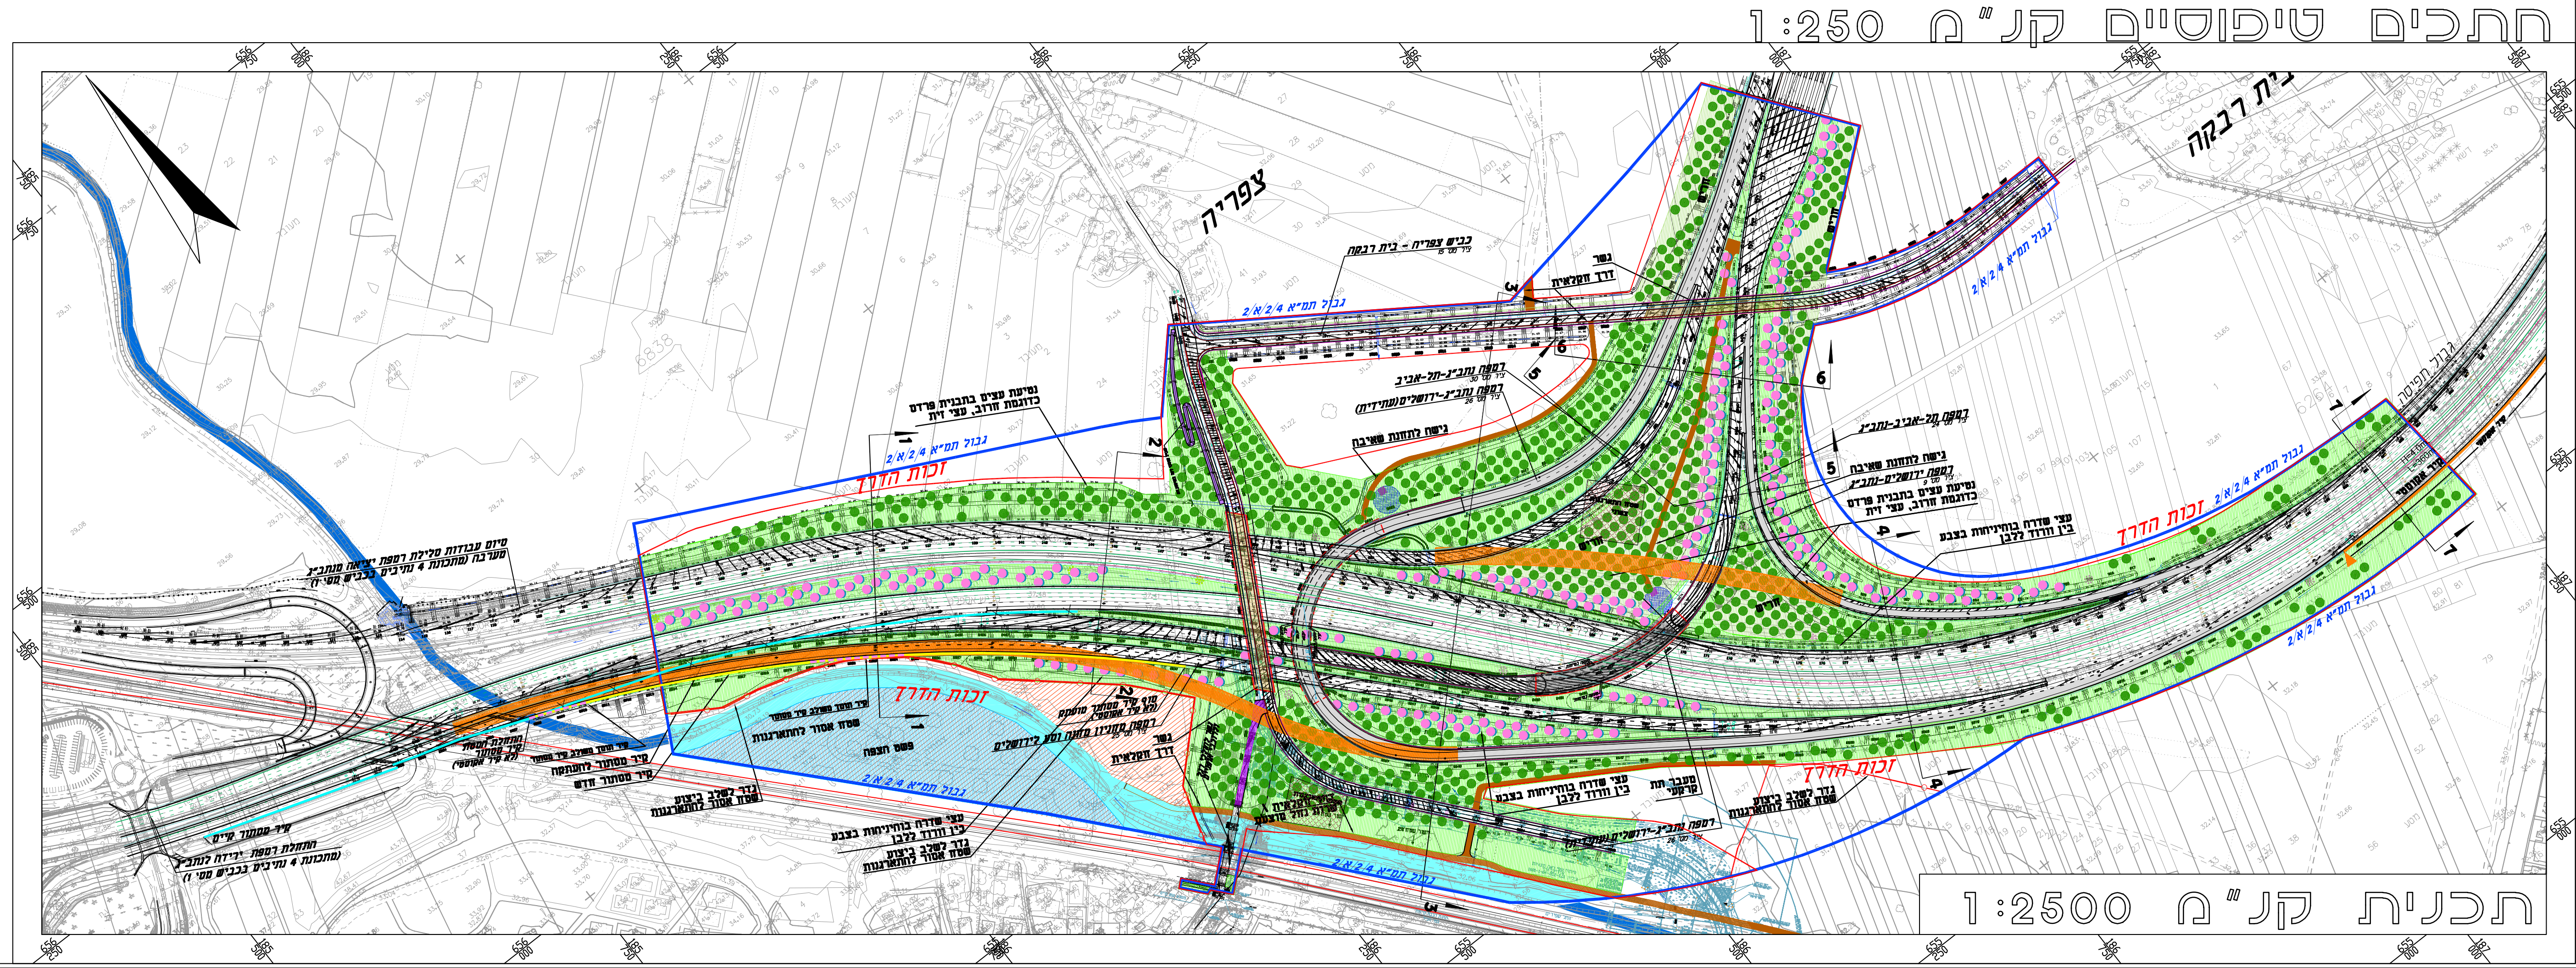
צפריה
בית רבקה
זכות הדרך
גבול תמ"א 2/א/2/4