


חוק התכנון והבנייה, התשכ"ה - 1965	
תכנית מתאר ארצית	
מס' תמא\4\2\א\2	
מחלק כניסה מערבי לנמל התעופה בן גוריון	
נספח גשרים וסביבתם כולל אדריכלות מעבר תת קרקעי ברמפה תיא נתביג UP-01	
מחזור	מרכז
מרחב תכנון מקומי	עמק לוד
רשות מקומית	מ.א. עמק לוד
ישוב	כפר חב"ד
תכנית בסמכות	ארצית
איחוד וחלוקה	ללא איחוד וחלוקה
היתרים או הרשאות	הכנת שטחיהם ניתן להוציא היתרים או הרשאות
מונה תדפיס התשרים	8
מועד הפקה	23.07.2017
שלב	תכנון
שטח התכנית	532.699 דונם
אישורים	מחזור
שמות :	אבי שרייבר
עורך ראשי	תאגיד: דגש תכנון
יוזם	חברה ממשלתית תאגיד: נתיבי ישראל בע"מ


בעלי ענין בקרקע מדינת ישראל ואזורים

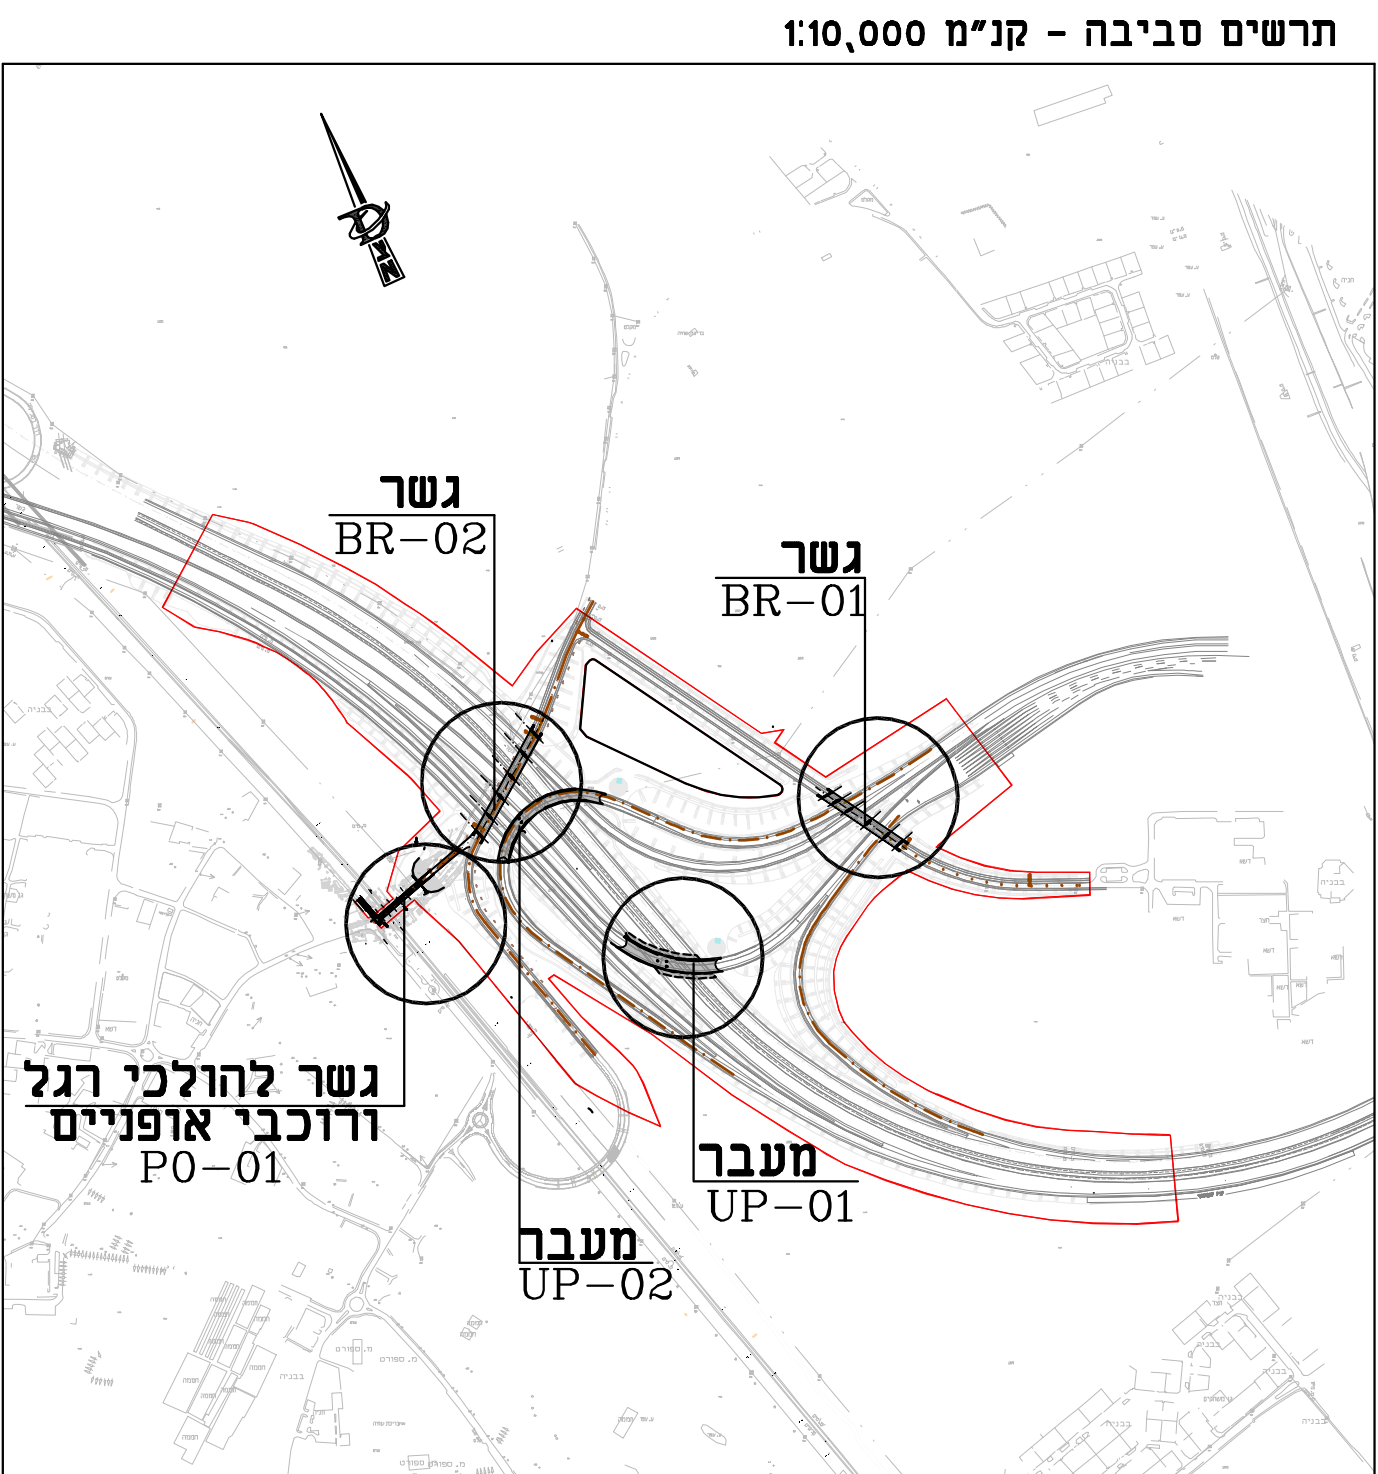


חריג מציור בזאת כי המפה הסופגית/מטבית המחוזה רקע לתכנית זו, נערכה על ידי ביום 22/06/2017 וחיא חוכנה לפי חוראות נוחל מבאית ובחחאט לחראות חוזק ולתקנות במודדים שבתוקף. דיוק בקו החזול והקדסטר: מזירות גרפית

שטח המודד: 442 מספר רשיון: חותמת: תאריך:


פורטל מזרחי

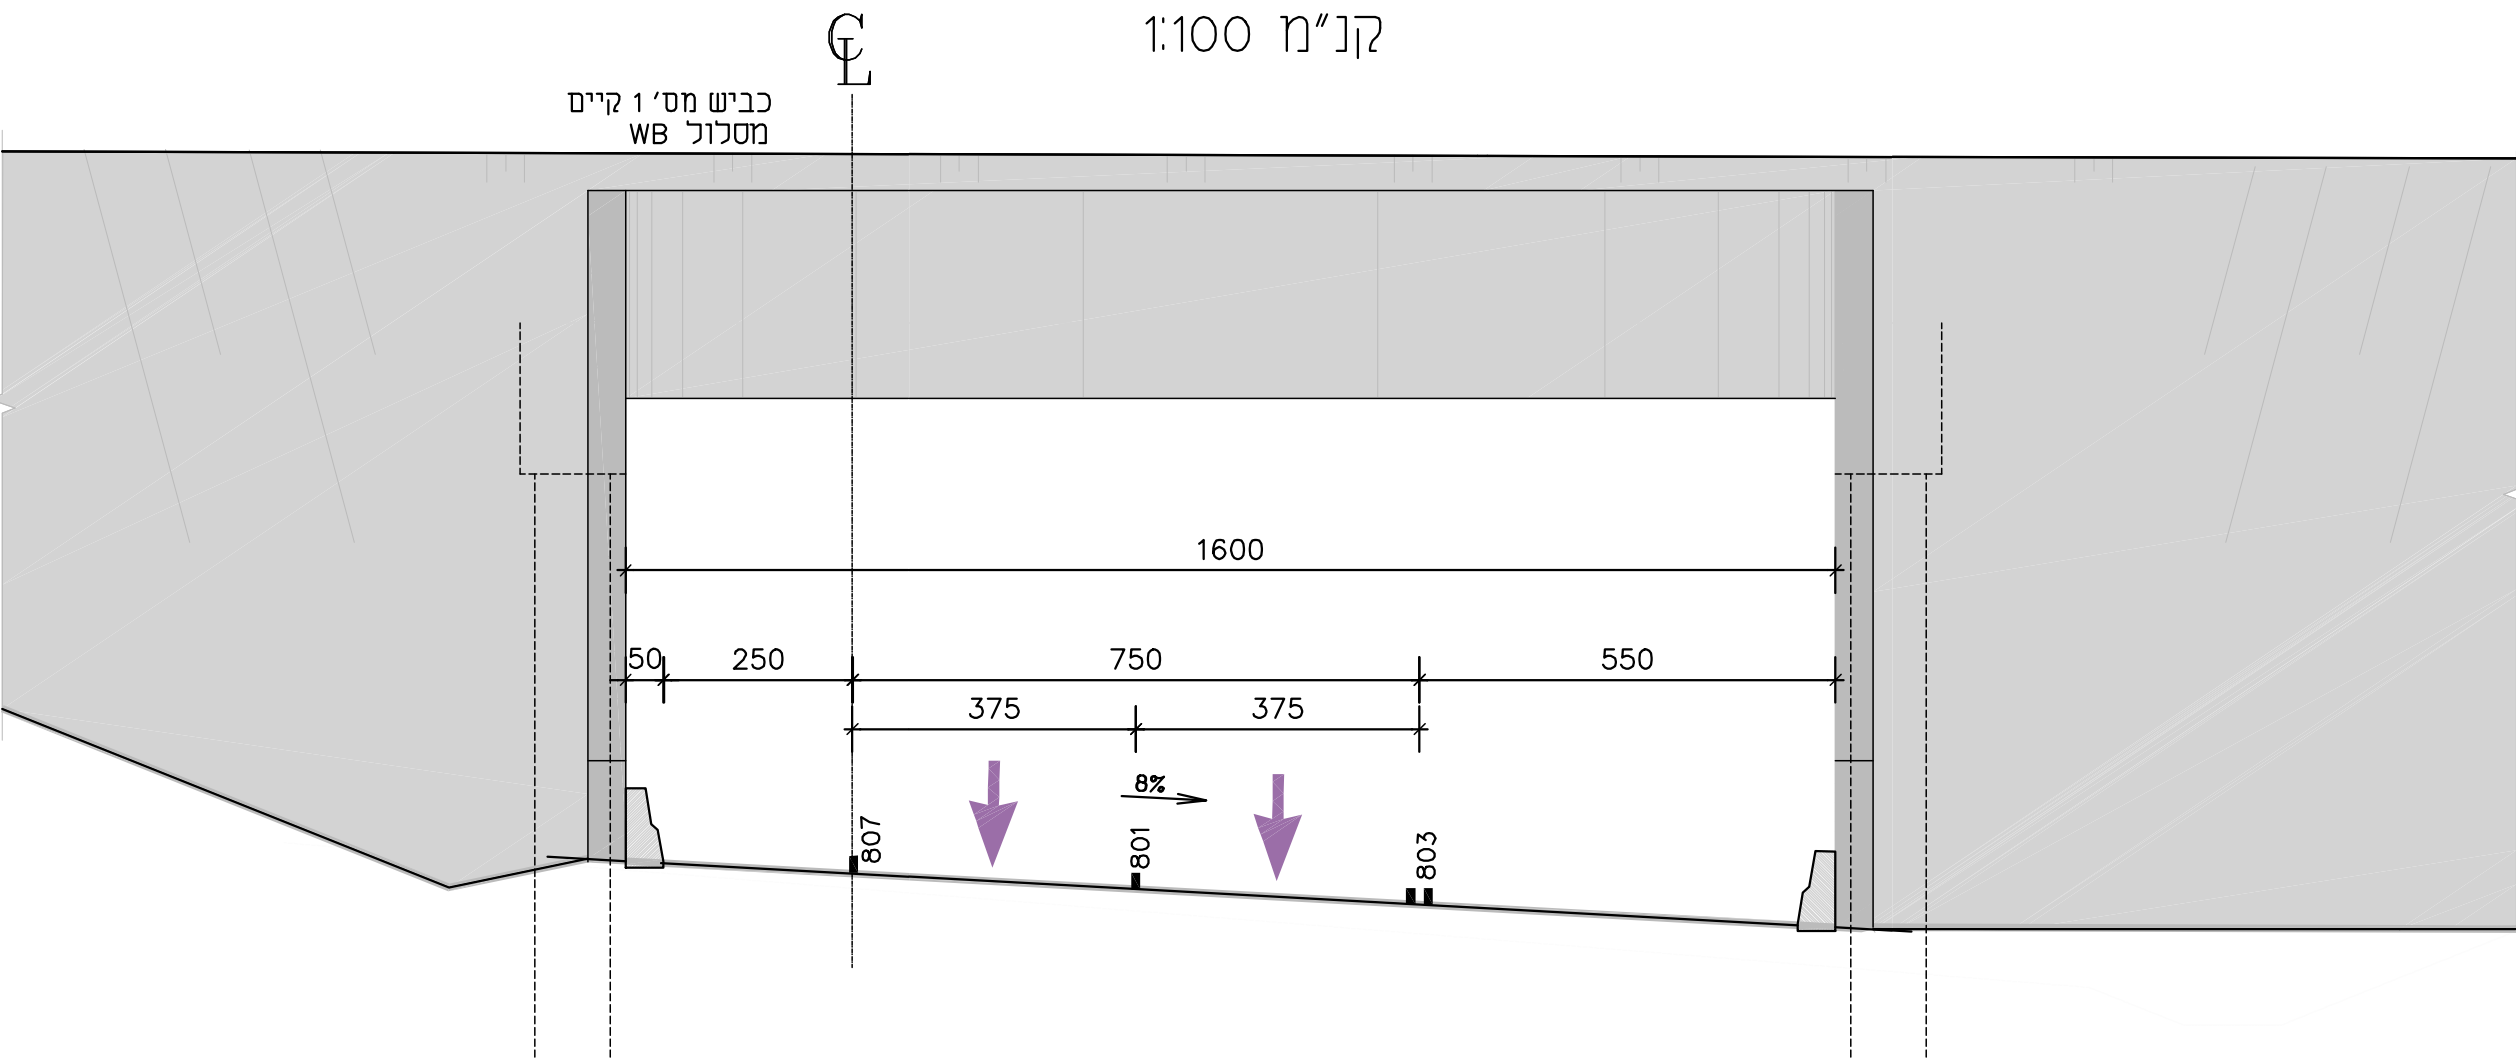

רמפה מתיא -נתביג

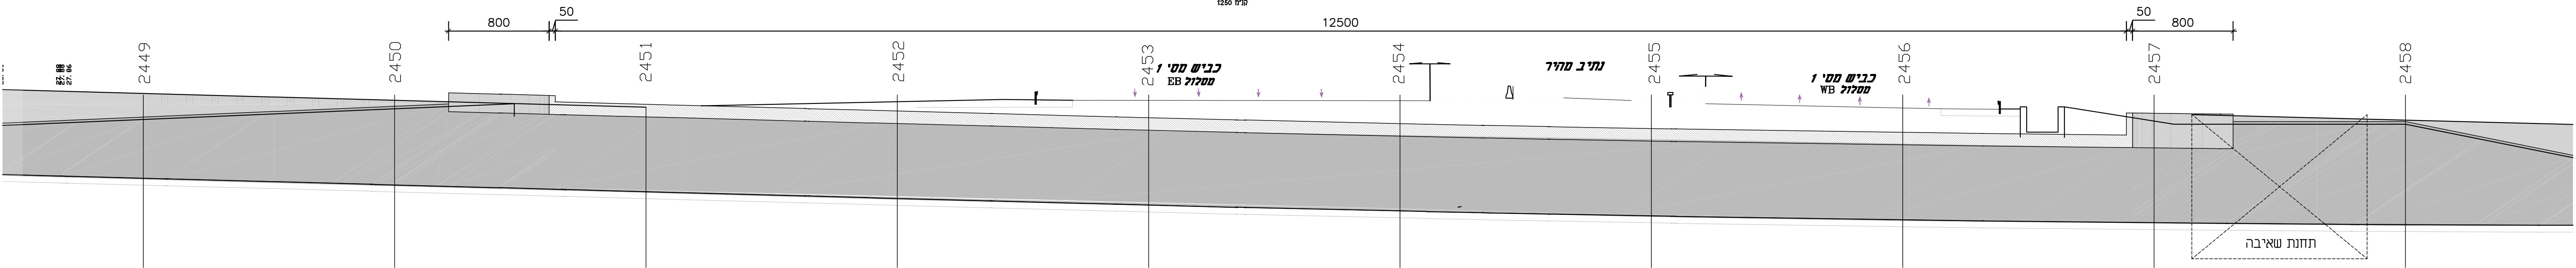


תנוחה

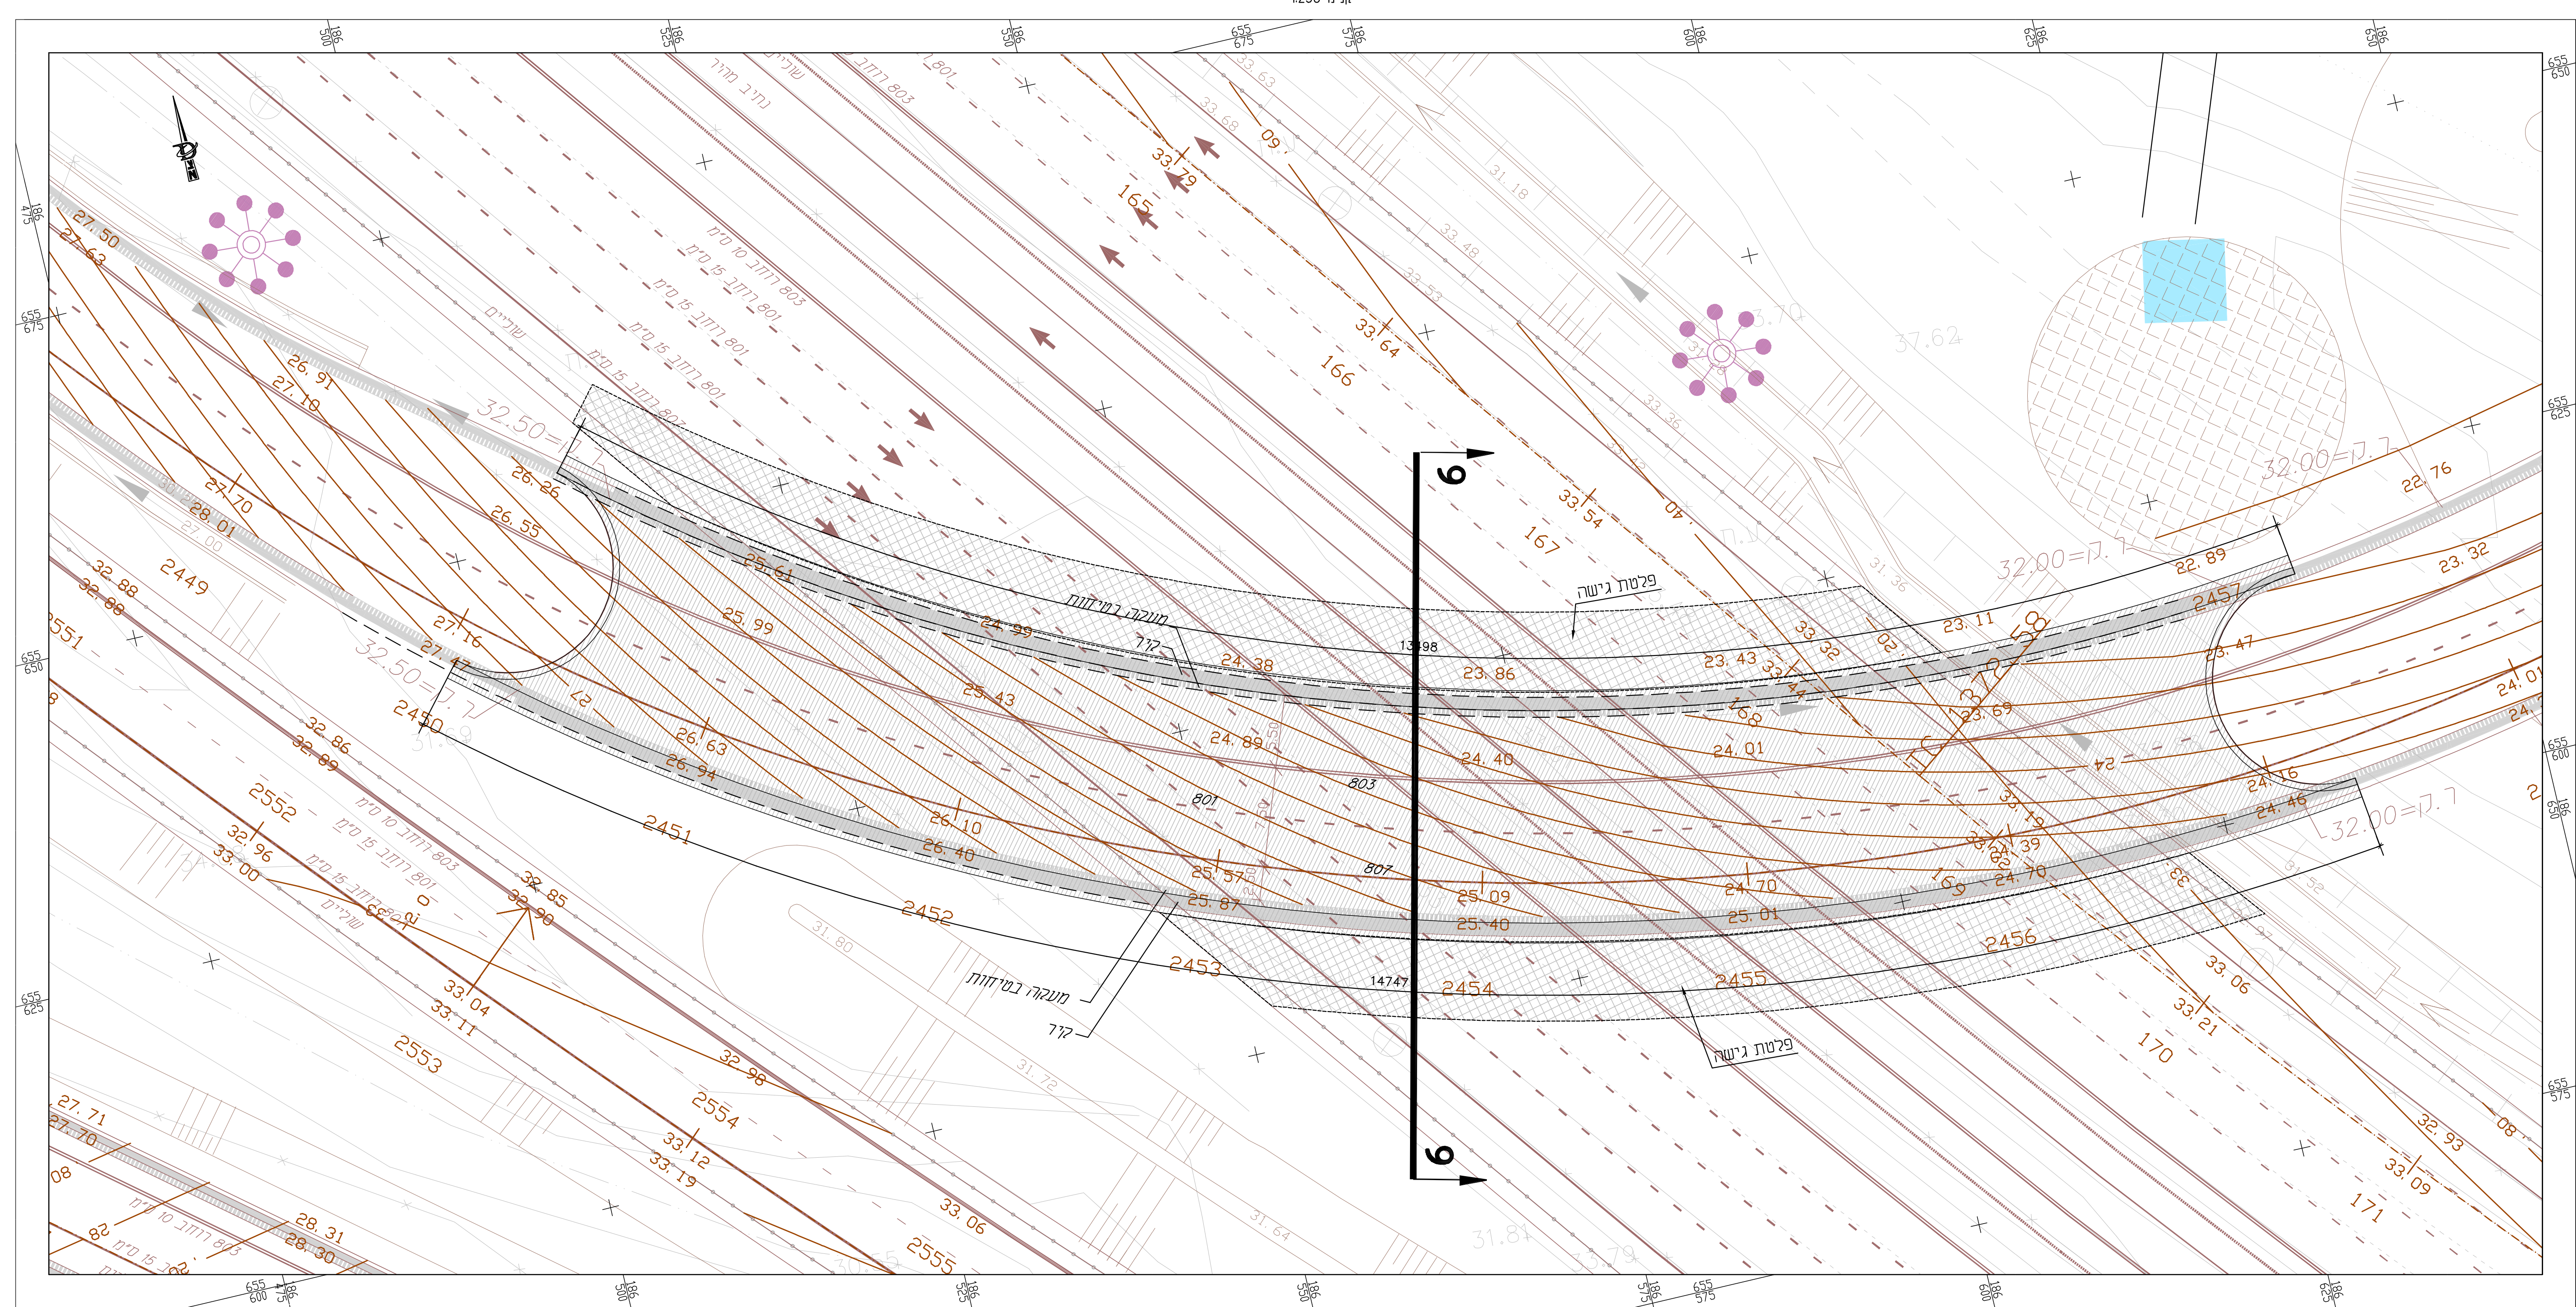

רמפה תיא נתביג-UP-01

חתך 9-9

קנה"מ 1:100

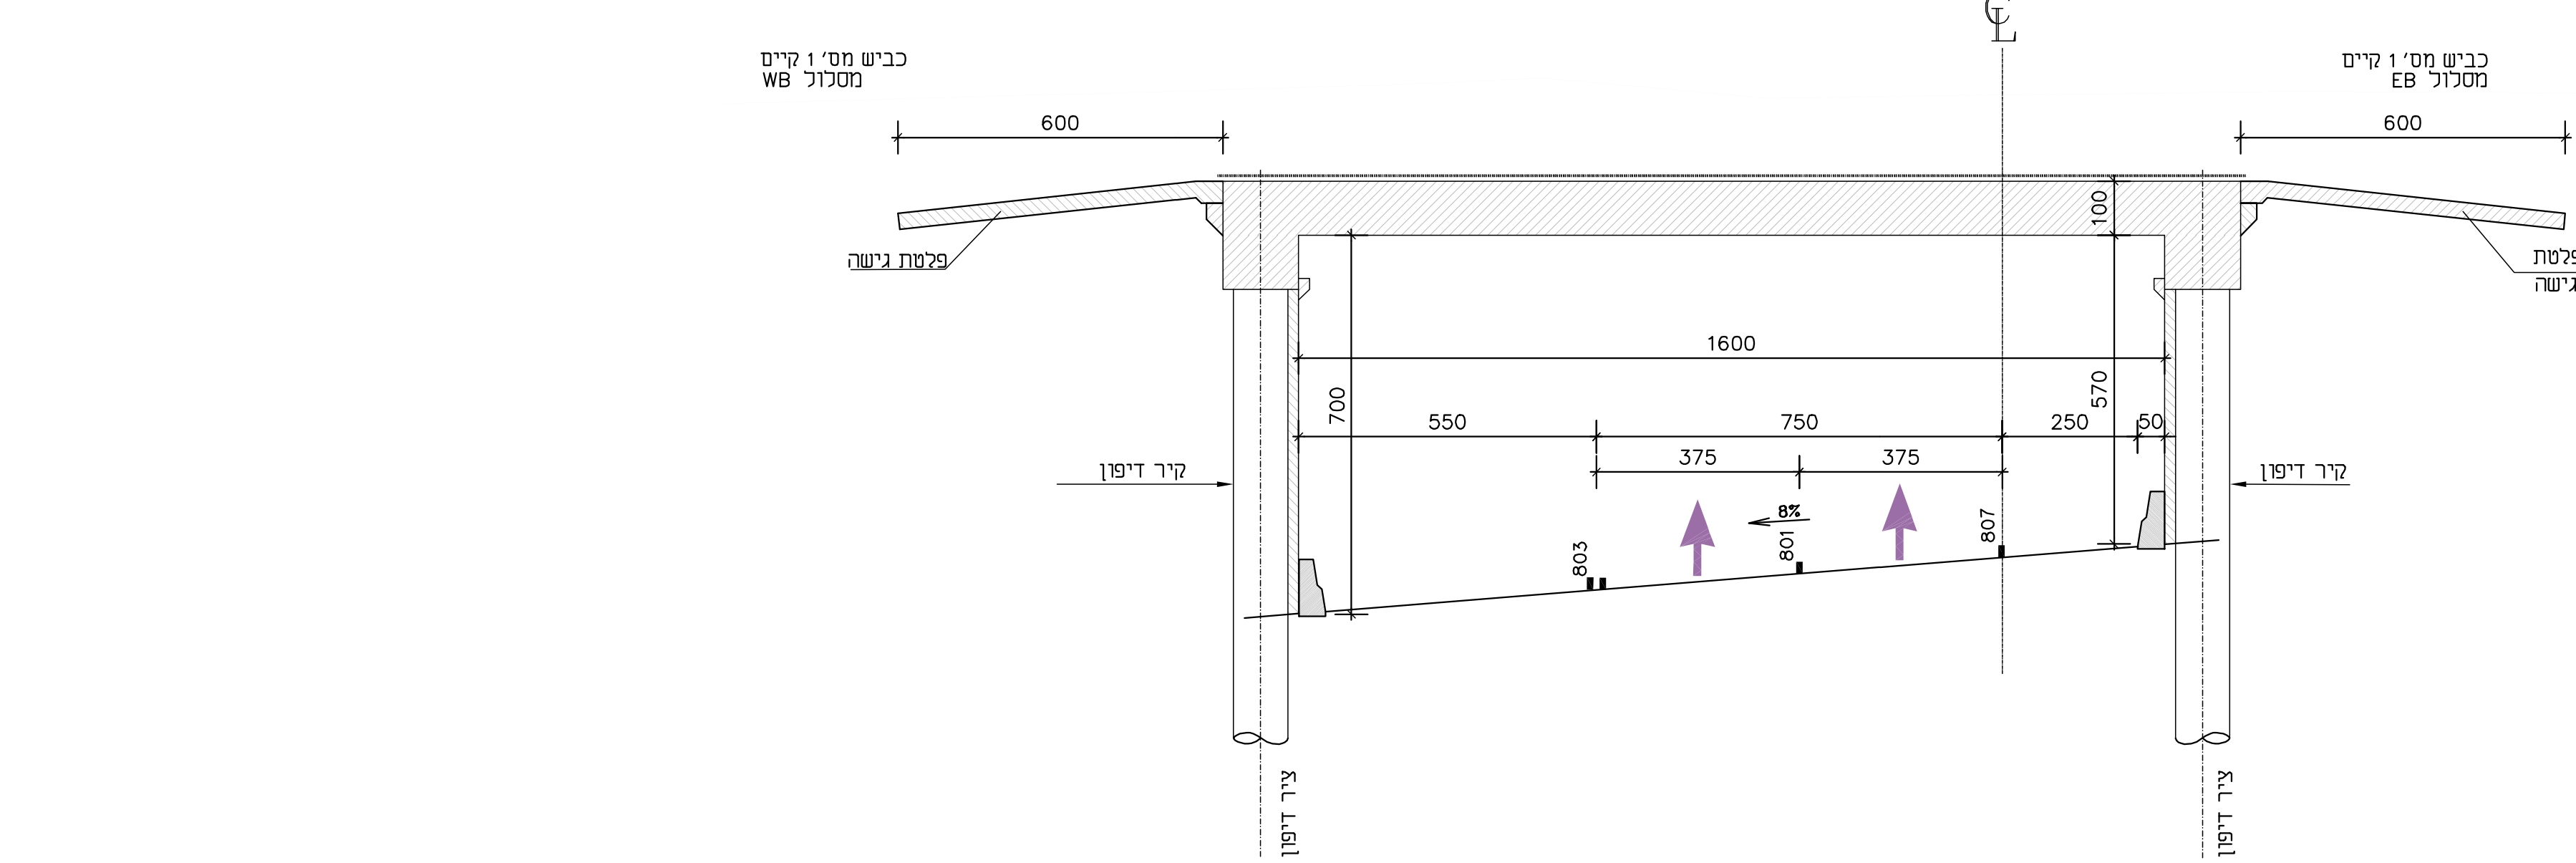

פורטל מערבי

