תיאור זרימת מים בתעלת איילון

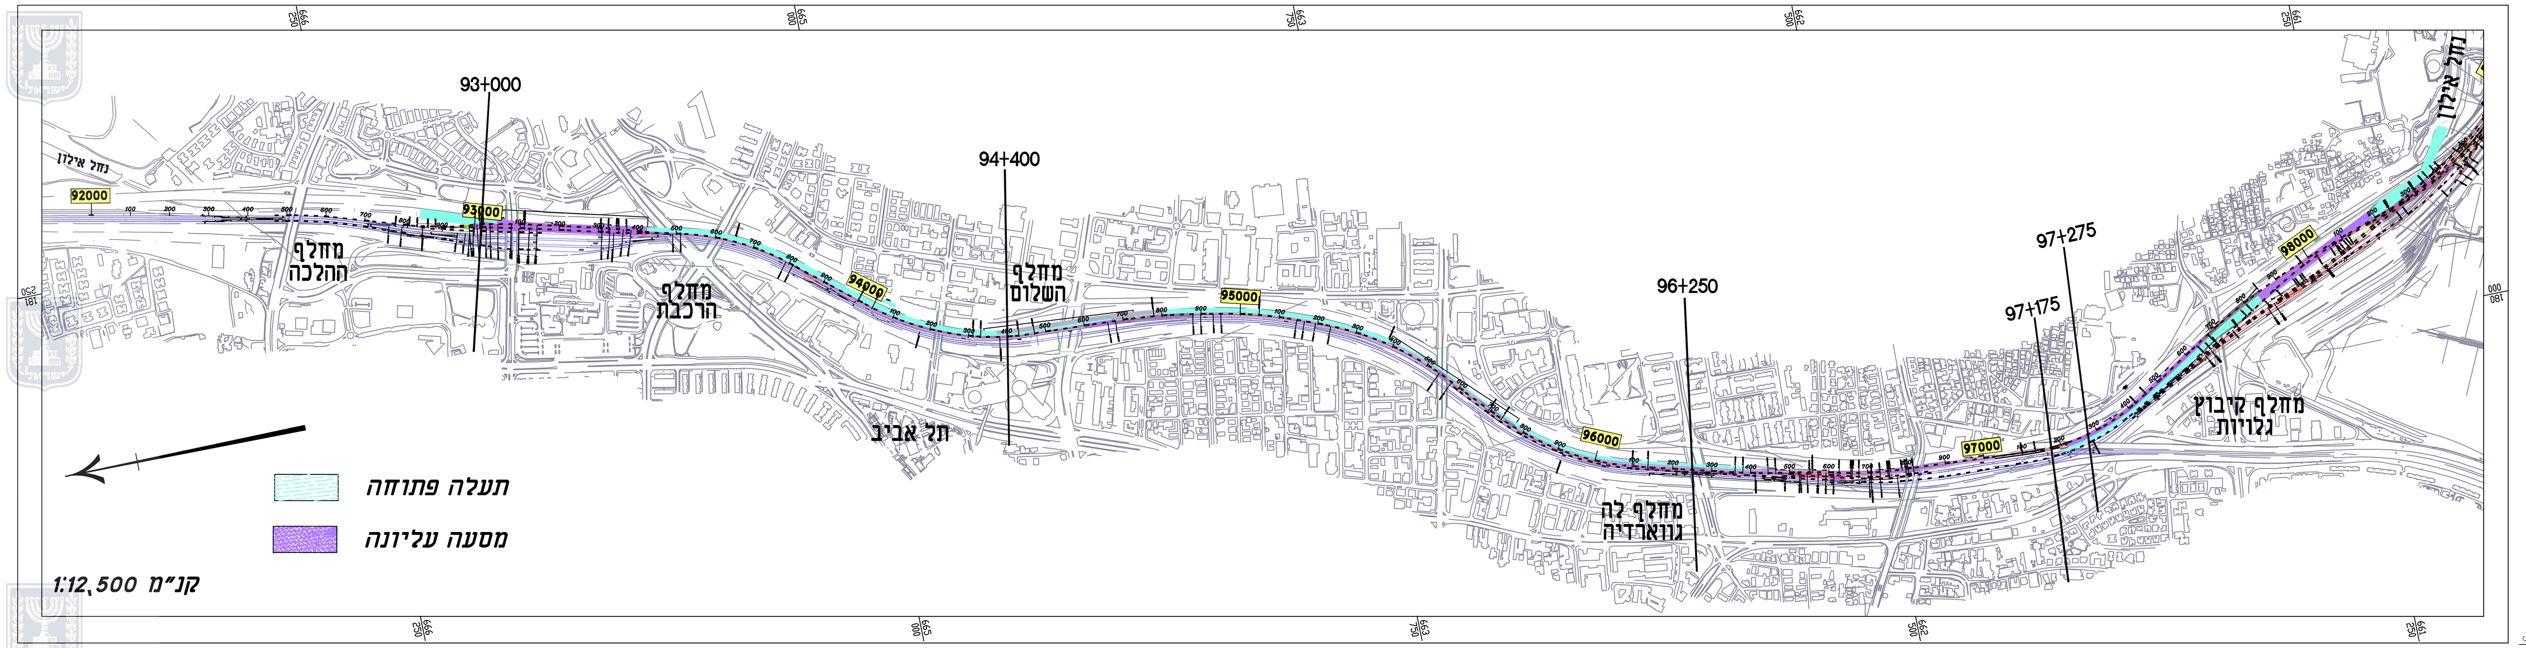

הערה: הרומים והמידות מסומנים באופן סכמטי בלבד ויקבעו בשלב התכנון המפורט

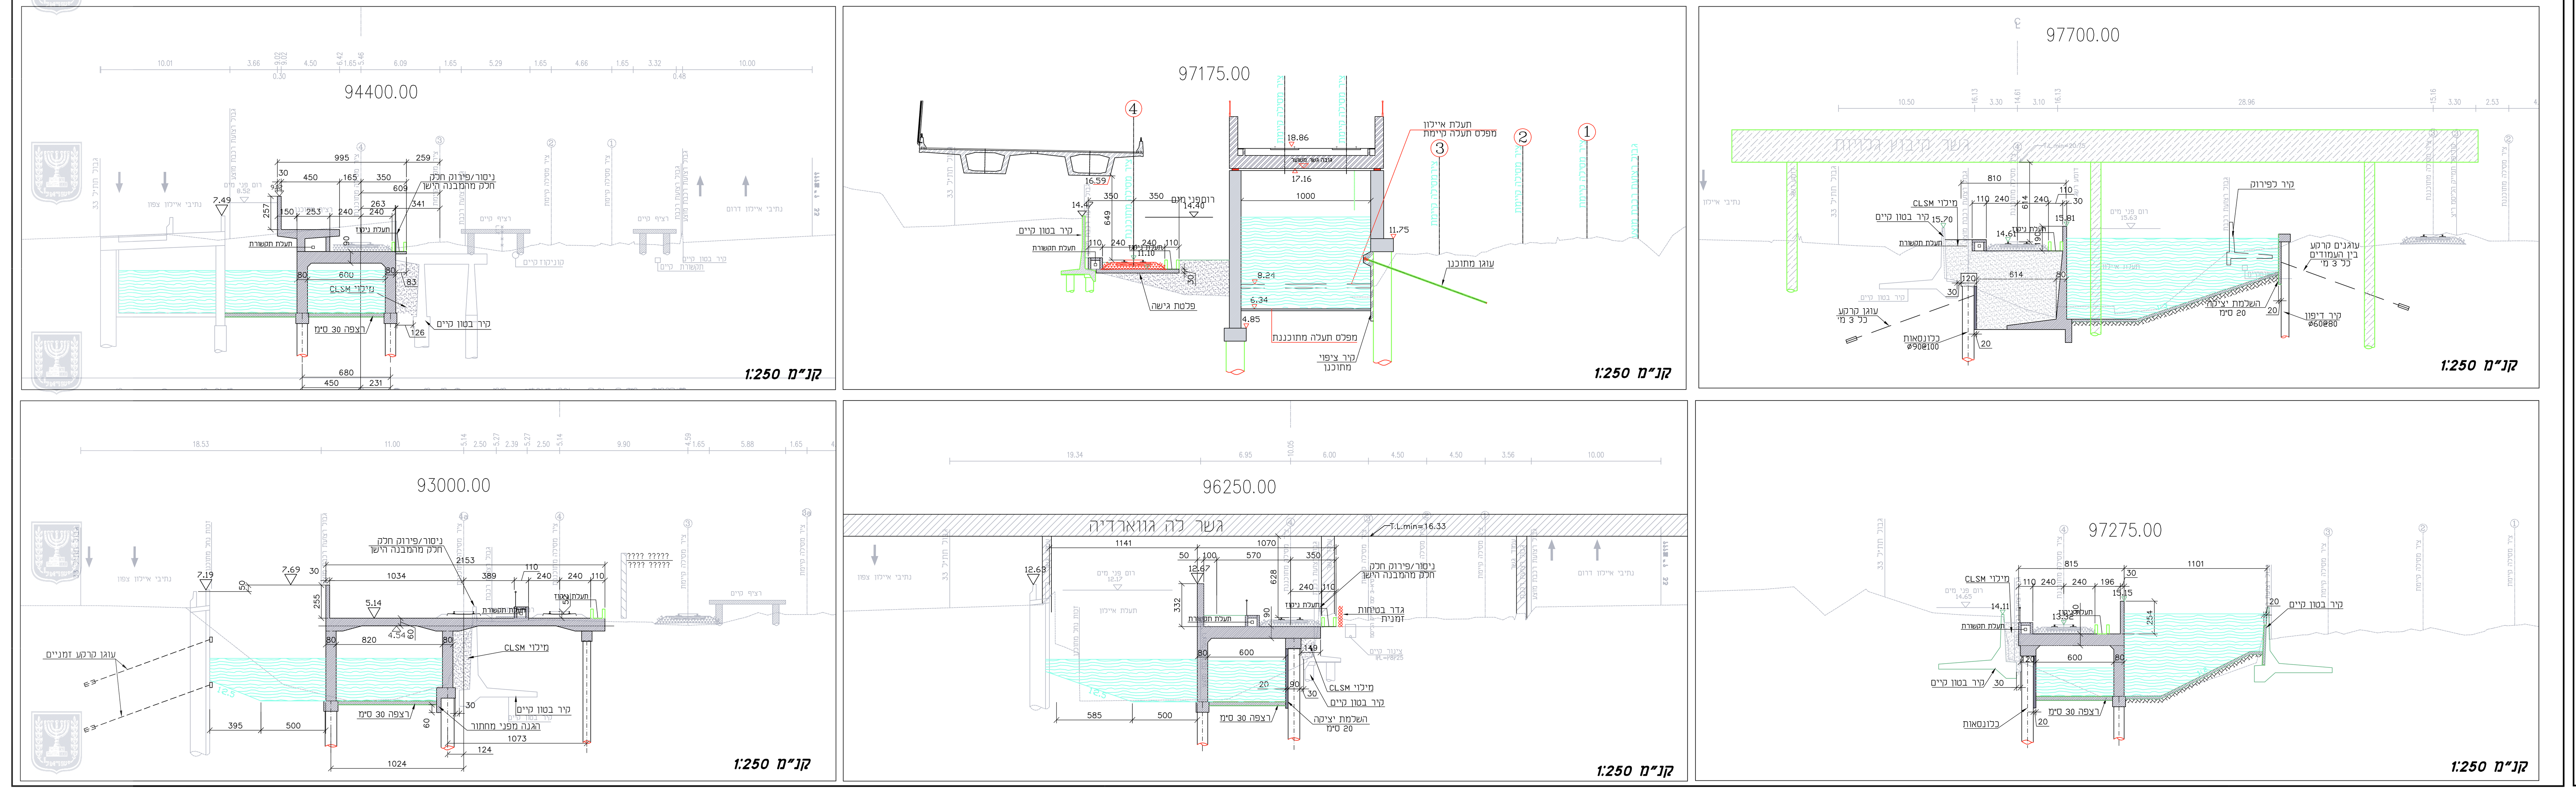

טבלת ריכוז נתוני ספיקה – רום מים – מהירות זרימה
עבור חתכים נבחרים בתעלת האיילון

Location	River Sta	ספיקה	רום קרקעית האיילון	רום פני המים	עומק המים	מהירות הזרימה
חיל השריון\ קיבוץ גלויות	97100	50	5.51	7.37	1.86	2.47
	97100	100	5.51	8.51	3	3.06
	97100	150	5.51	9.52	4.01	3.44
	97100	170	5.51	10.10	4.59	3.43
	97100	200	5.51	10.88	5.37	3.42
	97100	250	5.51	14.33	8.82	2.61
גשר ההגנה	96800	50	4.82	6.81	1.99	2.19
	96800	100	4.82	8.01	3.19	2.73
	96800	150	4.82	9.02	4.2	3.1
	96800	200	4.82	9.94	5.12	3.39
	96800	250	4.82	12.17	7.35	3.96
יצחק שדה	95500	50	2.17	5.15	2.98	0.97
	95500	100	2.17	5.88	3.71	1.56
	95500	150	2.17	6.94	4.77	1.88
	95500	200	2.17	8.08	5.91	2.25
	95500	250	2.17	9.46	7.29	2.49
תחנת השלום	94500	50	-0.09	5	5.09	0.54
	94500	100	-0.09	5.43	5.52	1.06
	94500	150	-0.09	6.08	6.17	1.59
	94500	200	-0.09	6.9	6.99	2.11
	94500	250	-0.09	8.05	8.14	2.58
גשר מוזס	94200	50	-0.29	4.98	5.27	0.55
	94200	100	-0.29	5.37	5.66	1.05
	94200	150	-0.29	5.97	6.26	1.46
	94200	200	-0.29	6.75	7.04	1.79
	94200	250	-0.29	7.88	8.17	2.02
סבידור	93400	50	-0.86	4.91	5.77	0.83
	93400	100	-0.86	5.08	5.94	1.66
	93400	150	-0.86	5.38	6.24	2.49
	93400	200	-0.86	5.8	6.66	3.33
	93400	250	-0.86	6.66	7.52	3.49

- בתכלת מסומנים מפלסי הזרימה בספיקת התכן
- באדום בהיר ספיקות גולשות מהאפיק

ספיקות צוורי הבקבוק ייבדקו בעת התכנון המפורט ויתואמו מול רשות הניקוז

הידרומודול

פתרון עקרוני לשיפור זרימת מי נגר באזור ההגנה-חיל השריון

מקרא:

- מסילה קיימת
- מסילה מתוכננת
- מבנה מתוכנן בתעלת אילון
- מבנה קיים בתעלת אילון
- גשר קיים מעל רצועת הרכבת
- תחום זרמה בתעלת אילון
- תעלה פתוחה
- כלונס קיים
- כלונס מתוכנן

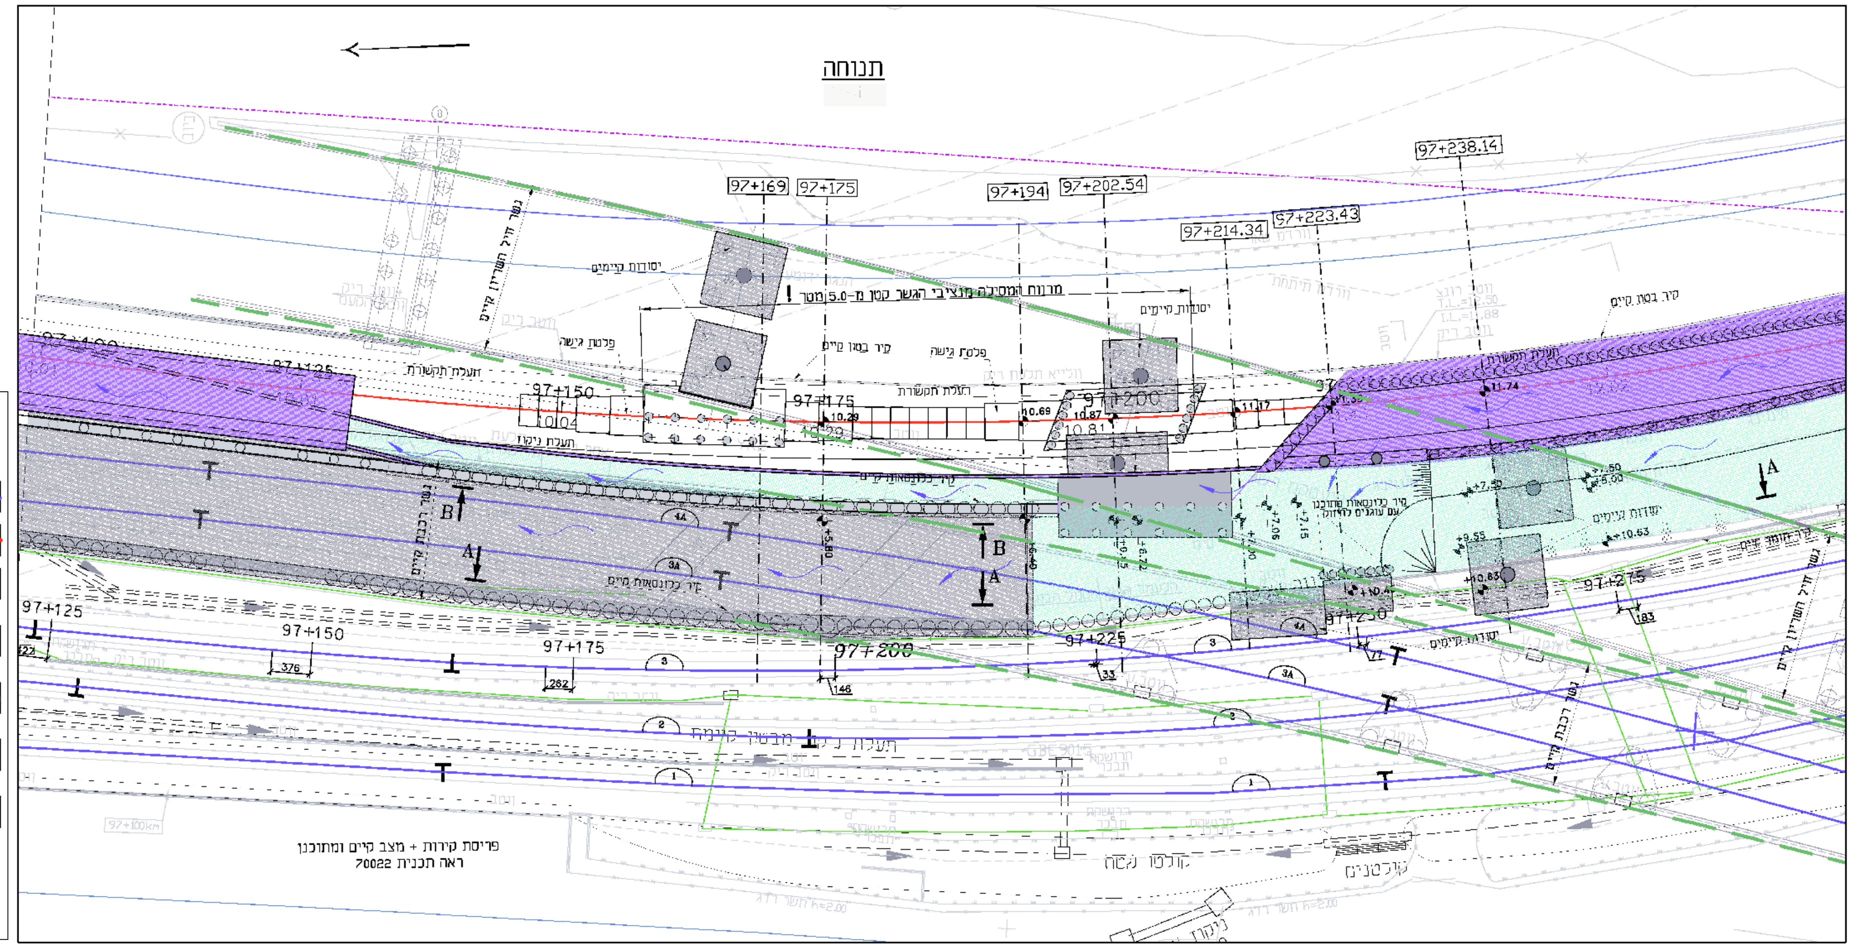

הערה:
תכנית זאת הינה עקרונית בלבד.
יש לעדכן התוויית מסילה במעבר
מתחת לגשר וויל השריון

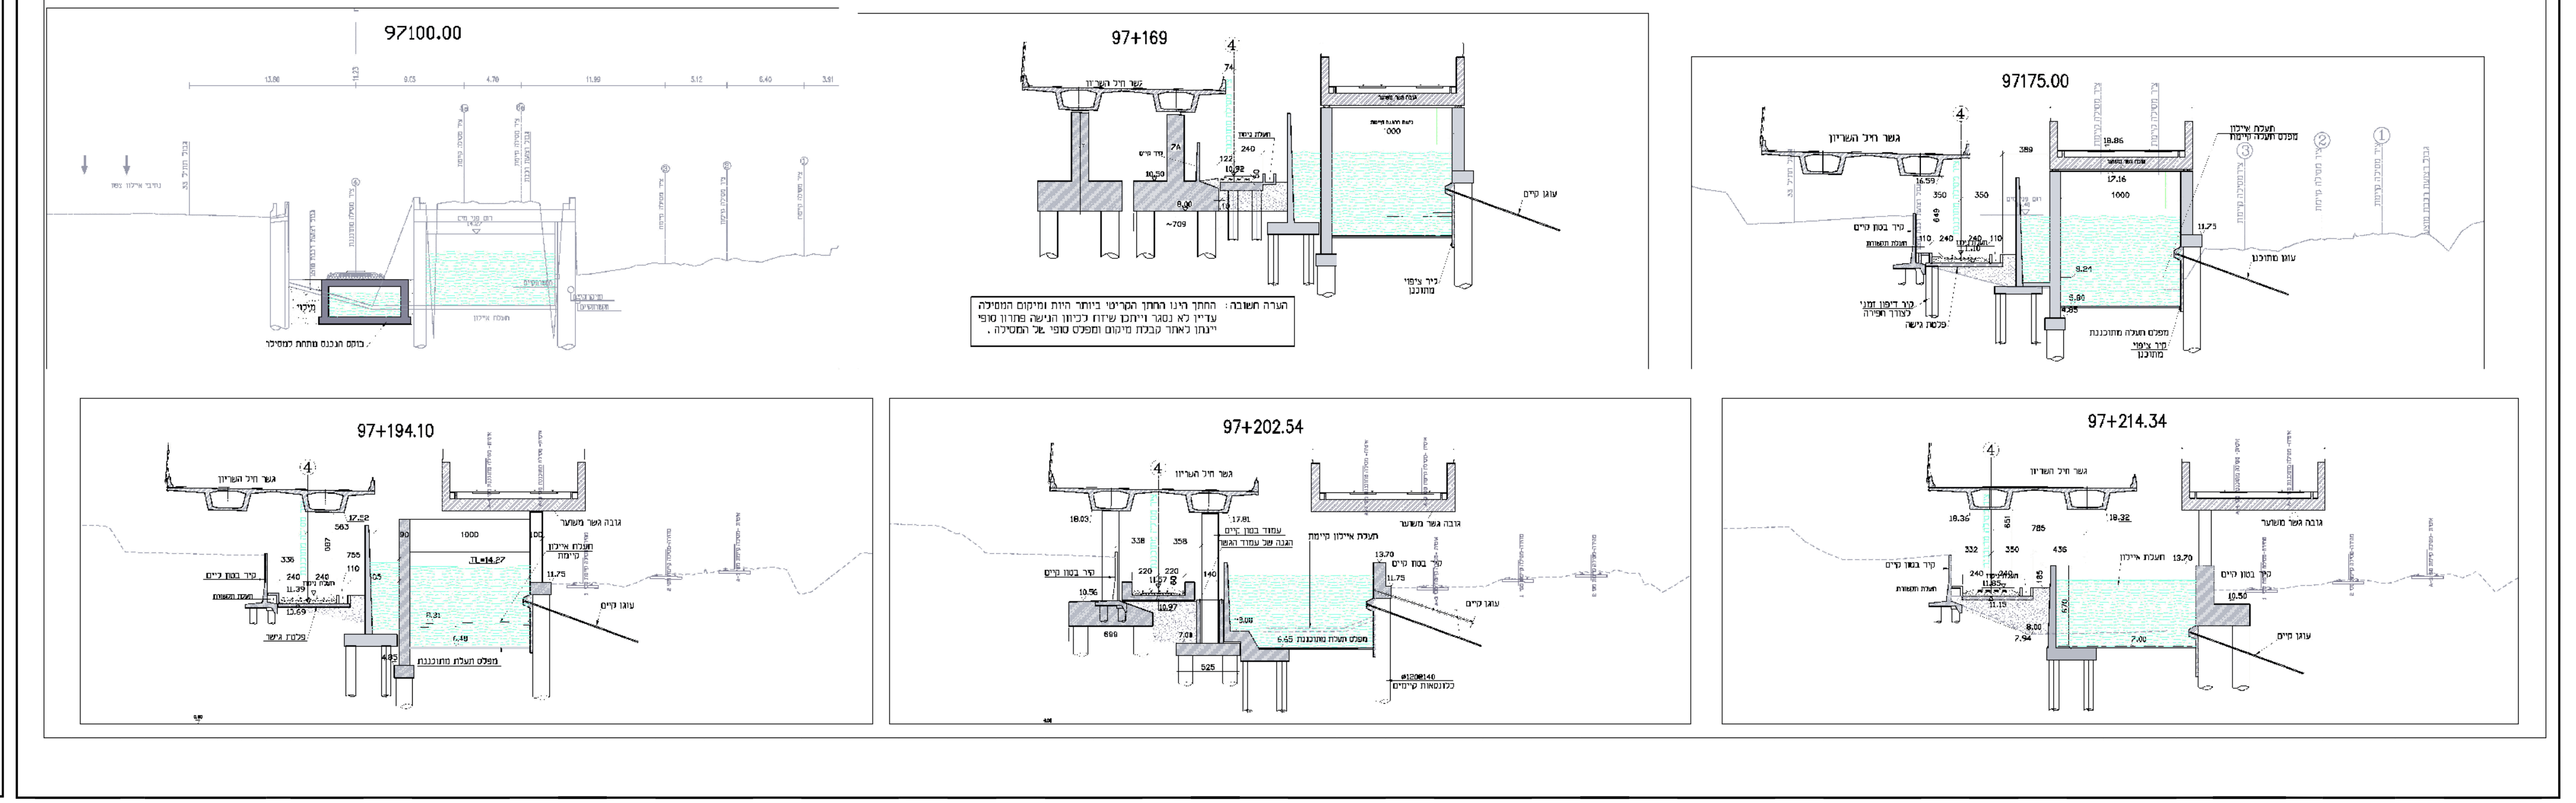

חוק התכנון והבנייה, התשכ"ה-1965
הועדה הארצית לתכנון ולבניה של תשתיות לאומיות

תת"ל 33

מסילה רביעית באיילון
קטע ת"א מרכז-לוד

תכנית לתשתית לאומית

נספח ניקוז - תעלת איילון

גליון מס' 1 מתוך 1

מחוז: תל אביב,מרכז
מרחבי תכנון מקומיים:

- ועדה מקומית תל אביב-יפו
- ועדה מקומית רמת גן
- ועדה מקומית גבעתיים
- מרחב תכנון מחוזי-מקומי (מחוז ת"א)
- ועדה מרחבית אור יהודה-אזור
- ועדה מרחבית מצפה אפק
- ועדה מקומית עמק לוד
- ועדה מקומית לוד

חותמת מוסד התכנון :

26.04.2016