

חוק התכנון והבנייה, התשכ"ה-1965
הועדה הארצית לתכנון ולבניה של תשתיות לאומיות

תת"ל 33

מסילה רביעית באילון
קטע ת"א מרכז-לוד


תכנית לתשתית לאומית

נספח תנועה-כביש מס'1


גליון מס' 1 מתוך 2
קני"מ : 2,500

- מחזור: תל אביב, מרכז
מרחבי תכנון מקומיים:
• ועדה מקומית תל אביב-יפו
• ועדה מקומית רמת גן
• ועדה מקומית גבעתיים
• מרחב תכנון מזרח-מקומי (מחזור ת"א)
• ועדה מרחבית אור יהודה-אזור
• ועדה מרחבית מצפה אפק
• ועדה מקומית עמק לוד
• ועדה מקומית לוד


חותמת מוסד התכנון :

 


שלב: אישור תכנית מהדורה: 16 תאריך: 25.04.2018

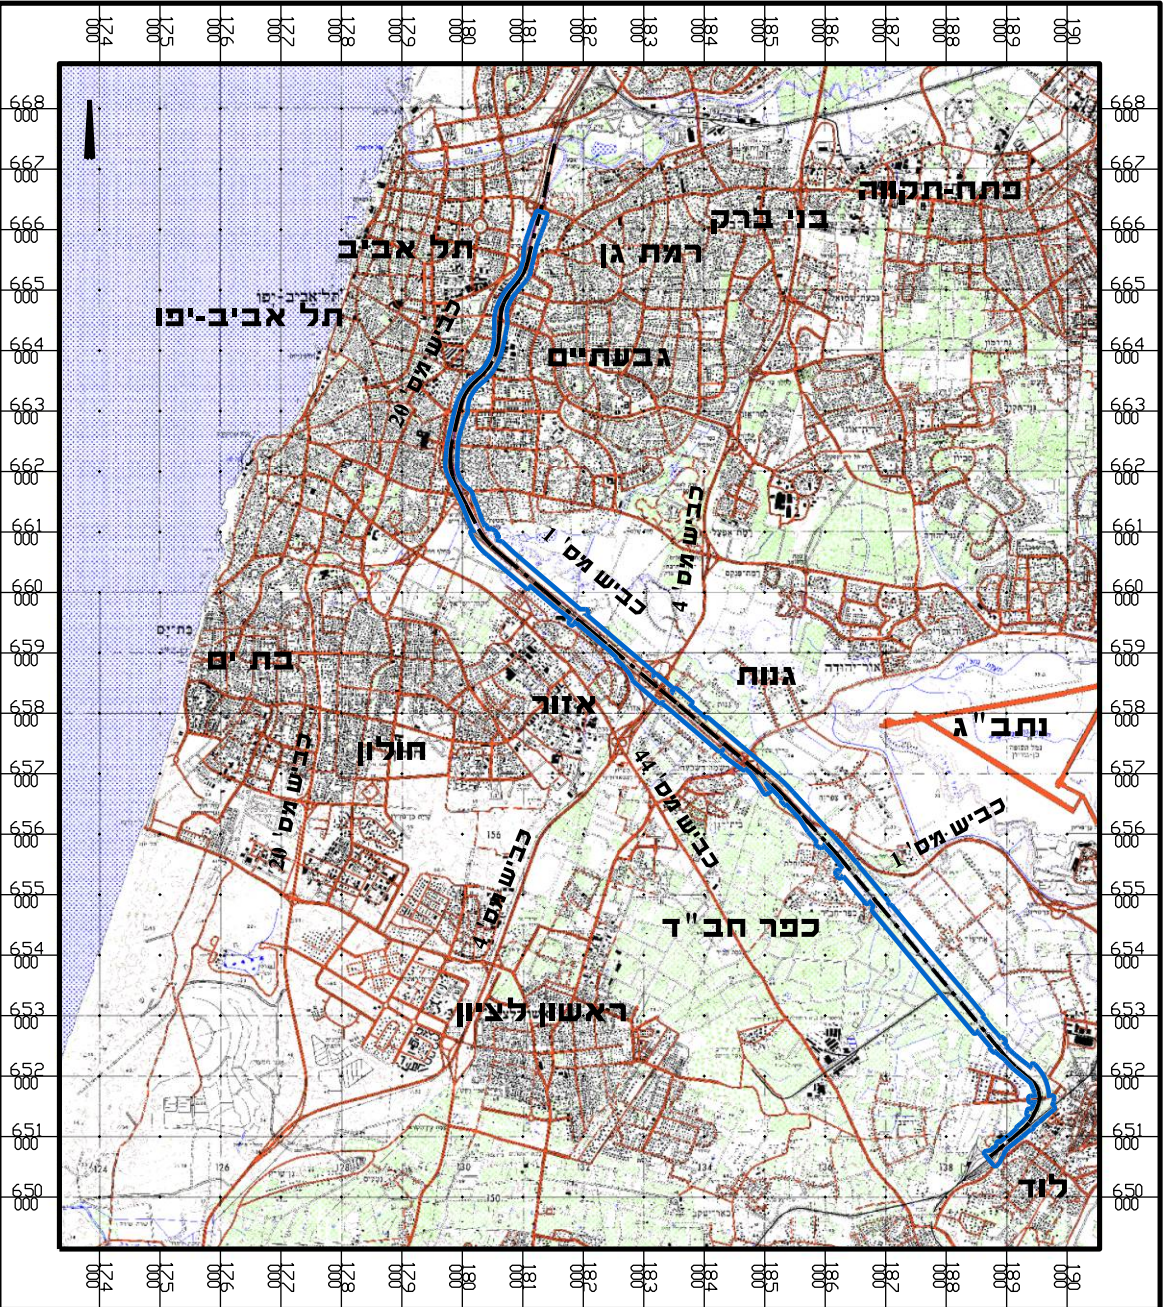

מפת מפתח:
קני"מ : 100,000

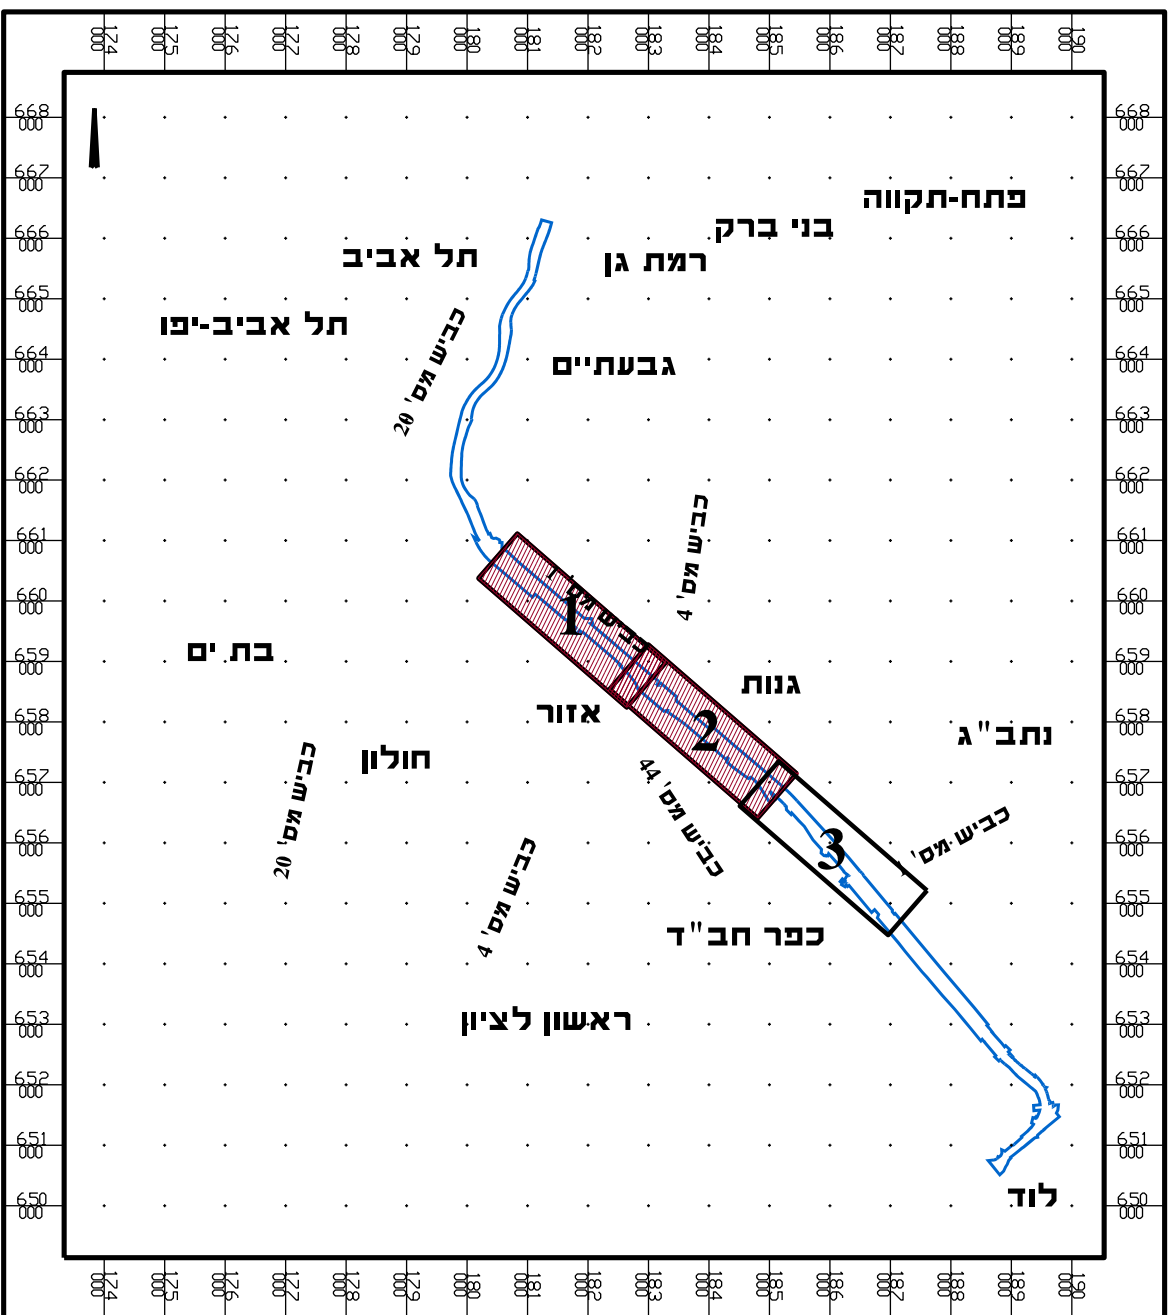

תכנון מחלק שפירים
בסטרת תמ"א 47

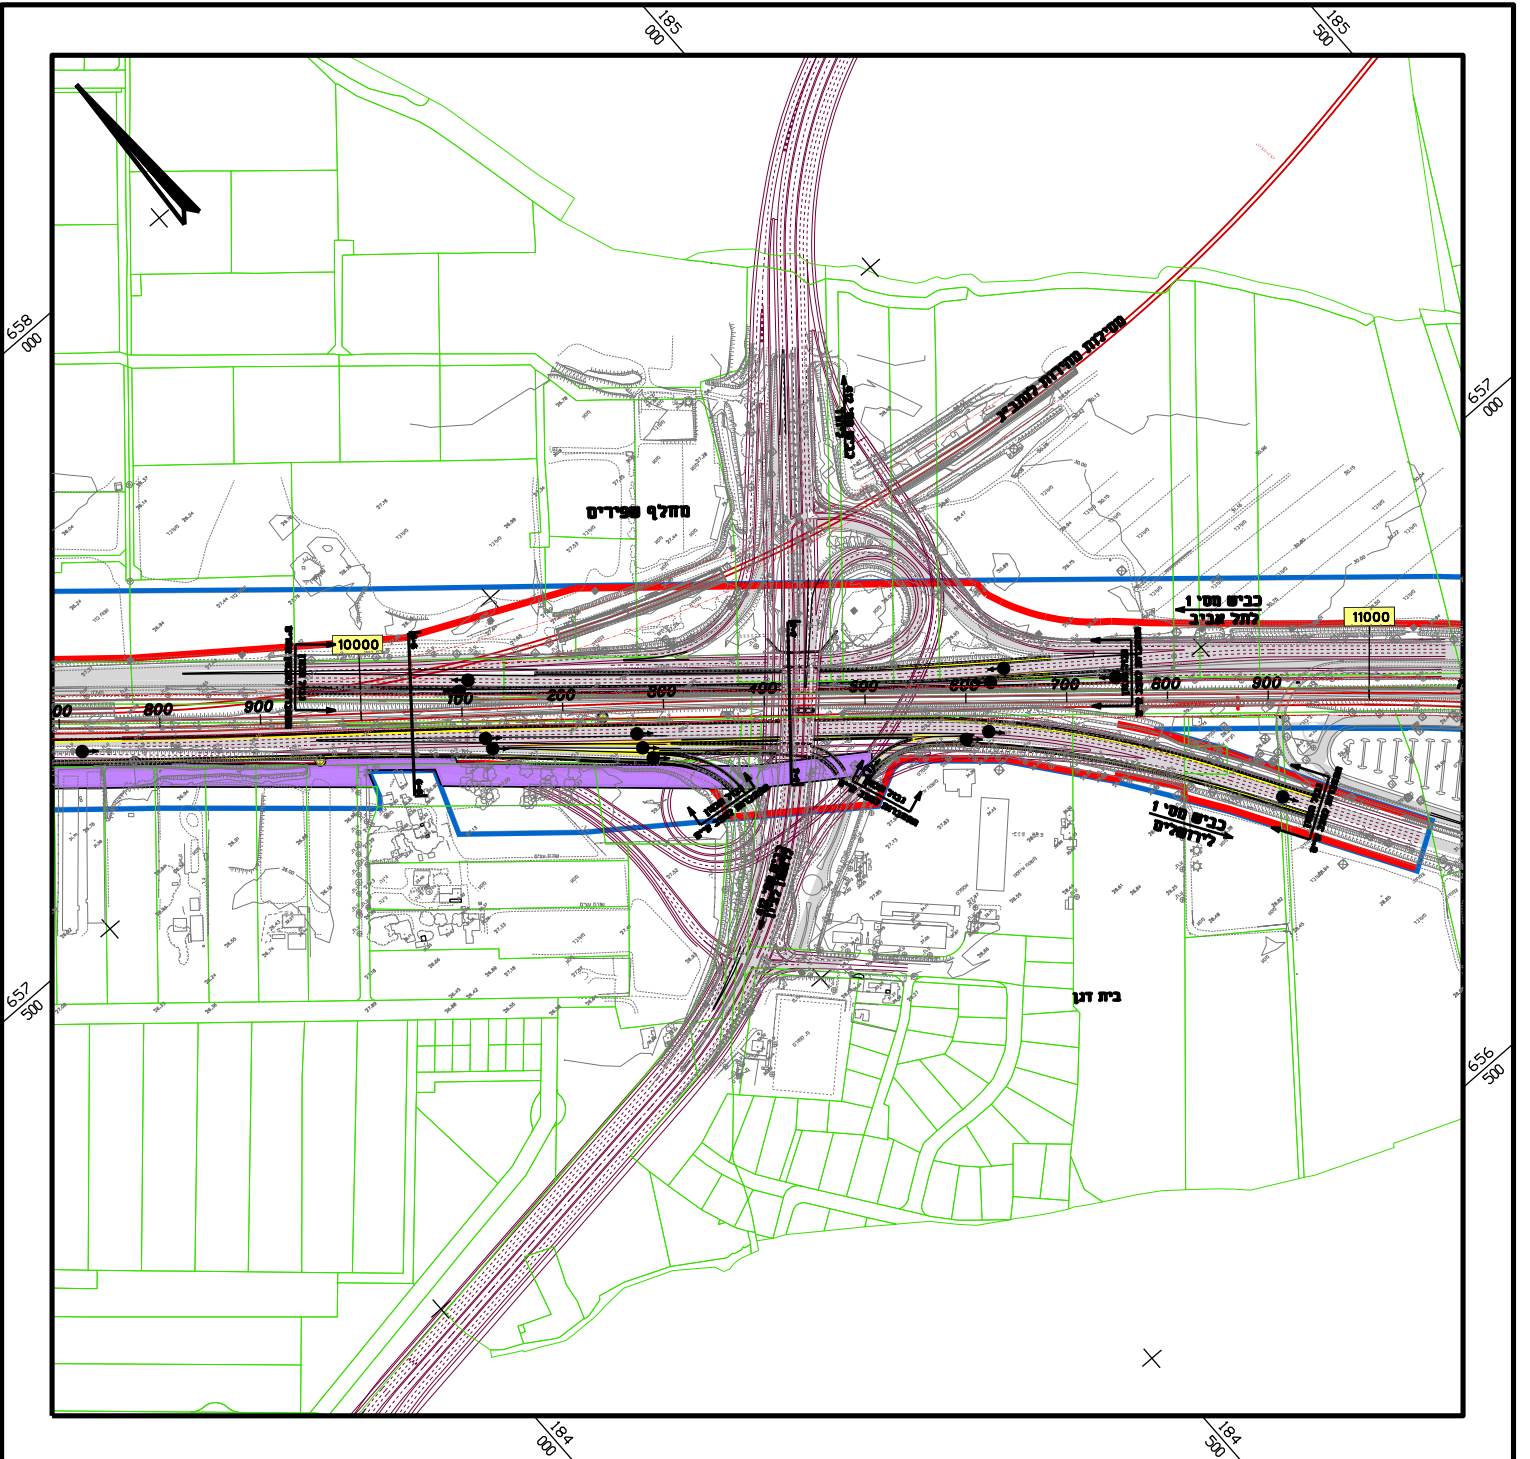

מקרא:

- גבול תחיל 33
- גבול זכות הדרך
- גבול זכות נחל מחובנו
- צד משטה מחובנו
- רציף מחובנו
- גבול רצועת רכבת
- חטט כביש קרימה
- דרך שירות מחובנו
- דרך תחילת מחובנו
- שכר אספלט מחובנו
- מעלה בנסו מחובנו
- מעלה מחובנו
- תכנון על ידי ראשונים
- עמודי חשמל דו-ערוץ
- רצועה מחובנו לאורך
- רצועה מחובנו משטח
- רצועה מחובנו לחוף

