תכנית תתל/ 33 15/05/2018 12:13:42 נספח תנועה תנועה על רקע תצ"א גיליון 2

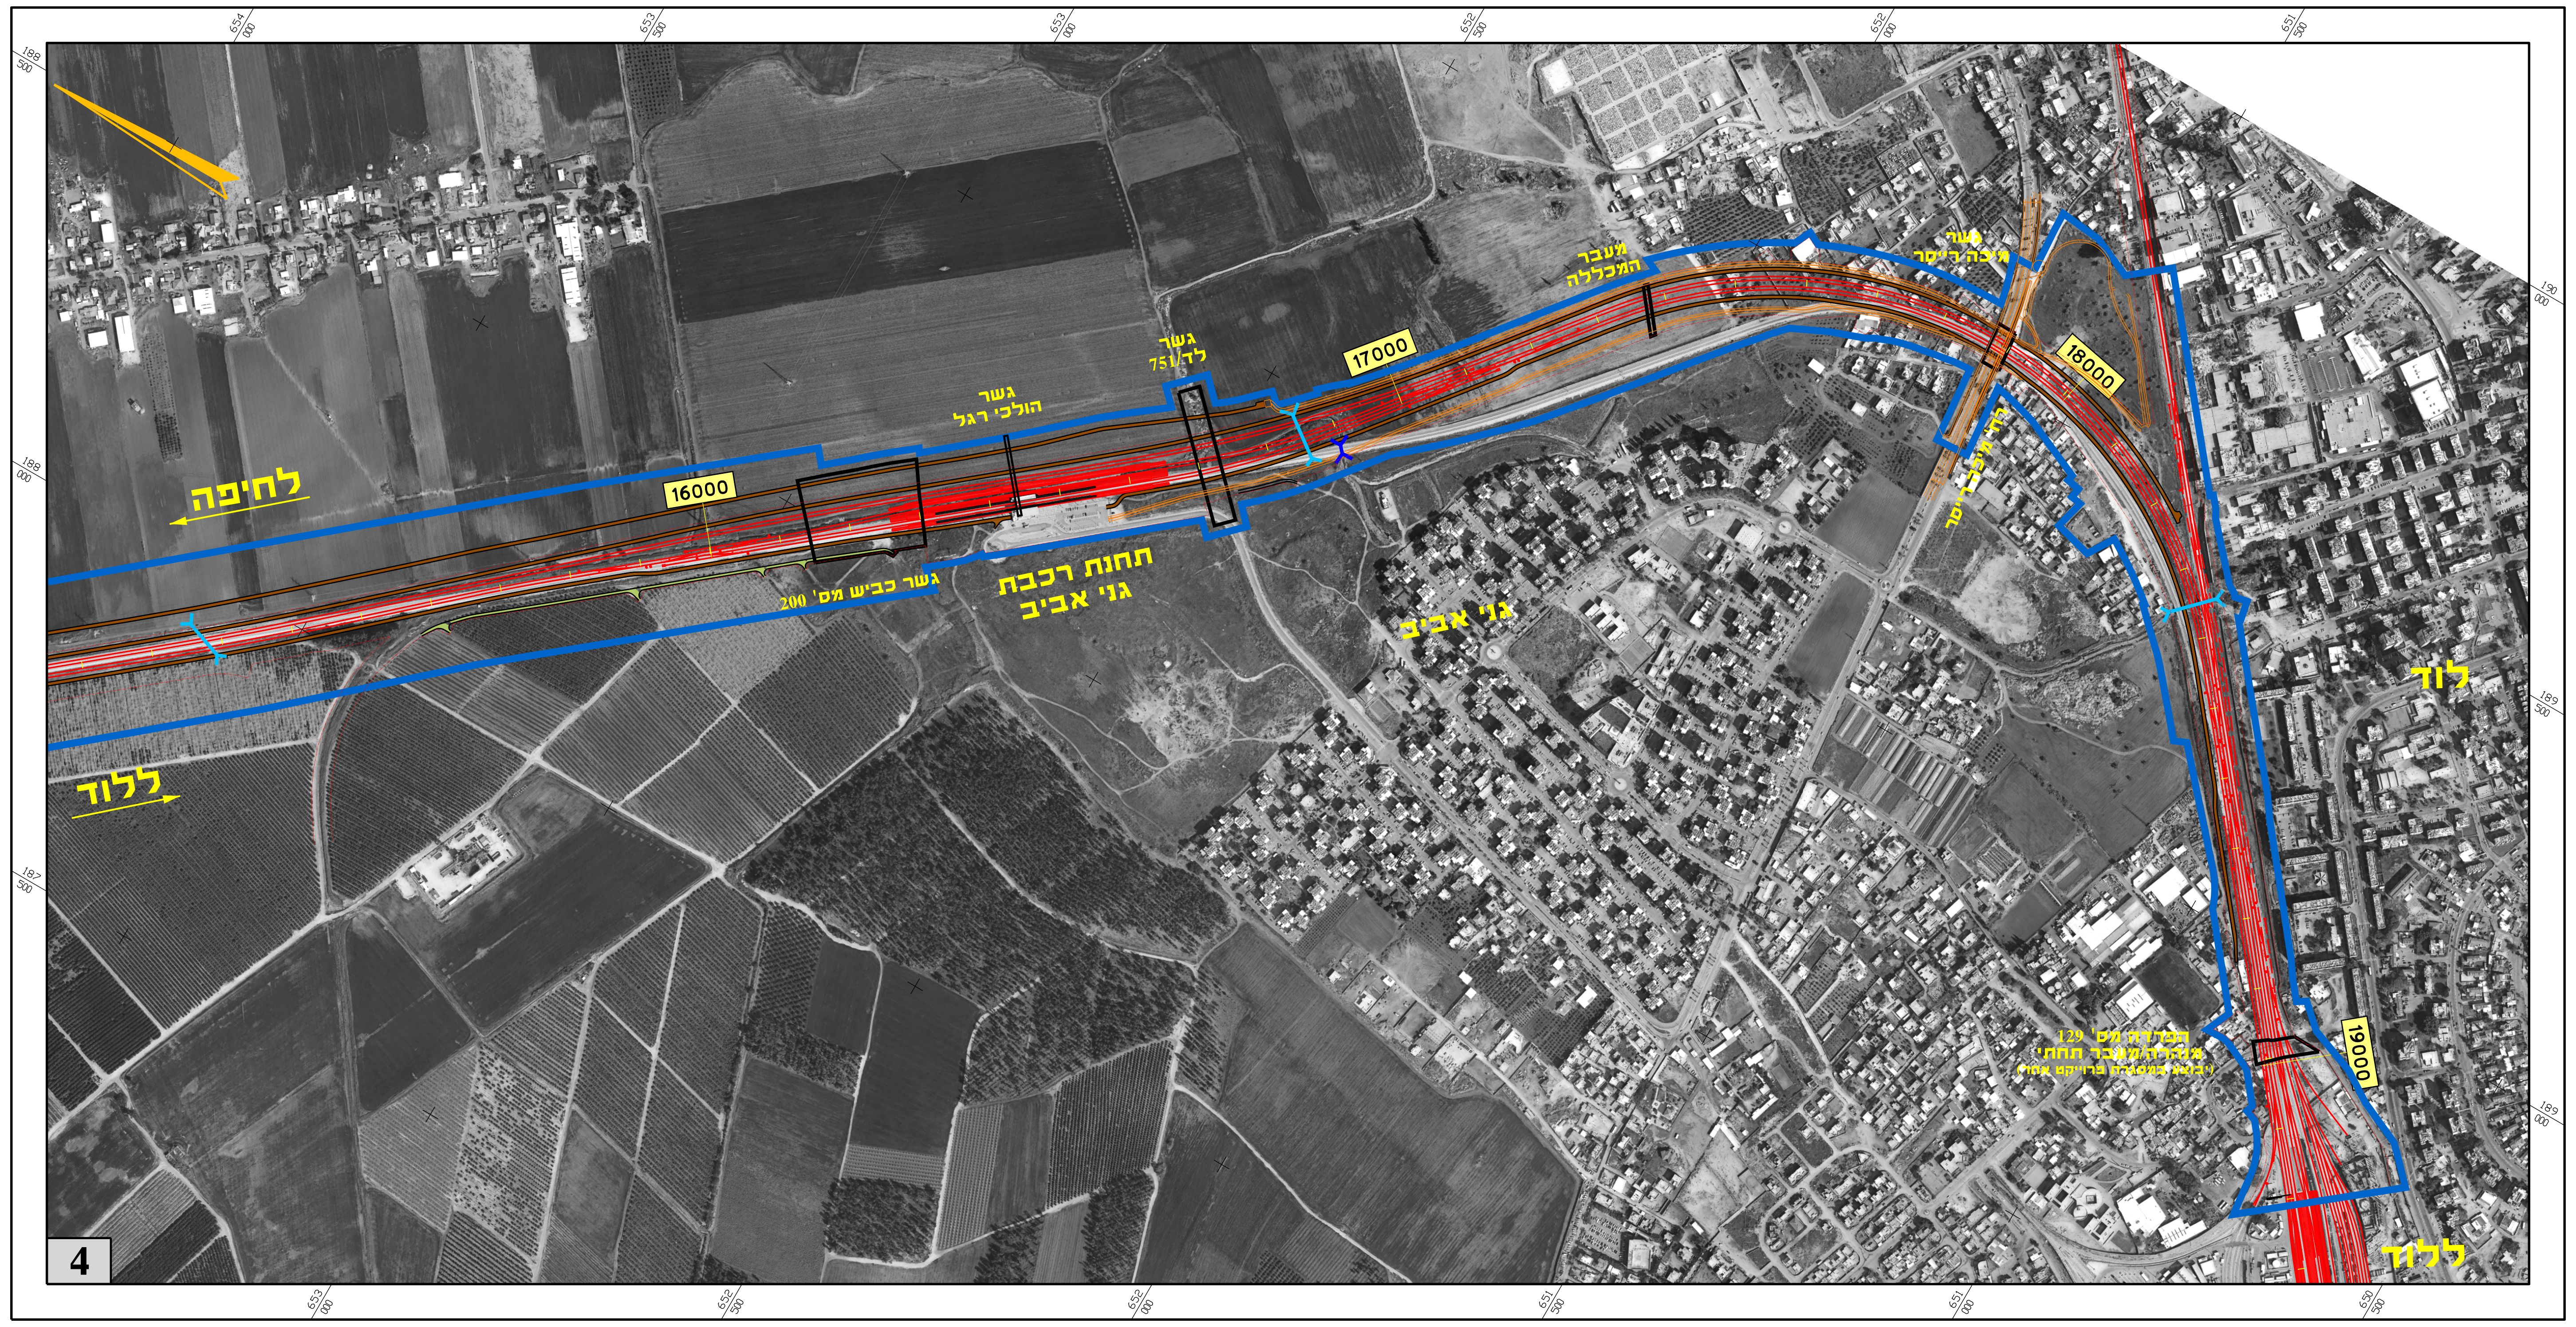
לחיפה
ללוד
16000
17000
18000
19000
גשר הולכי רגל
גשר לד/751
מעבר המכללה
גשר מיכה רייסר
גשר מיכה רייסר
תחנת רכבת גני אביב
גשר כביש מס' 200
גני אביב
לוד
ללוד
הפרדה מס' 129 מנהרה/מעבר תחתי (יבוצע במסגרת פרוייקט אחר)
4
654/000
653/500
653/000
652/500
652/000
651/500
651/000
650/500
188/500
188/000
187/500
190/000
189/500
189/000

תרשים סביבה :
קנ"מ 1 : 100 000

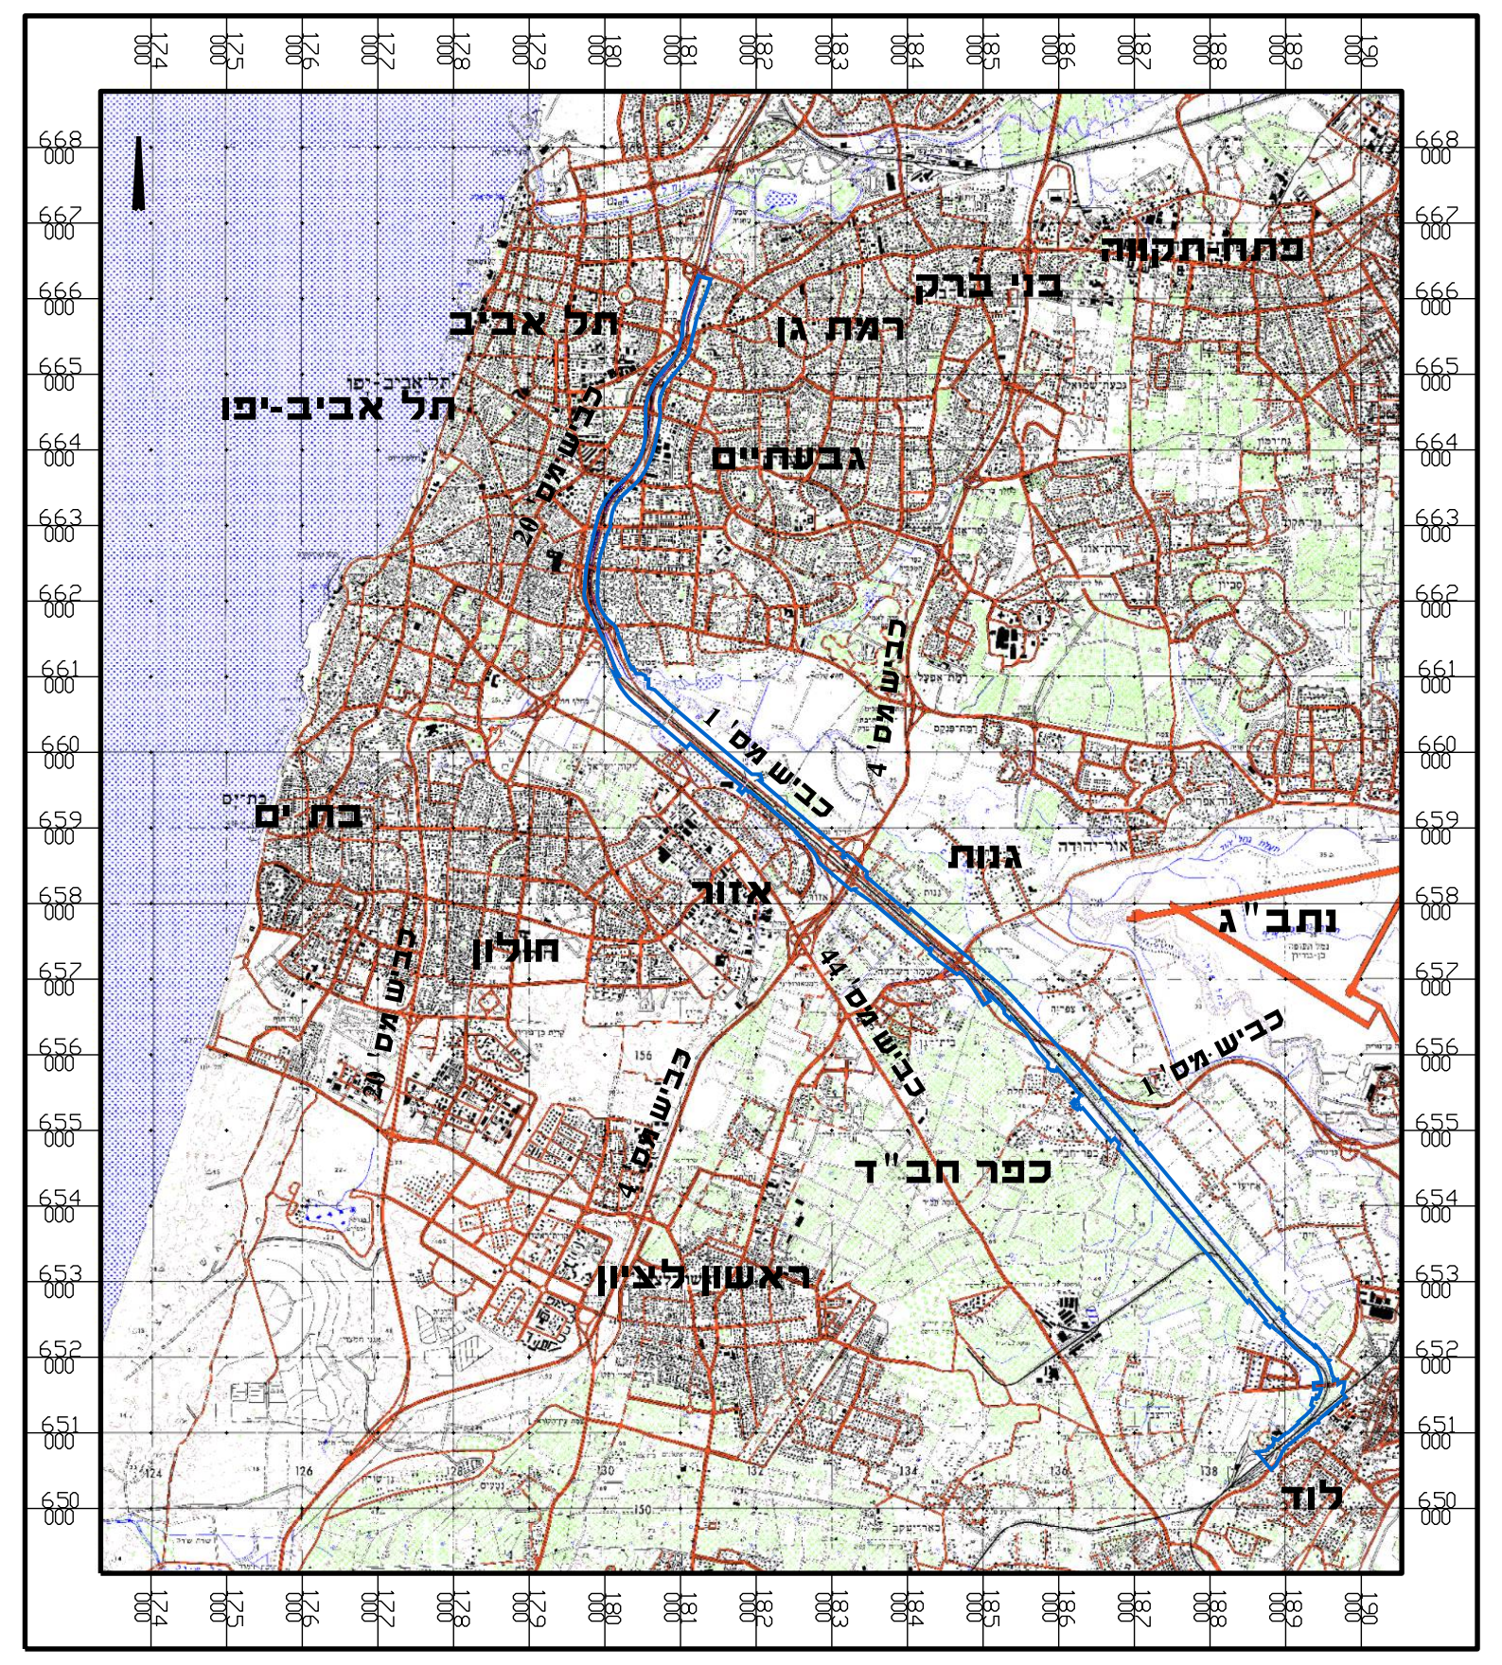
תל אביב
רמת גן
בני ברק
פתח-תקווה
תל אביב-יפו
גבעתיים
כביש מס' 20
כביש מס' 1
כביש מס' 4
בת ים
גנות
אזור
נתב"ג
חולון
כביש מס' 44
כביש מס' 1
כפר חב"ד
ראשון לציון
לוד

מפת מפתח:
קנ"מ 1 : 100 000

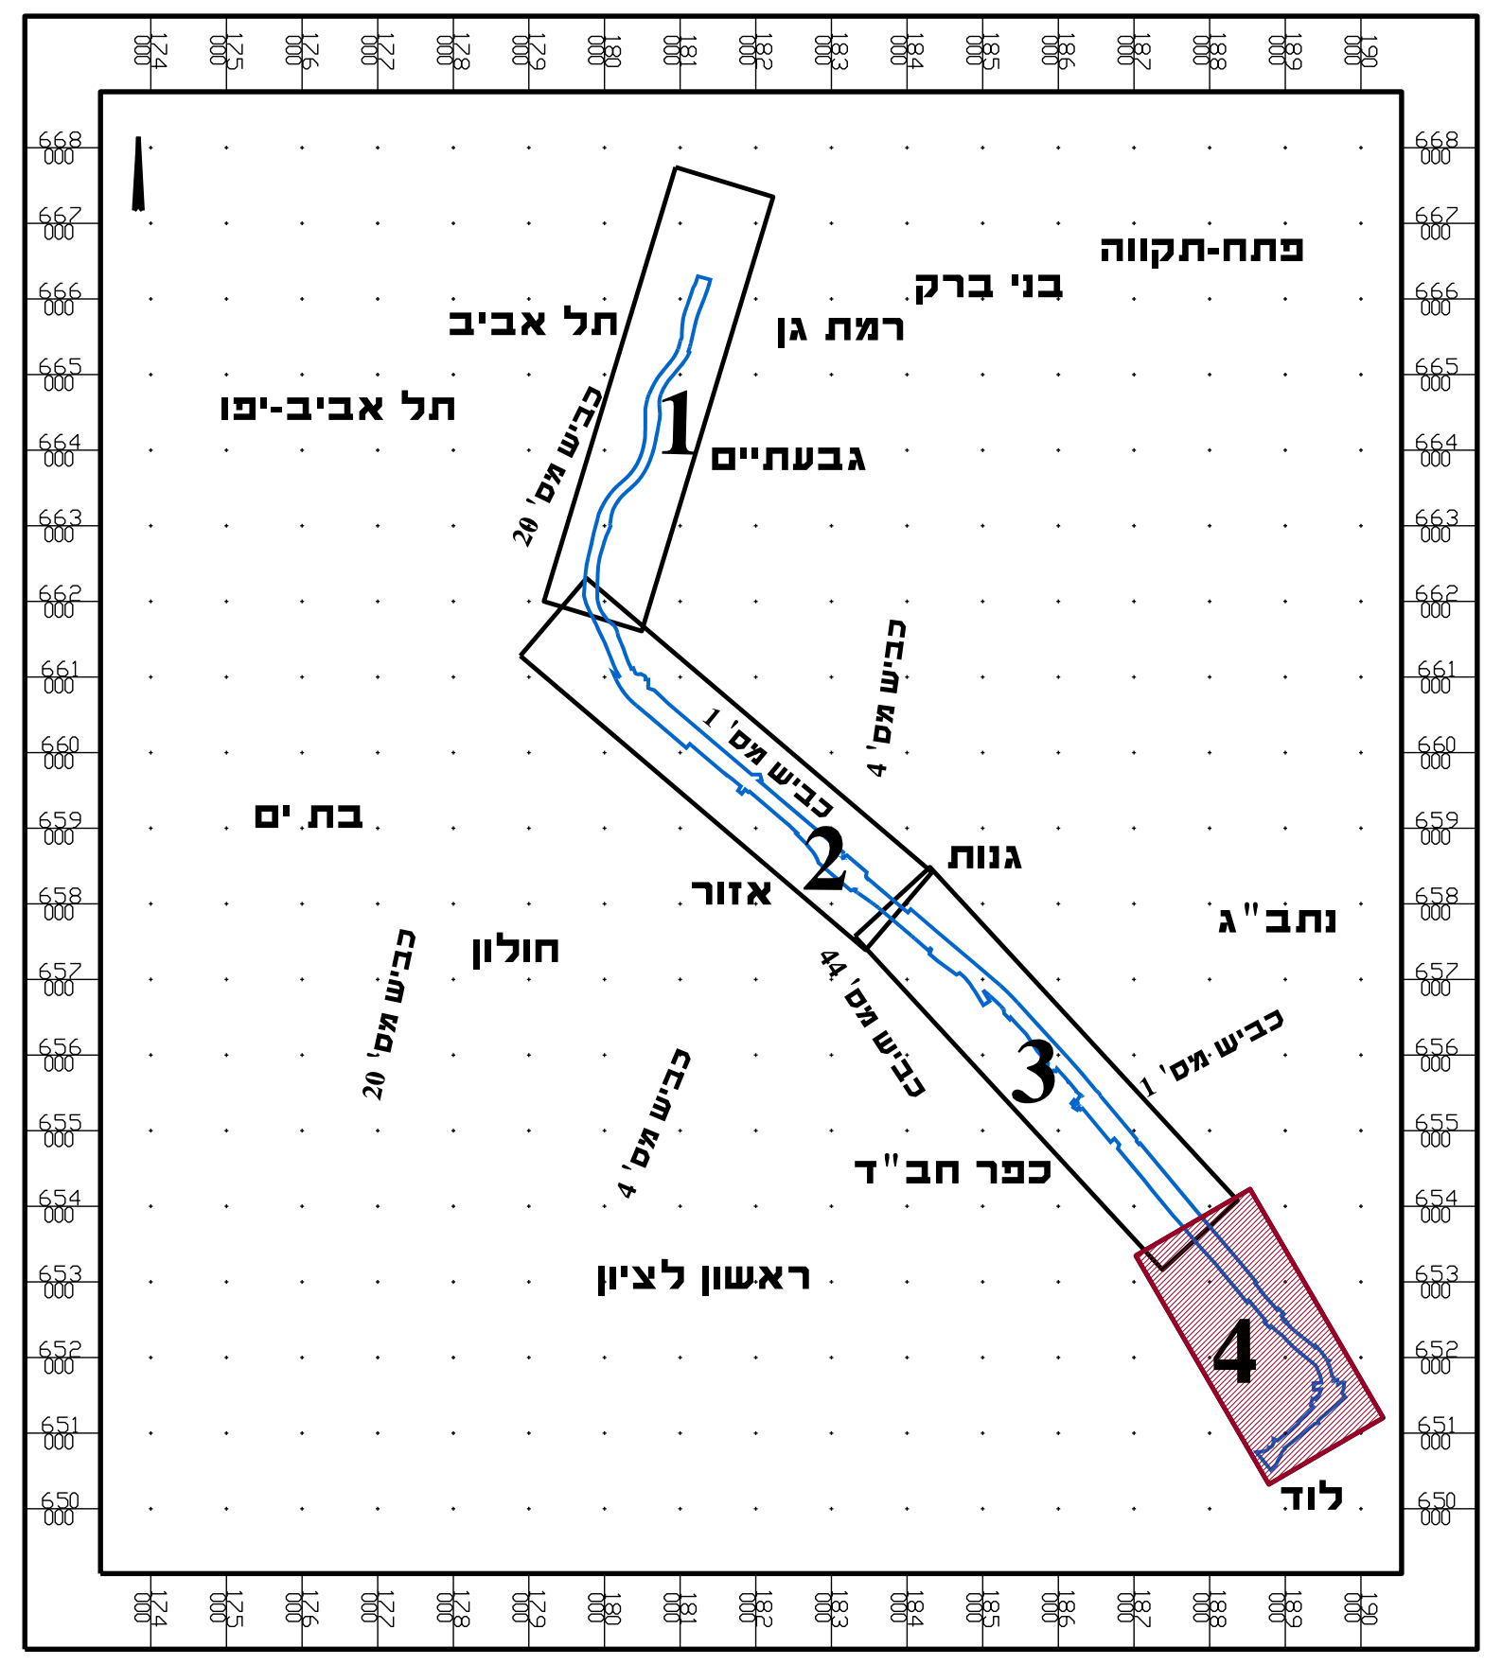
פתח-תקווה
בני ברק
רמת גן
תל אביב
תל אביב-יפו
1
גבעתיים
כביש מס' 20
כביש מס' 1
כביש מס' 4
בת ים
2
גנות
אזור
נתב"ג
חולון
כביש מס' 20
כביש מס' 44
3
כביש מס' 1
כביש מס' 4
כפר חב"ד
ראשון לציון
4
לוד

## מקרא :

- גבול תכנית
- גבול רצועת רכבת מוצע
- גבול זכות הדרך
- גבול זכות נחל מתוכנן
- רציף מתוכנן
- צירי מסילות רכבת
- גשר/מעבר מתוכנן
- גשר/מעבר תת קרקעי קיימים
- מעביר מים קיים
- מעביר מים מתוכנן
- 104000 מס' חתך/ק"מ
- תעלת ניקוז/תעלת בטון
- דרך שרות רכבת/ שרות כביש

חוק התכנון והבנייה, התשכ"ה- 1965
הועדה הארצית לתכנון ולבניה של תשתיות לאומיות

# תת"ל 33

## מסילה רביעית באיילון
קטע ת"א מרכז-לוד

תכנית לתשתית לאומית

## תנוחה על רקע תצ"א

גליון מס' 2 (מקטע 4) מתוך 2
קנ"מ : 1 : 5,000

מחוז: תל אביב,מרכז
מרחבי תכנון מקומיים:

- ועדה מקומית תל אביב-יפו
- ועדה מקומית רמת גן
- ועדה מקומית גבעתיים
- מרחב תכנון מחוזי-מקומי (מחוז ת"א)
- ועדה מרחבית אור יהודה-אזור
- ועדה מרחבית מצפה אפק
- ועדה מקומית עמק לוד
- ועדה מקומית לוד

חותמת מוסד התכנון :

שלב: אישור תכנית מהדורה: 14 תאריך: 25.04.2018

| | |
|---|---|
| מדינת ישראל<br>משרד האוצר<br>הועדה הארצית לתכנון ולבנייה של תשתיות לאומיות | חתימה וחותמת |
| בעלי קרקע<br>מדינת ישראל ואחרים | חתימה וחותמת |
| יוזמי התכנית | חתימה וחותמת |

מנהל פרוייקט : חתימה וחותמת

| שם: | תפקיד: | מס' ת"ז | כתובת: |
|---|---|---|---|
| איתי עובדיה | מנה"פ | 023518210 | רח. יגאל אלון 67 , תל אביב |
| טלפון: | פקס: | דוא"ל: | שם: |
| 03-6251222 | 03-6251223 | itay@yahel-eng.co.il | |

עורך התוכנית: חתימה וחותמת

| שם: | תפקיד: | מס' ת"ז | כתובת: |
|---|---|---|---|
| אלכס לרנר | מתכנן | 308640283 | רח. היוזמה 4 , טירת הכרמל |
| טלפון: | פקס: | דוא"ל: | שם: |
| 04-8569000 | 04-8569010 | yenon@yenon.co.il | ינון-תכנון יעוץ ומחקר בע"מ |

מודד מוסמך: חתימה וחותמת

| שם: | מודד מוסמך | מס' ת"ז | כתובת: |
|---|---|---|---|
| ברנרד גטניו | 570 | 052602984 | רח. הירקון 67 , בני ברק |
| טלפון: | פקס: | דוא"ל: | שם: |
| 03-7541000 | 03-7516353 | info@datamap.com | |

הריני מצהיר בזאת כי מדידת המפה הטופוגרפית/המצבית המהווה רקע לתוכנית זו, נערכה על ידי ביום ________
והיא הוכנה לפי הוראות נוהל מבאית ובהתאם להוראות החוק ולתקנות המודדים שבתוקף.
דיוק הקו הכחול והקדסטר: מדידה גרפית/ קו כחול (בכבד) ברמה אנליטית/ מדידה אנליטית מלאה ברמת תצ"ר (כולל הקו הכחול)

שם המודד ________ מספר רישיון ________ חתימה ________ תאריך ________

az-Tn-4 25/04/2018 12:31:19 alinag S:\2080\SHEET\PD-FA\SP\Taza_Tnuha_2080.dgn