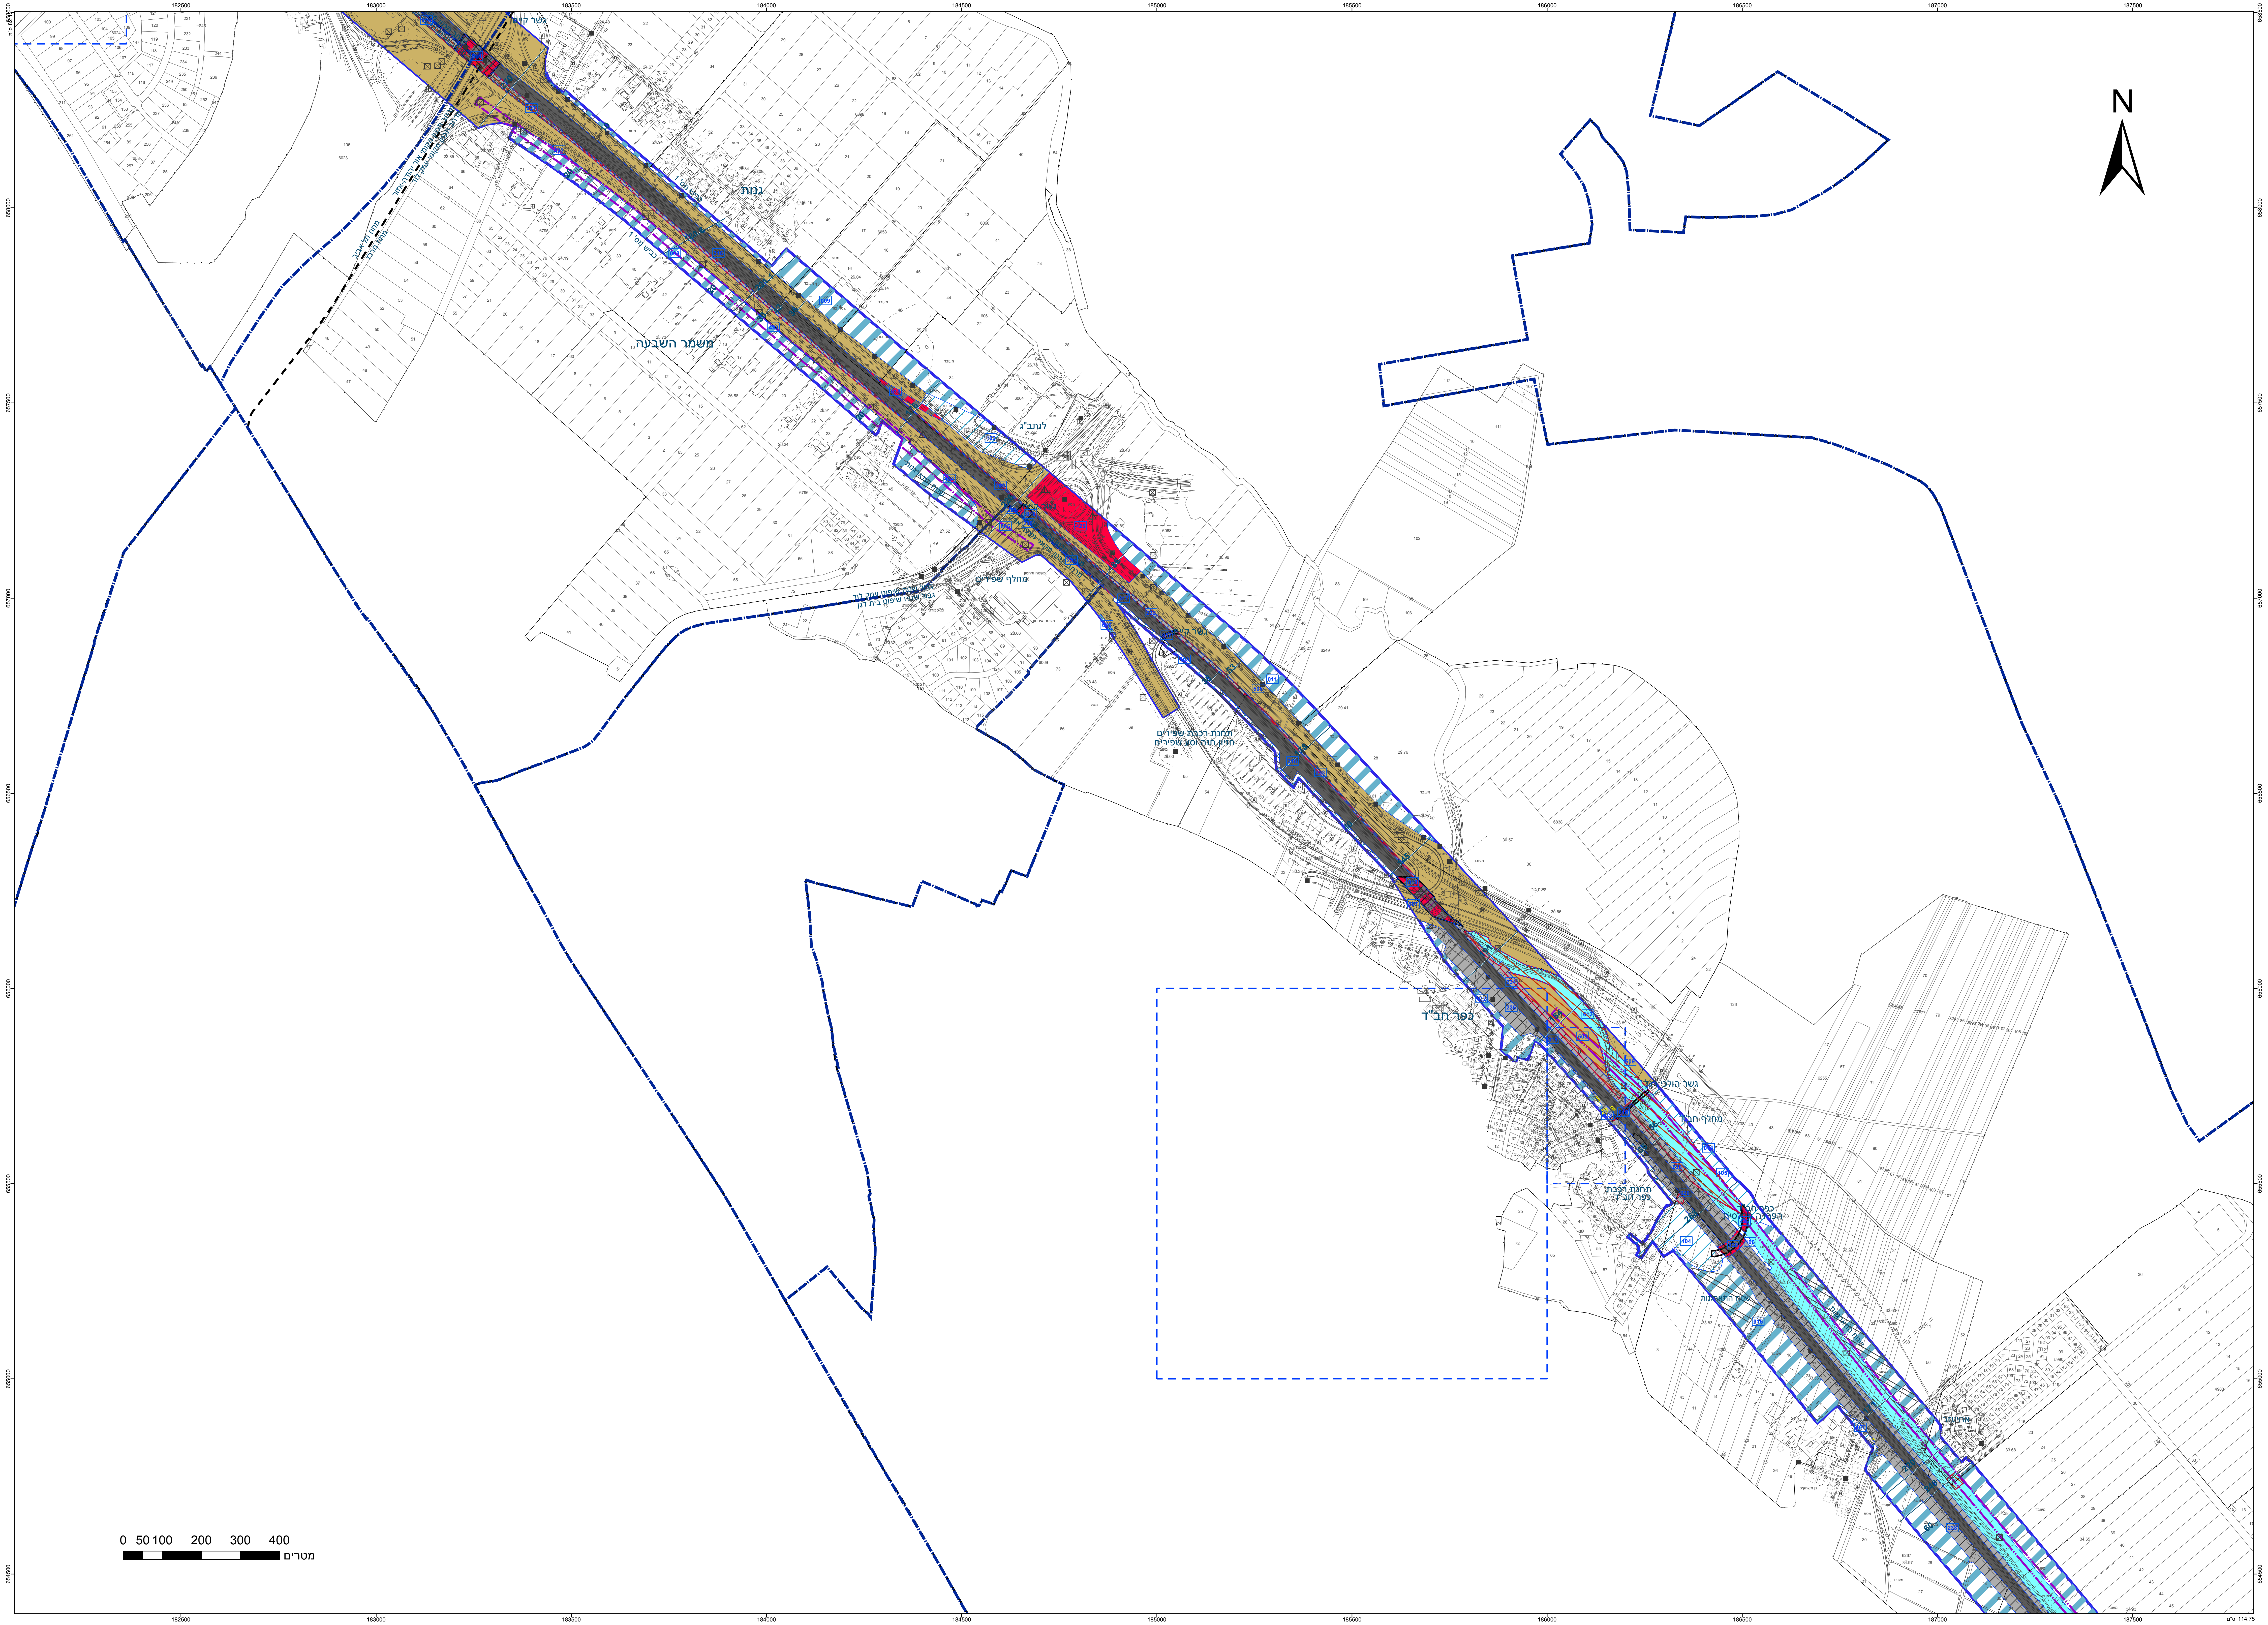
N
גשר קיים
גנות
כביש מס' 1
משמר השבעה
מחוז תל אביב
מחוז מרכז
לנתב"ג
מחלף שפירים
גבול שטח שיפוט עמק לוד
גבול שטח שיפוט בית דגן
תחנת רכבת שפירים
חניון חנה וסע שפירים
כפר חב"ד
גשר הולכי רגל
מחלף חב"ד
תחנת רכבת כפר חב"ד
כפר חב"ד הפרדה מפלסית
שטח התארגנות
אחיעזר
0 50 100 200 300 400
מטרים
182500
183000
183500
184000
184500
185000
185500
186000
186500
187000
187500
658500
658000
657500
657000
656500
656000
655500
655000
654500

מקרא

▭	גבול תכנית
140	תא שטח ומספרו
גוש 1234	גבול גוש ומספרו
5	גבול חלקה ומספרה

רוזטת דרך: 1 מספר הדרך, 2 קוי בנין, 3 רוחב הדרך

🟦	נחל/תעלה/מאגר מים
🟫	דרך מאושרת
🟥	דרך מוצעת
⬛	מסילה מאושרת
▨	מסילה מוצעת
▨	מפגש דרך-מסילה
▨	יעוד עפ"י תכנית מאושרת אחרת
▨	מגבלות בניה ופיתוח
▩	גשר/מעבר עילי
▨	הנחיות מיוחדות
▨	דרך/מסילה לביטול
▭	אתר עתיקות/אתר הסטורי
▭	מבנה להריסה
▭	גבול מסדרון תשתיות ת"ק
▭	גבול מסדרון תשתיות עילי
— —	גבול מרחב תכנון
—·—	גבול שטח שיפוט
—	מידות

מקרא מפת מדידה

מקרא

מבנה	▭	שוחת ביקורת כללית	Ⓣ
צריף\סככה\חממה	▭	עמוד כללי	Ⓤ
אספלט	—	ארון כללי	ע
אבן שפה	— —	עמוד תאורה	⊗
דרך עפר	— —	עמוד תקשורת	◎
גדר תיל \ רשת	—×—×	ע. חשמל עץ	○
גדר אבן\קיר	—	ע. חשמל בטון	◐
גדר אבן קיר אבן\ גדר\ בטון	— —	ע. חשמל תעלה	●
שפת ואדי	—	ע.חשמל, זוית	■
מדרון עליון\ שיפוע טבעי	┬┬┬	שוחת גוב\ מים	Ⓜ
עץ	♣	שוחת ביוב	ⓑ
נקודת גובה אופיינית	12.85	שוחת ניקוז	ⓝ
קו גובה משני (1.0, 0.5 מ')	~	גוב תקשורת	▭
קו גובה ראשי (5.0, 2.5, 1.0 מ')	—123—		

תרשים התמצאות - קנ"מ 1:120000

תל-אביב-יפו
בני ברק
רמת גן
גבעתיים
פתח תקווה
בת ים
חולון
אזור
ראשון לציון
לוד
נס ציונה
רמלה
באר יעקב
1
2
3
4

שנת צילום אויר: 2015

תרשים סביבה - קנ"מ 1:30000

חוק התכנון והבנייה, התשכ"ה - 1965

תכנית לתשתית לאומית

מס' תתל/ 33

מסילה רביעית באיילון, קטע ת"א מרכז - לוד

תשריט מצב מוצע גיליון 3 מתוך 4

מחוז	מרכז, תל-אביב
מרחב תכנון מקומי	כמפורט בהוראות / הודעה
רשות מקומית	כמפורט בהוראות / הודעה
ישוב	כמפורט בהוראות / הודעה
תכנית בסמכות	ארצית
איחוד וחלוקה	ללא איחוד וחלוקה
היתרים או הרשאות	תכנית שמכוחה ניתן להוציא היתרים או הרשאות
מונה תדפיס התשריט	44
מועד הפקה	11/06/2018 12:16
שטח התכנית	3542.037 דונם
קנה מידה	1:5000

אישורים

שמות*

מגיש התכנית	חברה/תאגיד ממשלתי תאגיד: נתיבי ישראל - החברה הלאומית לתשתיות תחבורה בע"מ
עורך ראשי	אלכס לרנר תאגיד: ינון תכנון יעוץ ומחקר בע"מ
יזם	חברה ממשלתית תאגיד: נתיבי ישראל - החברה הלאומית לתשתיות תחבורה בע"מ

בעלי ענין בקרקע*

טבלת גושים וחלקות (הוקלדו ידנית)*

מספר גוש	חלק/ כל הגוש	מספרי חלקות בשלמותן	מספרי חלקות בחלקיותן

* הרשימה המלאה מפורטת בהוראות התכנית / בהודעה שפורסמה בעיתונות וברשומות

הריני מצהיר בזאת כי המפה הטופוגרפית/המצבית המהווה רקע לתכנית זו, נערכה על ידי ביום 09.03.2017 והיא הוכנה לפי הוראות נוהל מבא"ת ובהתאם להוראות החוק ולתקנות המודדים שבתוקף. דיוק הקו הכחול והקדסטר:
מדידה גרפית

שם המודד	מספר רשיון	חתימה	תאריך
גטניו ברני מודד מוסמך	570		

גרסת מערכת 12.2015