



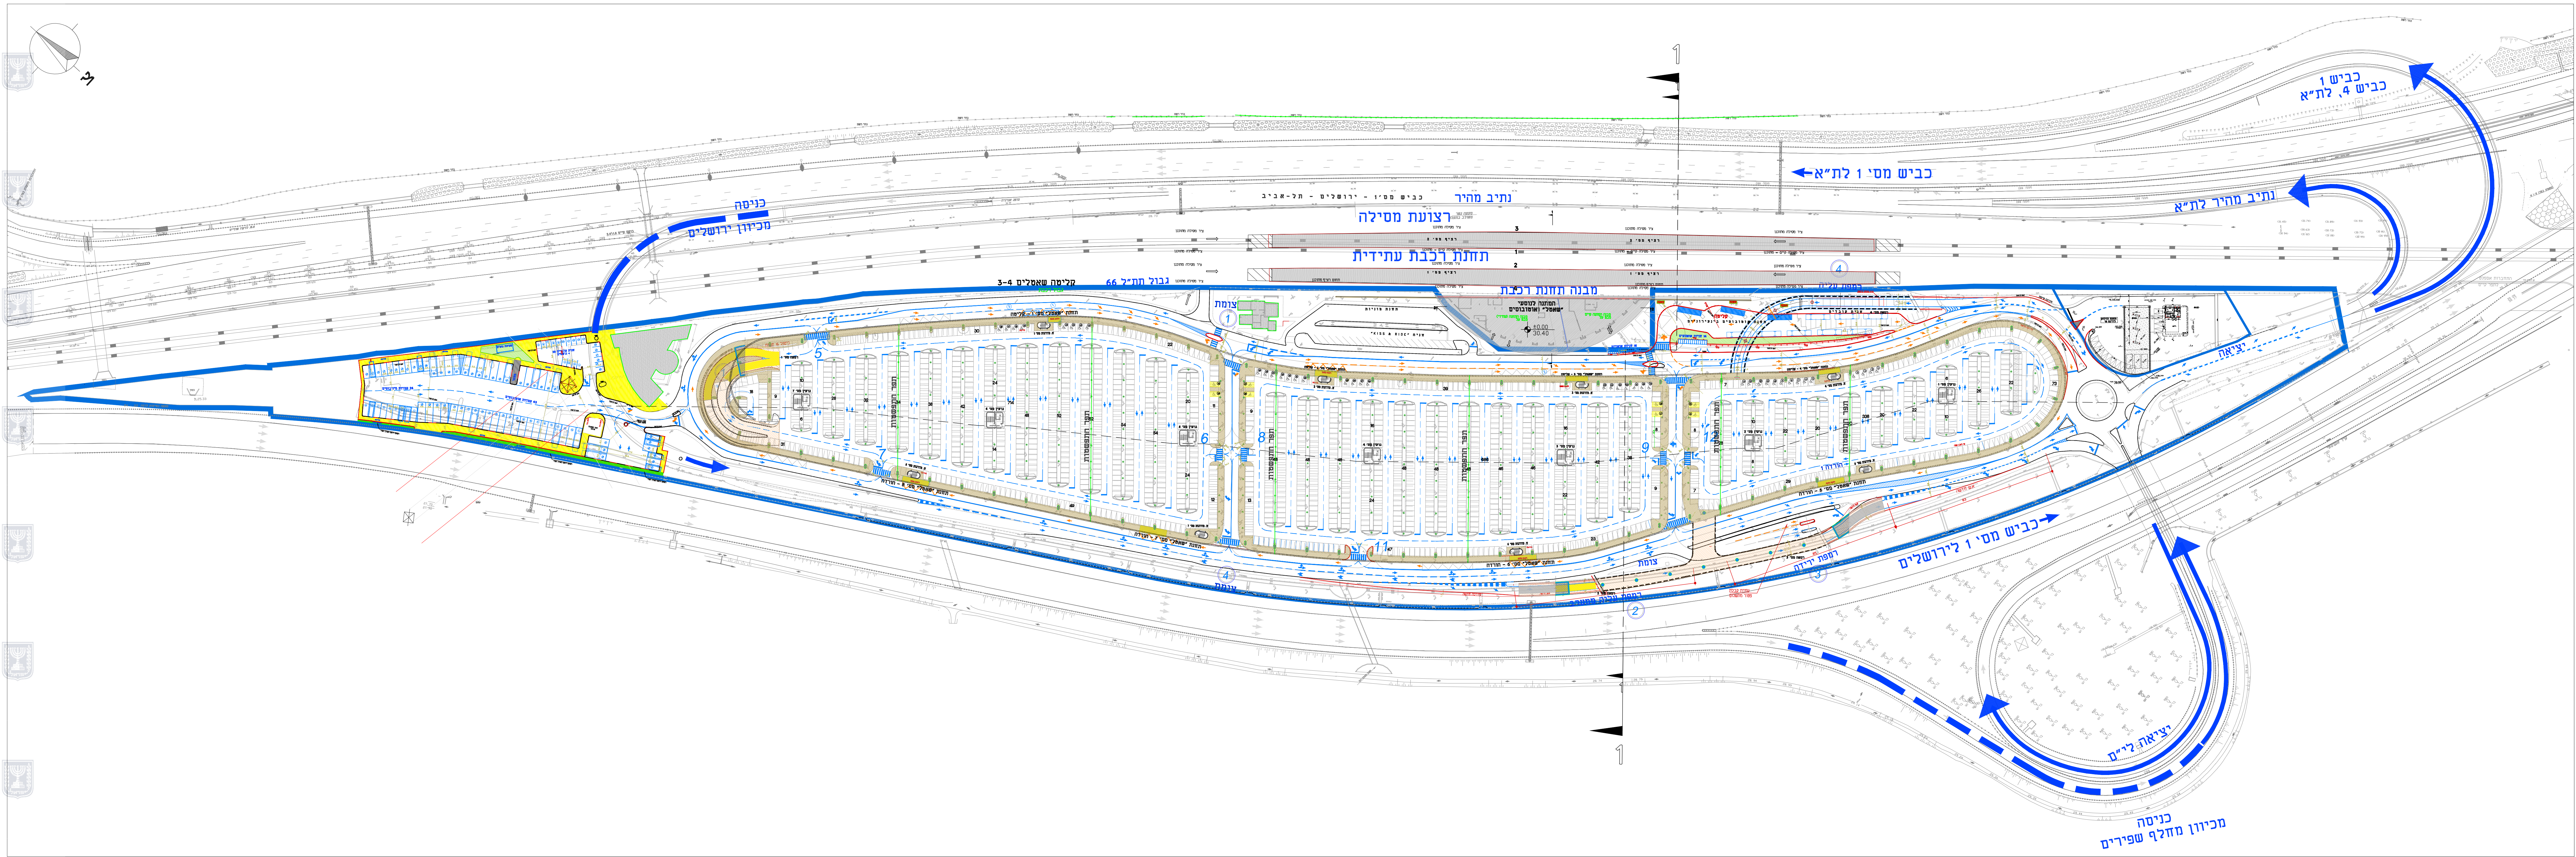

ק.מ 1:1000

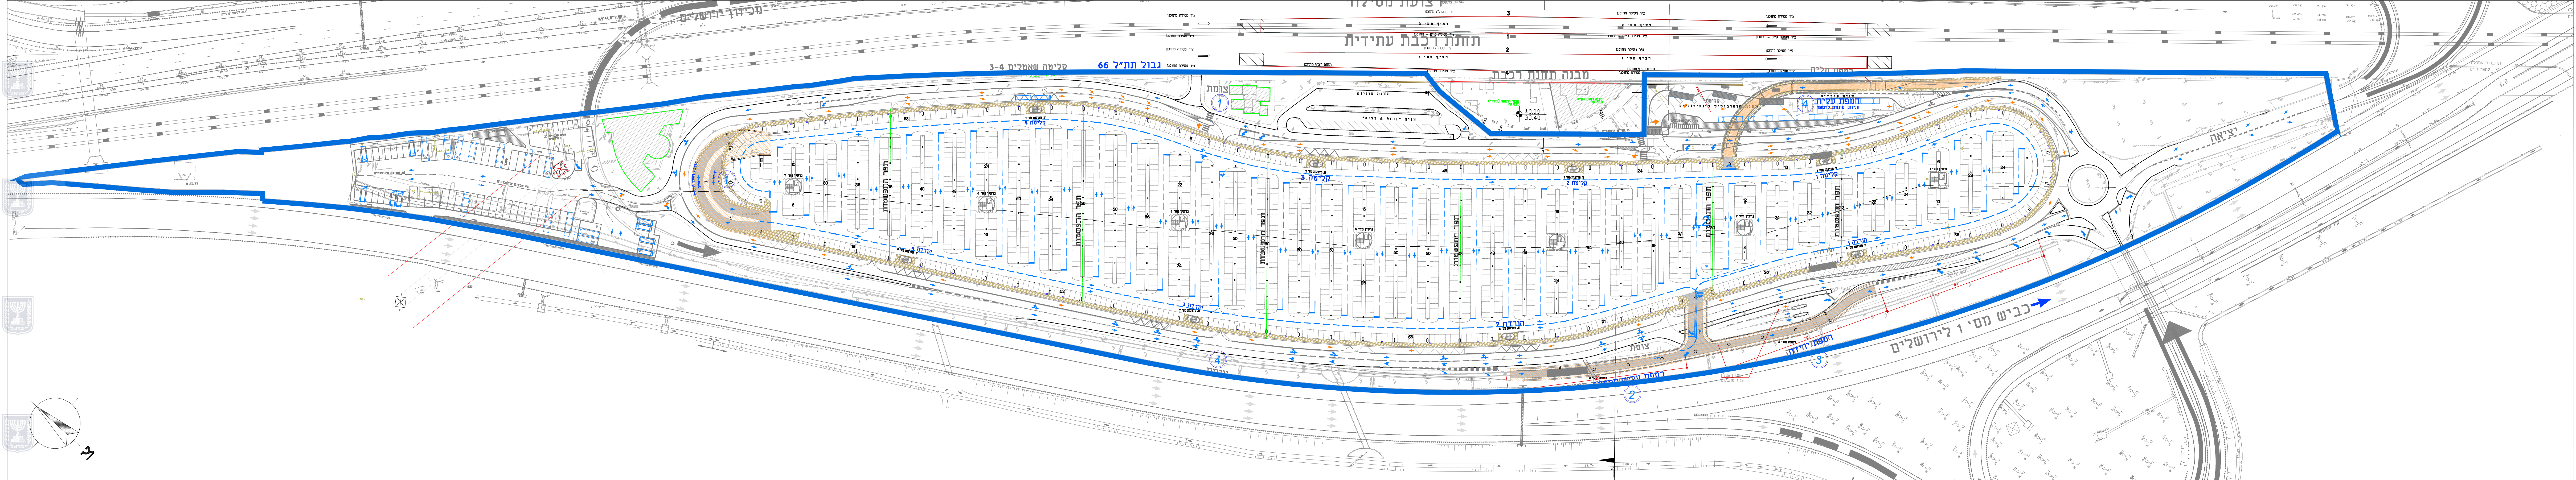


ק.מ 1:1000



קומת קרקע מפלס קיים.

חוק התכנון והבנייה, התשכ"ה - 1965 תכנית לתשתית לאומית	
תת"ל\66	
"חנה וסע" שפירים	
תשריט נספח תנועה	גליון_1 מתוך_2
מחזור	המרכו
מרחב תכנון מקומי	עמק לוד
רשות מקומית	מועצה אזורית עמק לוד
ישוב	
תאריך	21/09/15
שם הנספח	קו"מ
נספח תנועה	11000
תרשים סביבה	150.000
תרשים נוסף	110.000
תרשים נוסף	-
תמונה נוספת	-
שמות ודתימות:	
עורך התוכנית	שם: ניצן ארד תאריך: תחילת שנת 2015
	חתימה: תחילת שנת 2015

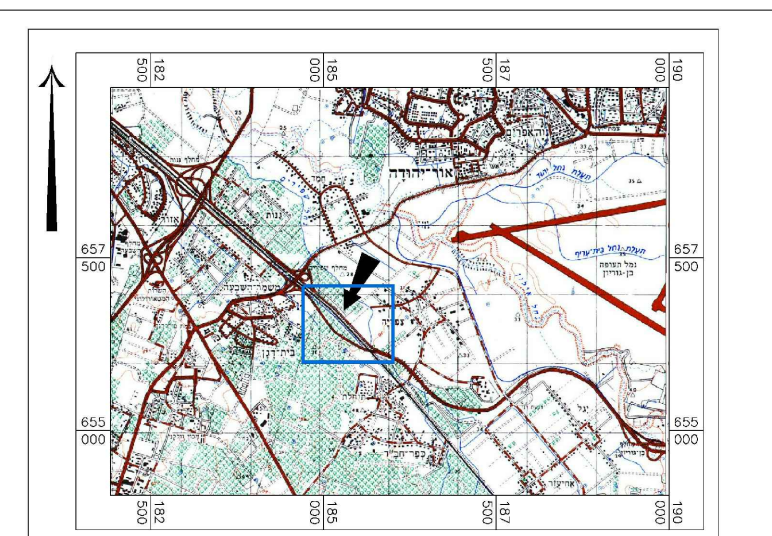

טבלת חניות חנה וסע שפירים

מפלס	קיים	מתוכנן	השינוי
פרטיות:			
קומת קרקע	2,110	1,815	(-294)
מפלס +1	—	1,970	(+1970)
סה"כ	2,110	3,785	(+1675)
אוטובוסים			
	30	65	(+35)
דו גלגלי			
	20	30	(+10)

*כולל חניות נכים ע"י התקן