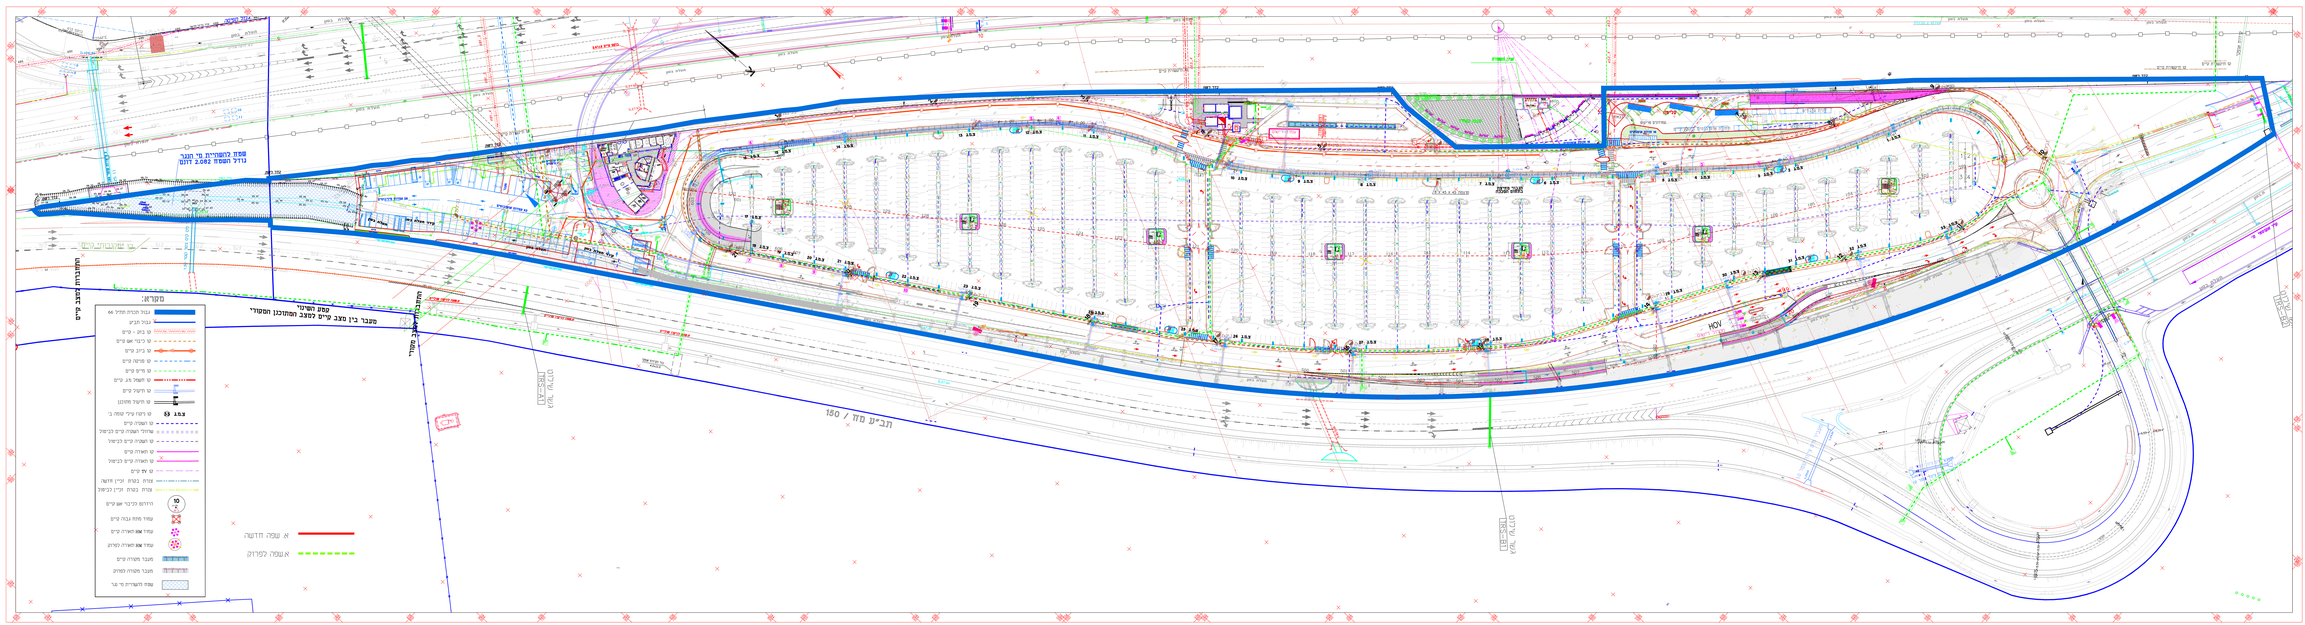

שטח להשהיית מי הנגר
גודל השטח 2.082 דונם
גבול תפיסה
תעלת בטון
גדר רשת
עמדות מיניבוסים 26
עמדות אוטובוסים 43
קו "מקורות" קיים
קו תיקשורת קיים
התחברות למצב קיים
קטע השינוי
מעבר בין מצב קיים למצב המתוכנן המקורי
התחברות למצב מקורי
150 / תב"ע מחז
גשר שירות TRS-A1
גשר שירות TRS-B1
גשר שירות TRS-B2
HOV
מסלול רישום
עמדת רישום
קליטה
עמודונים פריקים
תחנת אוטובוסים
חניות אופנועים 14
עמדת אבטחה
כניסה
מגבור משפטים בתחום הסככה
מרצפת 45 X 45 X 8
כביש
בור לקידום אפקר
4.0x11.0
א.שפה לניקוז שוליים
מקרא:
גבול תכנית תת"ל 66
גבול תב"ע
קו בזק - קיים
קו כיבוי אש קיים
קו ביוב קיים
קו סניקה קיים
קו מים קיים
קו חשמל מ.ג. קיים
קו תיעול קיים
קו תיעול מתוכנן
קו ניקוז עילי קומה ב'
צ.מ.ג
קו השקיה קיים
שרוולי השקיה קיים לביטול
קו השקיה קיים לביטול
קו תאורה קיים
קו תאורה קיים לביטול
קו TV קיים
צנרת בקרת זכיין חדשה
צנרת בקרת זכיין לביטול
הידרנט לכיבוי אש קיים
עמוד מתח גבוה קיים
עמוד HM תאורה קיים
עמוד HM תאורה לפרוק
מעבר מקורה קיים
מעבר מקורה לפרוק
שטח להשהיית מי נגר
א. שפה חדשה
א.שפה לפרוק

חוק התכנון והבנייה, התשכ"ה – 1965
תכנית לתשתית לאומית

תת"ל\66

"חנה וסע" שפירים

תכי פרוקים מערכות קיימות בתחום מ.ח.150 גליון 1 מתוך 1

מחוז	המרכז
מרחב תכנון מקומי	עמק לוד, מצפה אפק
רשות מקומית	מועצה אזורית עמק לוד
ישוב	
תאריך	13/09/15

שם הנספח	קנ"מ
תכי פרוקים מערכות קיימות בתחום מ.ח.150	1:500
תרשים סביבה	1:100,000

שמות וחתימות:

עורך התוכנית	שם: שלמה גלבר תאגיד: חלל"א חברה לעבודות הנדסה אזרחית (1985) בע"מ	חתימה:

T:\6822 HANYON SHPIRIM-B\IZIK\TNU-LAHV-2014\T-MARAHOT-PERUKIM-04.dwg, IDFrame, 06/10/2015 11:03:43,
DWG To PDF.pc3