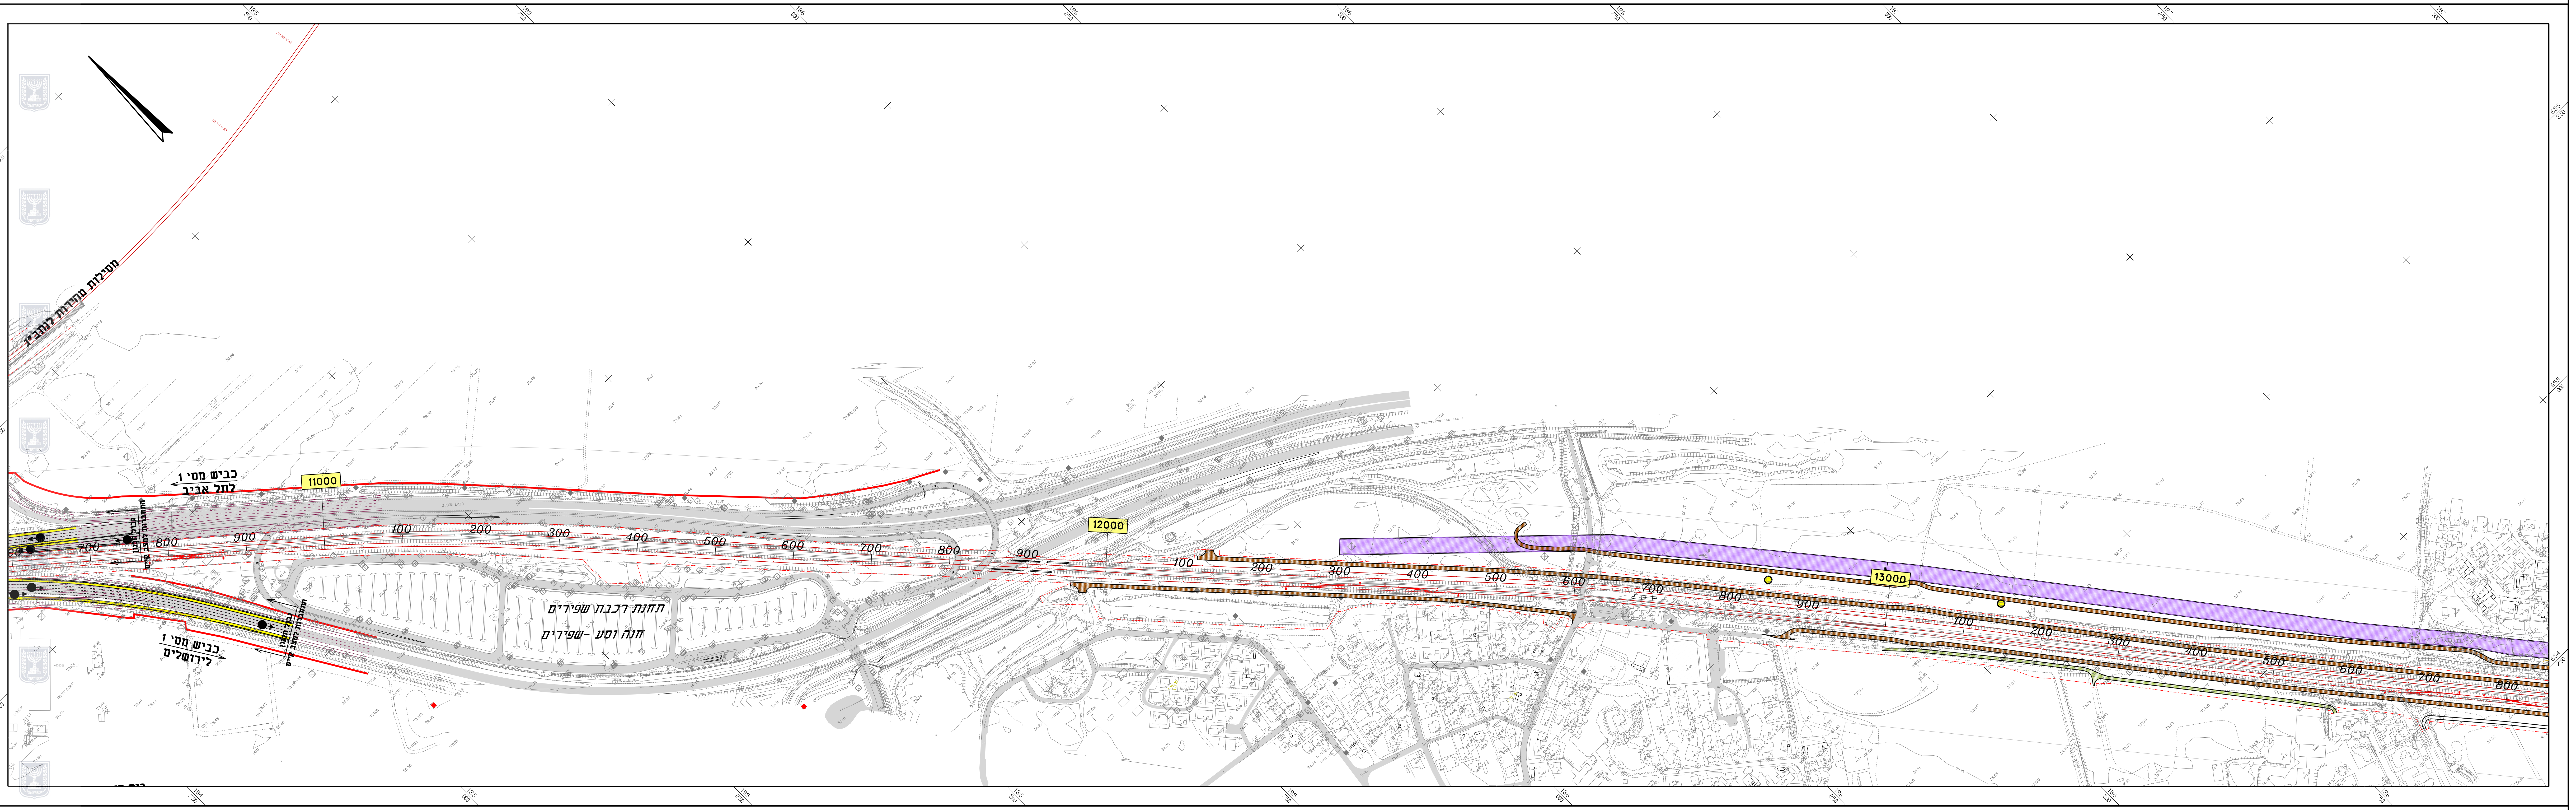

## תכנון מחלף חב"ד
## במסגרת ת.מ.א. 4\2\א\2

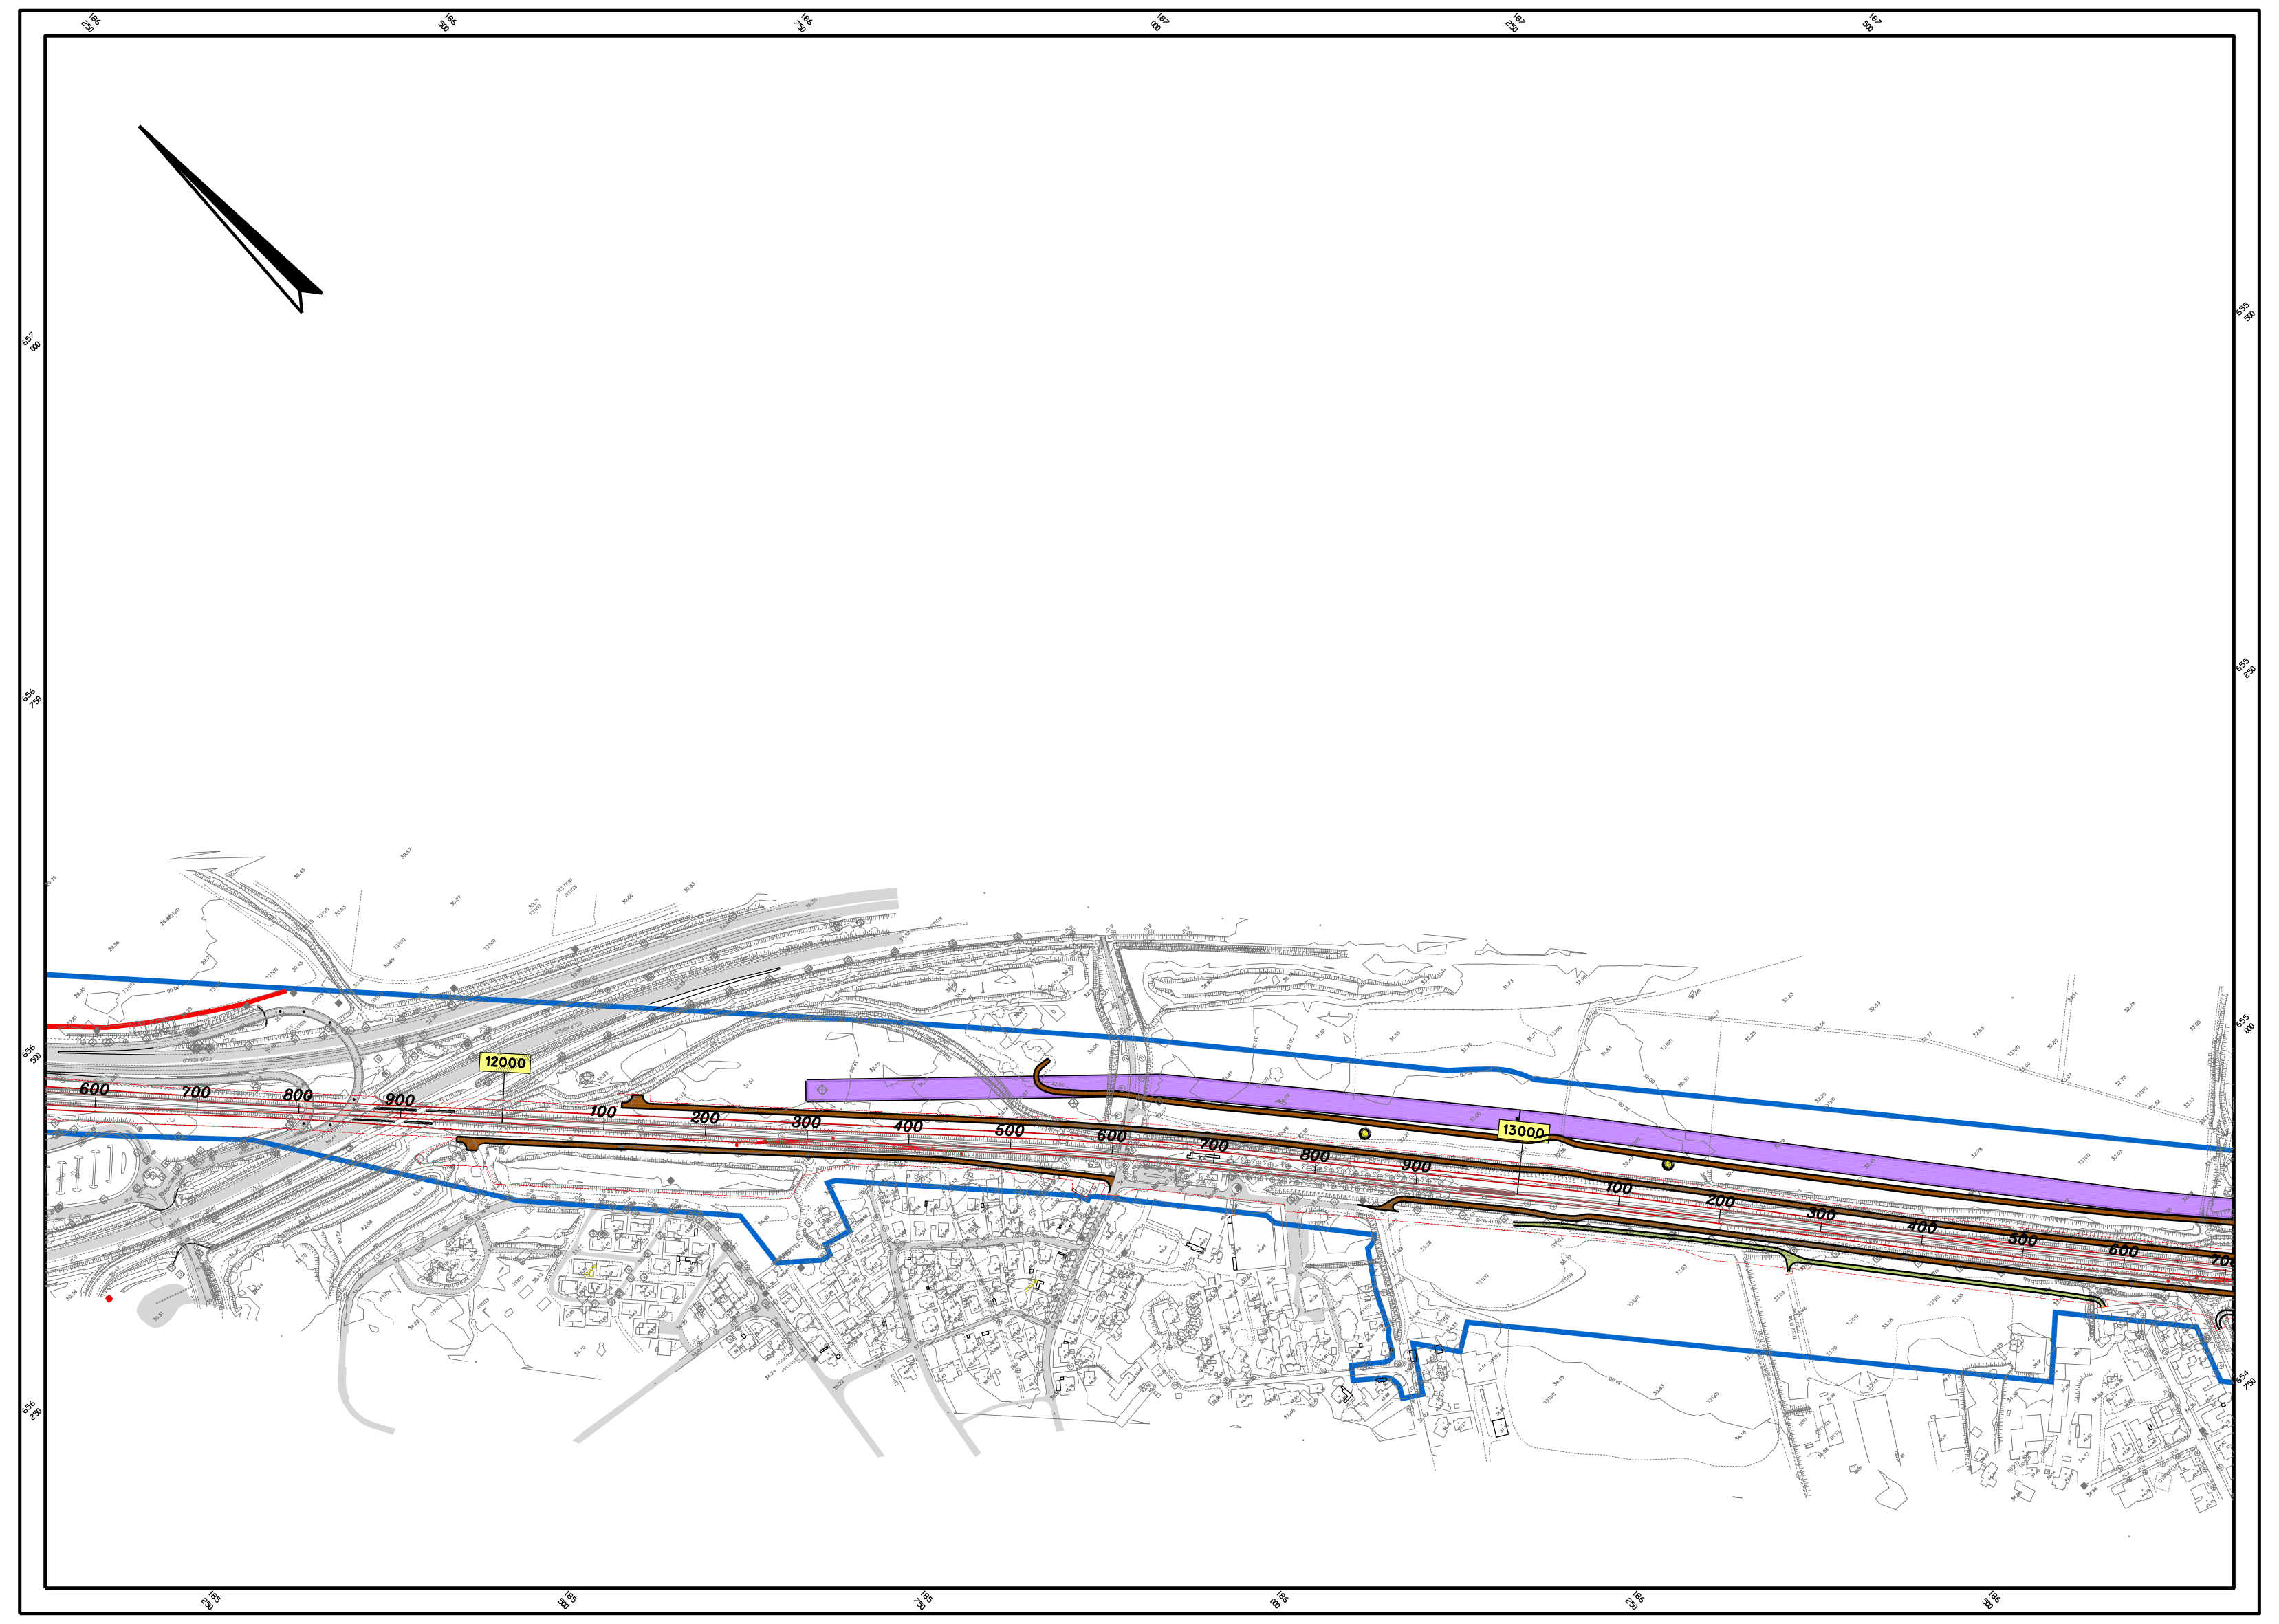

### תרשים סביבה :
קנ"מ 1 : 100,000

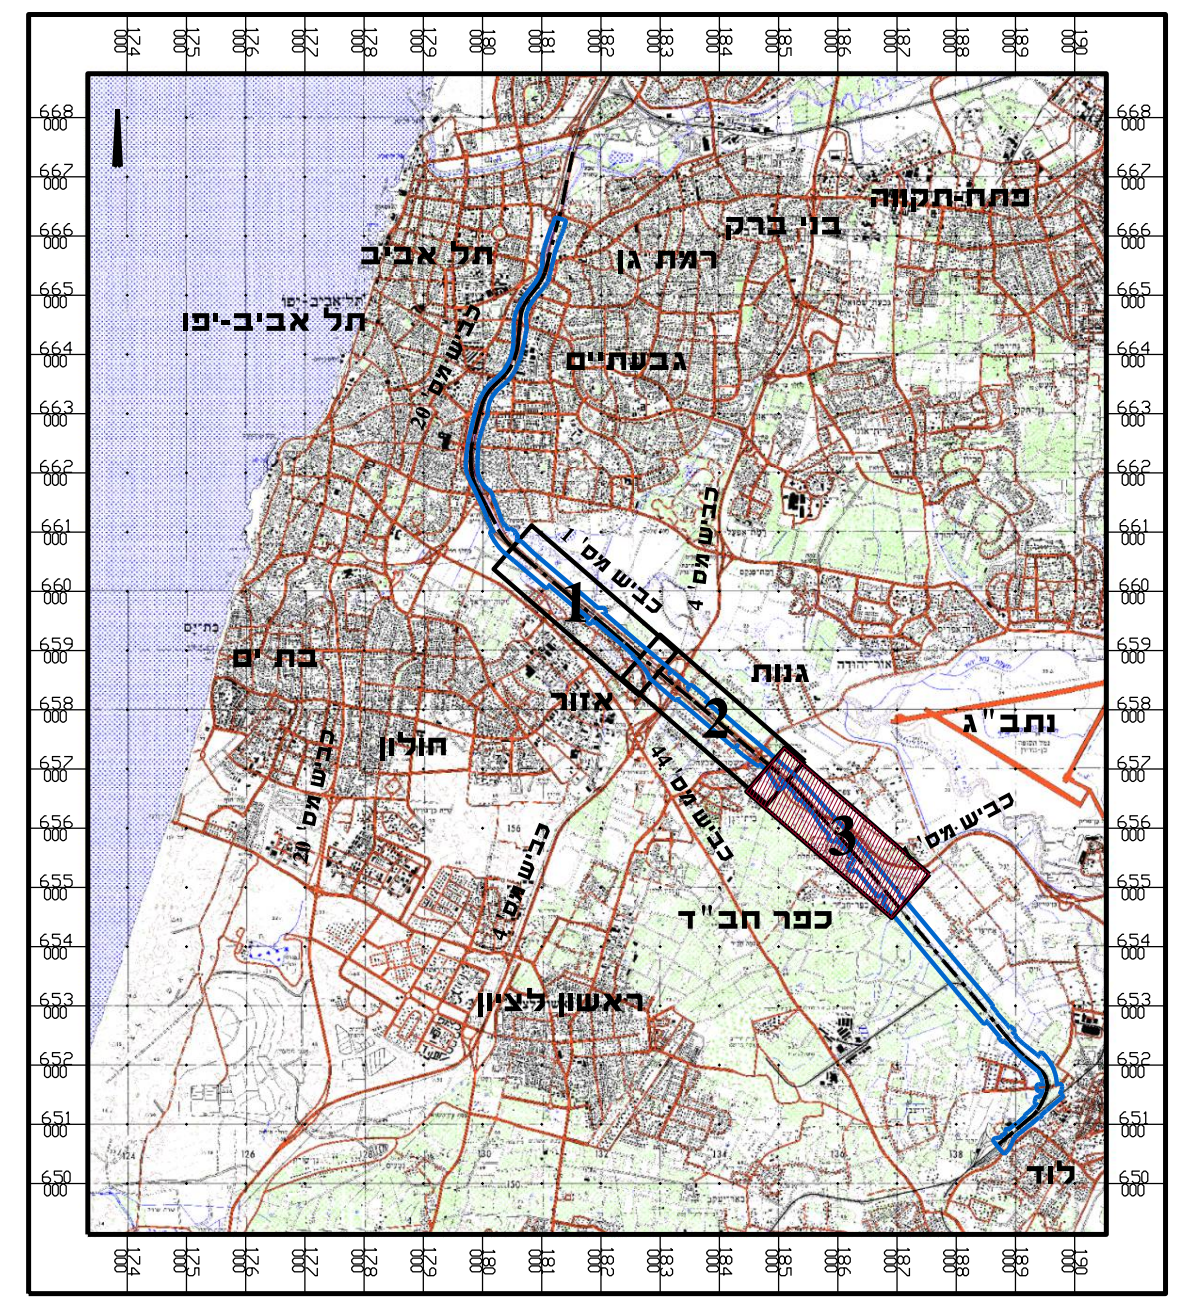

### מפת מפתח :
קנ"מ 1 : 100,000

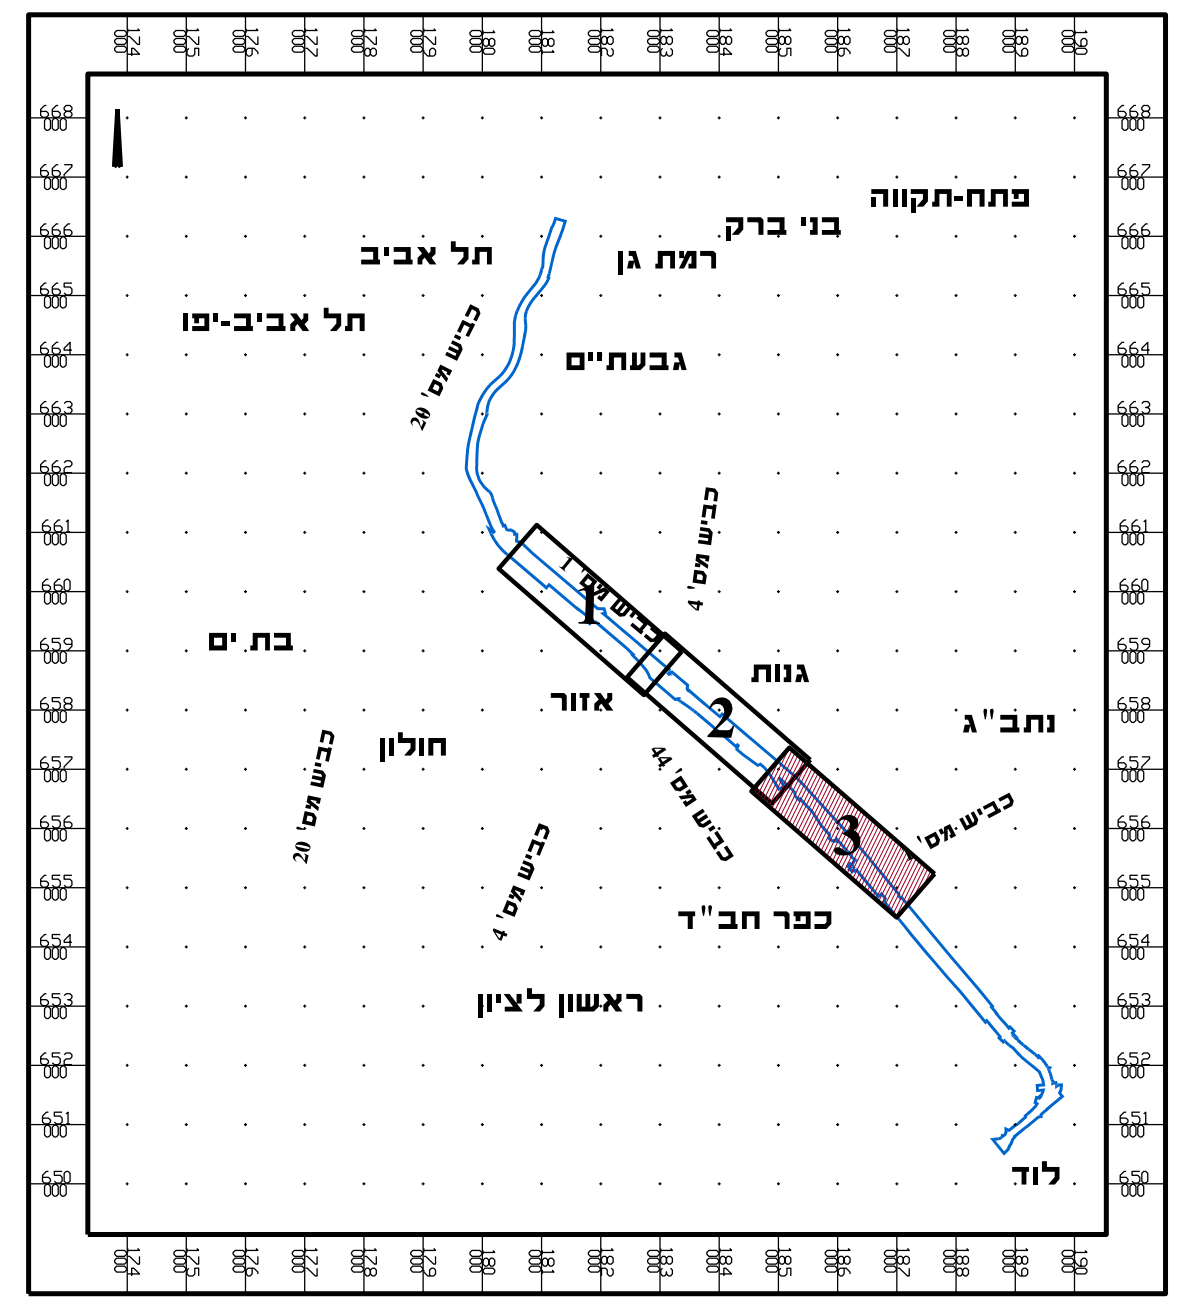

### מקרא:

| | |
|---|---|
| ▬ | גבול תת״ל 33 |
| ▬ | גבול זכות הדרך |
| ┈ | גבול זכות נחל מתוכנן |
| ─ | ציר מסילה מתוכננת |
| ▨ | רציף מתוכנן |
| -·-·- | גבול רצועת רכבת |
| ▭ | מסעת כביש קיימת |
| ▨ | דרך שירות מתוכננת |
| ▨ | דרך חקלאית מתוכננת |
| ▬ | שול אספלט מתוכנן |
| -□-□-□- | מעקה בטון מתוכנן |
| -○-○-○- | מעקה מתוכנן |
| ≡ | תכנון על ידי האחרים |
| ● ● | עמודי חשמל להעתקה |
| ▭ | רצועה מתוכננת לאיגודן מיקום מערכות משוער |
| ▨ | רצועה מתוכננת לחיח |

חוק התכנון והבנייה, התשכ"ה- 1965
הועדה הארצית לתכנון ולבניה של תשתיות לאומיות

# תת״ל 33

## מסילה רביעית באיילון
קטע ת״א מרכז-לוד

תכנית לתשתית לאומית

## נספח תנועה-כביש מס׳1

גליון מס׳ 2 מתוך 2
קנ״מ : 1 : 2,500

מחוז: תל אביב,מרכז

מרחבי תכנון מקומיים:
- ועדה מקומית תל אביב-יפו
- ועדה מקומית רמת גן
- ועדה מקומית גבעתיים
- מרחב תכנון מחוזי-מקומי (מחוז ת״א)
- ועדה מרחבית אור יהודה-אזור
- ועדה מרחבית מצפה אפק
- ועדה מקומית עמק לוד
- ועדה מקומית לוד

חותמת מוסד התכנון :

שלב: אישור תכנית מהדורה: 06 תאריך: 25.04.2018

מדינת ישראל
משרד האוצר
הועדה הארצית לתכנון ולבנייה
של תשתיות לאומיות
חתימה וחותמת

בעלי קרקע
**מדינת ישראל ואחרים**
חתימה וחותמת

יוזמי התכנית
נתיבי ישראל
החברה הלאומית לתשתיות תחבורה בע״מ
חתימה וחותמת

מנהל פרוייקט :
תהרדסים
ייזום פרוייקטים בע״מ
חתימה וחותמת

| שם: | תפקיד: | מס׳ ת״ז | כתובת: |
|---|---|---|---|
| איתי עובדיה | מנה״פ | 023518210 | רח. יגאל אלון 67 , תל אביב |
| **טלפון:** | **פקס:** | **דוא״ל:** | **שם:** |
| 03-6251222 | 03-6251223 | itay@yahel-eng.co.il | |

עורך התוכנית
ינון תכנון יעוץ ומחקר בע״מ
הנדסה אזרחית, דרכים, תנועה, מסילות ברזל, אדר׳ נוף ומבנים, הדמיות, קונסטרוקציות, מדידות וניהול פרויקטים
חתימה וחותמת

| שם: | תפקיד: | מס׳ ת״ז | כתובת: |
|---|---|---|---|
| אלכס לרנר | מתכנן | 308640283 | רח. היוזמה 4 , טירת הכרמל |
| **טלפון:** | **פקס:** | **דוא״ל:** | **שם:** |
| 04-8569000 | 04-8569010 | yenon@yenon.co.il | ינון-תכנון יעיץ ומחקר בע״מ |

מודד מוסמך
קבוצת דטהמפ DATAMAP GROUP
דטהמפ אגרומפ אוריומפ גטניר ושות׳
מערכות מידע גאוגרפיות בע״מ מיפוי וסקרים חקלאיים בע״מ מיפוי פוטוגרמטרי בע״מ מודדים מוסמכים בע״מ
רח׳ הירקון 67, בני-ברק 51206 טל.03-7541000 פקס.03-7516356
67 Hayarkon St. Bnei-Brak 51206 Tel.03-7541000 Fax.03-7516356
חתימה וחותמת

| שם: | מודד מוסמך | מס׳ ת״ז | כתובת: |
|---|---|---|---|
| ברנרד גטניו | 570 | 052602984 | רח. הירקון 67 , בני ברק |
| **טלפון:** | **פקס:** | **דוא״ל:** | **שם:** |
| 03-7541000 | 03-7516353 | info@datamap.com | |

הריני מצהיר בזאת כי מדידת המפה הטופוגרפית/המצבית המהווה רקע לתוכנית זו, נערכה על ידי ביום __________
והיא הוכנה לפי הוראות נוהל מבא״ת ובהתאם להוראות החוק ולתקנות המודדים שבתוקף.
דיוק הקו הכחול והקדסטר: מדידה גרפית/ קו כחול (בלבד) ברמה אנליטית/ מדידה אנליטית מלאה ברמת תצ״ר (כולל הקו הכחול)

שם המודד ______ מספר רישיון ______ חתימה ______ תאריך ______

30/04/2018 09:35:13 S:\2080\SHEET\PD-FA\SP\Nispah_Tnua.dgn