חוק התכנון והבנייה, התשכ"ה- 1965
הועדה הארצית לתכנון ולבניה של תשתיות לאומיות

תת״ל 33

מסילה רביעית באיילון
קטע ת״א מרכז-לוד

תכנית לתשתית לאומית

תאום תשתיות

גליון מס׳ 4 (מקטעים 7-8) מתוך 4
קנ״מ : 2,500 : 1

מחוז: תל אביב,מרכז

מרחבי תכנון מקומיים:
- ועדה מקומית תל אביב-יפו
- ועדה מקומית רמת גן
- ועדה מקומית גבעתיים
- מרחב תכנון מחוזי-מקומי (מחוז ת״א)
- ועדה מרחבית אור יהודה-אזור
- ועדה מרחבית מצפה אפק
- ועדה מקומית עמק לוד
- ועדה מקומית לוד

חותמת מוסד התכנון :

שלב: אישור תכנית   מהדורה: 15   תאריך: 25.04.2018

תרשים סביבה :
קנ״מ 1 : 100,000

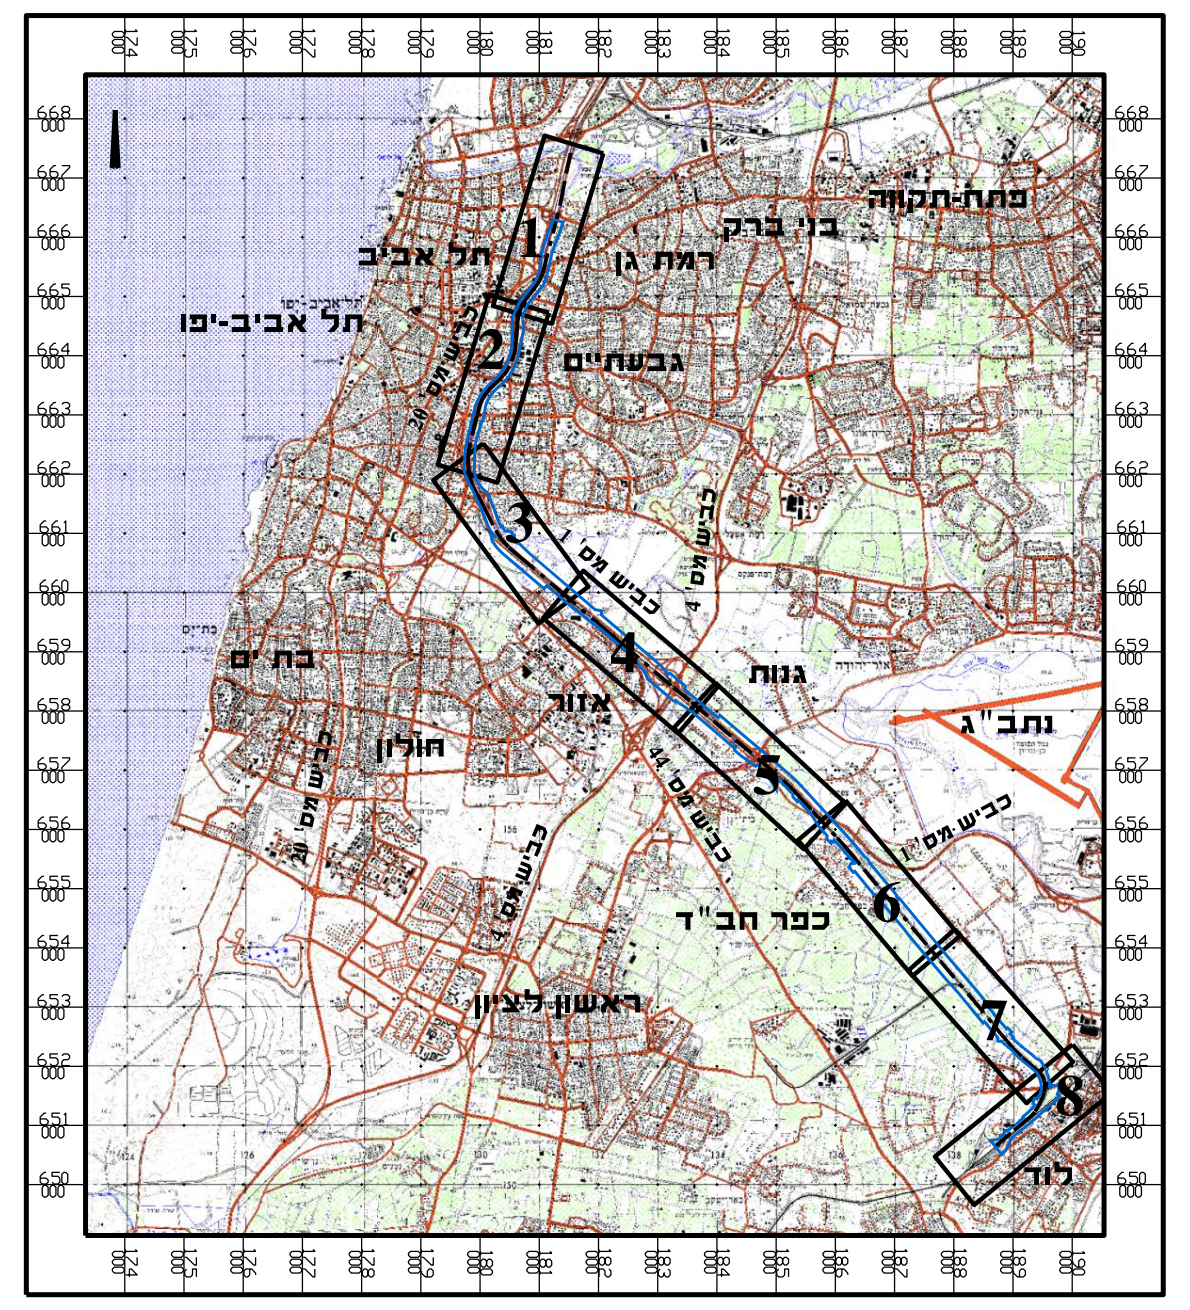

מפת מפתח :
קנ״מ 1 : 100,000

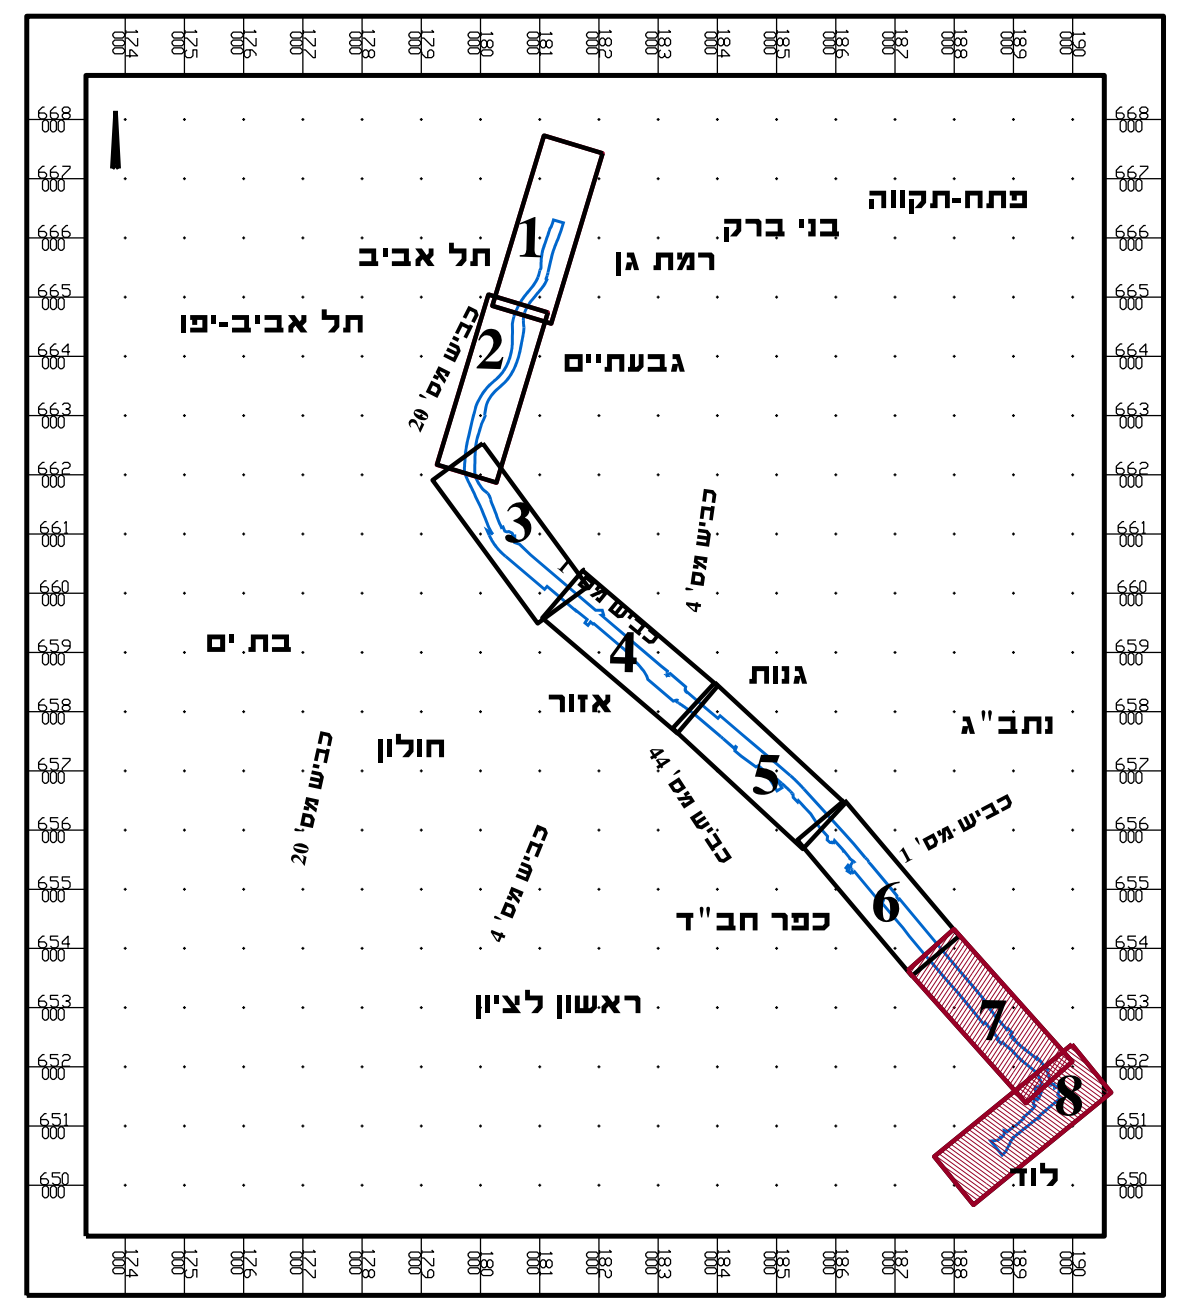

מקרא :

גבול תכנית תת״ל 33	━
שטח רצועת רכבת מוצע	▭
צירי מסילות רכבת	─
רציף	▬
מס׳ חתך/ק״מ	104000
דרך שרות מתוכננת	▨
גבול גוש	▲
מס׳ גוש	6974
תשתיות:	
אתר ארכאולוגי	[‒ ‒ ‒]
קו מתח עליון עילי קיים	─ ─
קו מתח עליון עילי לביטול	─✕─
עמודי חשמל קיימים לביטול	✕ ✕ ✕ ✕
עמודי חשמל להעתקה	⊗ ⊗ ⊗
קו מתח גבוה עילי קיים	─ ─
קו מתח גבוה תת קרקעי קיים	‒ ‒ ‒ ‒
קו מתח נמוך תת קרקעי קיים	‒ ‒ ‒ ‒
קו דלק קיים	─K─M─D─
קו תאורה תת קרקעי קיים	───
קו ביוב א.ע.ד.ן קיים	▬ ▬ ▬
קו סניקה א.ע.ד.ן קיים	‒ ‒ ‒ ‒
קו גז קיים	─G-A-Z─
קו בזק קיים	─B─B─
קוי הוט קיים	─HOT─HOT─
קו סלקום קיים	─CEL─CEL─
קו פרטנר קיים	─PAR─PAR─
קו מקורות קיים	▬ ▬ ▬
קו מי קולחין קיים	‒ ‒ ‒ ‒
קו ניקוז קיים	‒ ‒ ‒ ‒
מובל ניקוז קיים	═ ═ ═
מנהרת חשמל מ״ג	▨
קו ביוב מתוכנן	─S─S─
קו מתח עליון עילי מוצע	─SHV─SHV─
עמוד חשמל מוצע	☒
קו סניקה מתוכנן	─SF─SF─
קו מקורות מתוכנן	─MK─MK─
סימון חציות רכבת	▧
רצועה מתוכננת לאיגודן מיקום מערכות משוער	🟨
רצועה מתוכננת לחח״י	🟪
תכנון על ידי האחרים	═

מדינת ישראל משרד האוצר הועדה הארצית לתכנון ולבנייה של תשתיות לאומיות	חתימה וחותמת			
בעלי קרקע **מדינת ישראל ואחרים**	חתימה וחותמת			
יוזמי התכנית נתיבי ישראל החברה הלאומית לתשתיות תחבורה בע"מ	חתימה וחותמת			
מנהל פרוייקט :	חתימה וחותמת			
	שם: איתי עובדיה	תפקיד: מנה״פ	מס׳ ת״ז 023518210	כתובת: רח. יגאל אלון , 67 , תל אביב
	טלפון: 03-6251222	פקס: 03-6251223	דוא״ל: itay@yahel-eng.co.il	שם:
עורך התוכנית ינון תכנון יעוץ ומחקר בע״מ	חתימה וחותמת			
	שם: אלכס לרנר	תפקיד: מתכנן	מס׳ ת״ז 308640283	כתובת: רח. היוזמה 4 , טירת הכרמל
	טלפון: 04-8569000	פקס: 04-8569010	דוא״ל: yenon@yenon.co.il	שם: ינון-תכנון יעיץ ומחקר בע״מ
מודד מוסמך קבוצת דטהמפ DATAMAP GROUP	חתימה וחותמת			
	שם: ברנרד גטניו	מודד מוסמך 570	מס׳ ת״ז 052602984	כתובת: רח. הירקון , 67 , בני ברק
	טלפון: 03-7541000	פקס: 03-7516353	דוא״ל: info@datamap.com	שם:

הריני מצהיר בזאת כי מדידת המפה הטופוגרפית/המצבית המהווה רקע לתוכנית זו, נערכה על ידי ביום __________
והיא הוכנה לפי הוראות נוהל מבא"ת ובהתאם להוראות החוק ולתקנות המודדים שבתוקף.
דיוק הקו הכחול והקדסטר: מדידה גרפית/ קו כחול (בלבד) ברמה אנליטית/ מדידה אנליטית מלאה ברמת תצ״ר (כולל הקו הכחול)

שם המודד ____________   מספר רישיון ____________   חתימה ____________   תאריך ____________

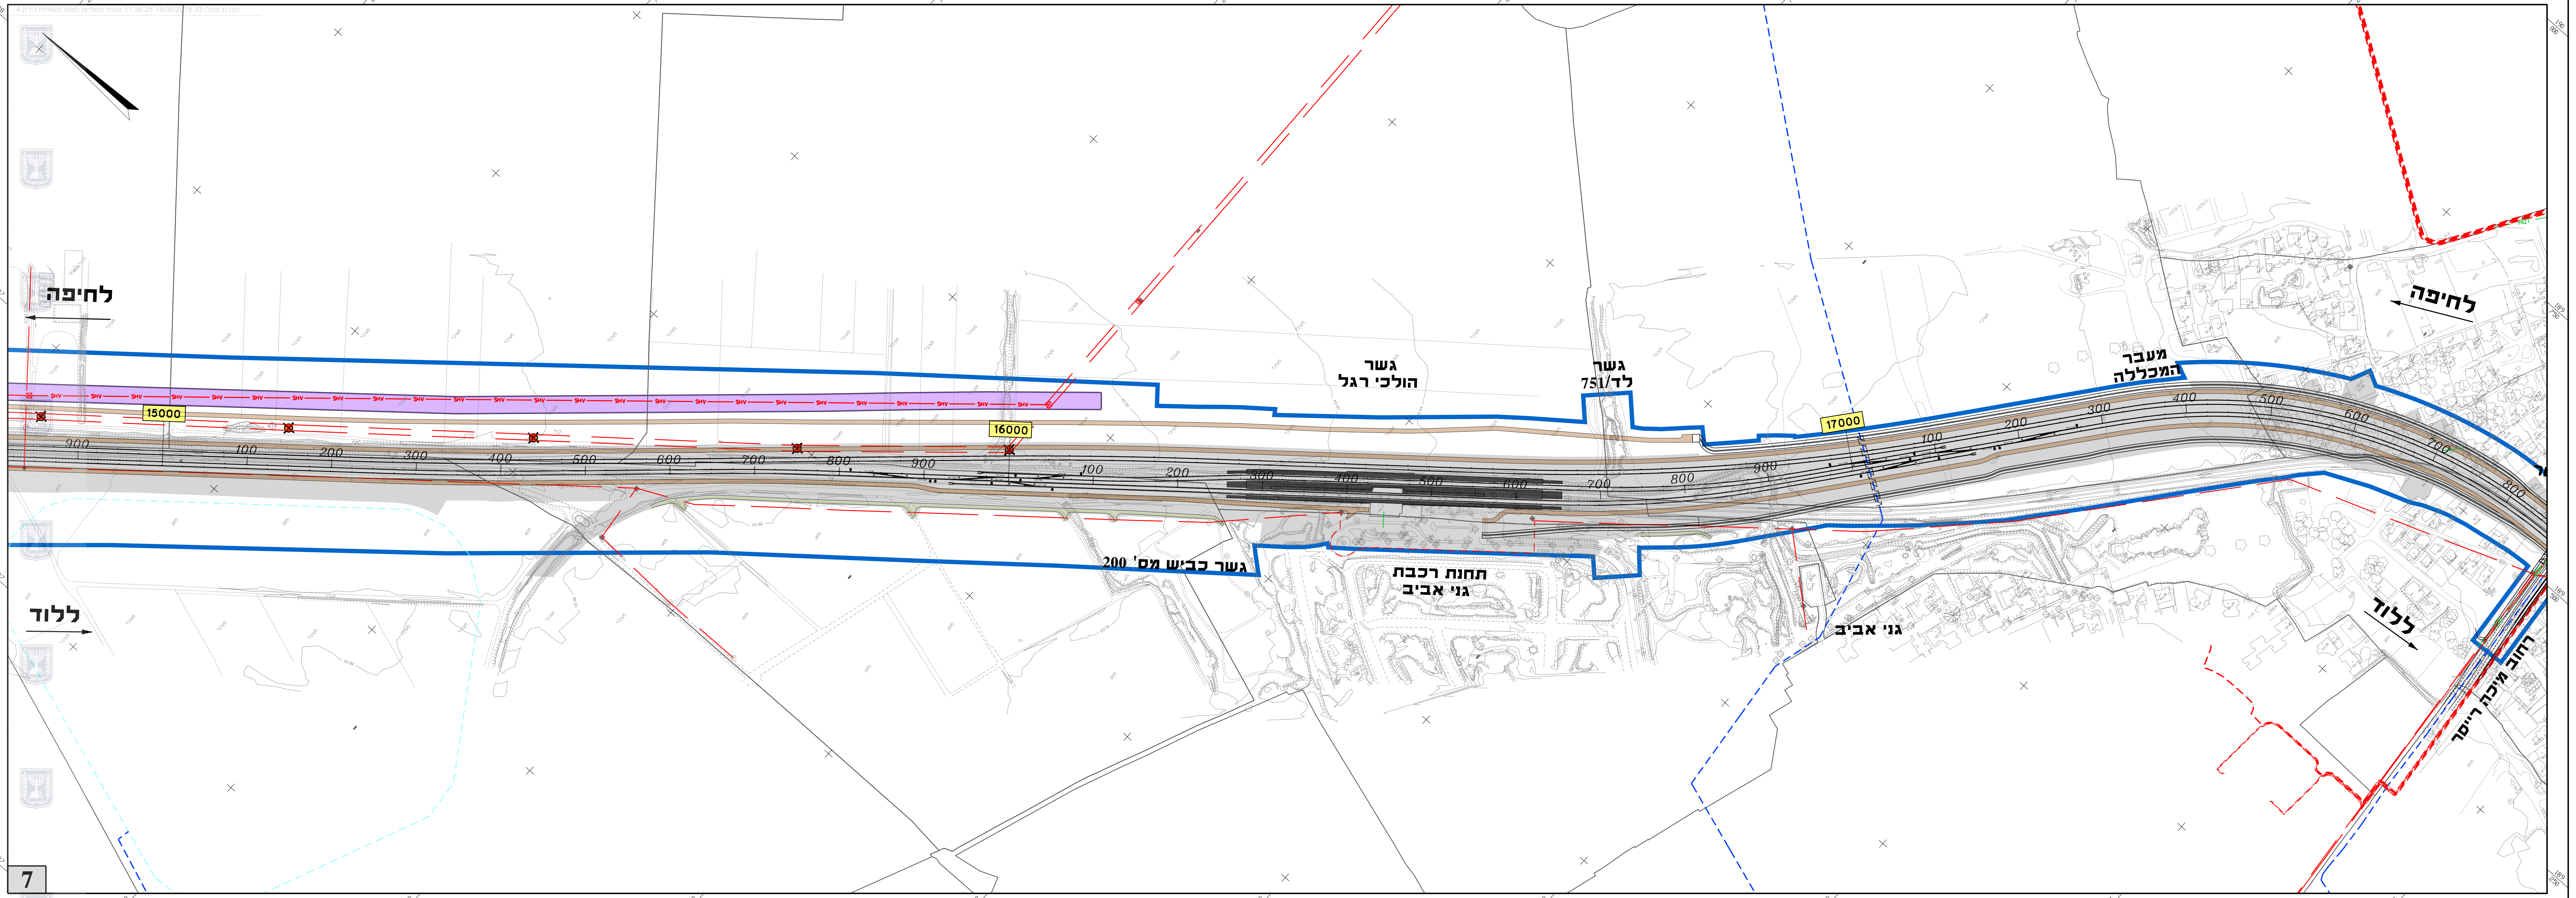

7

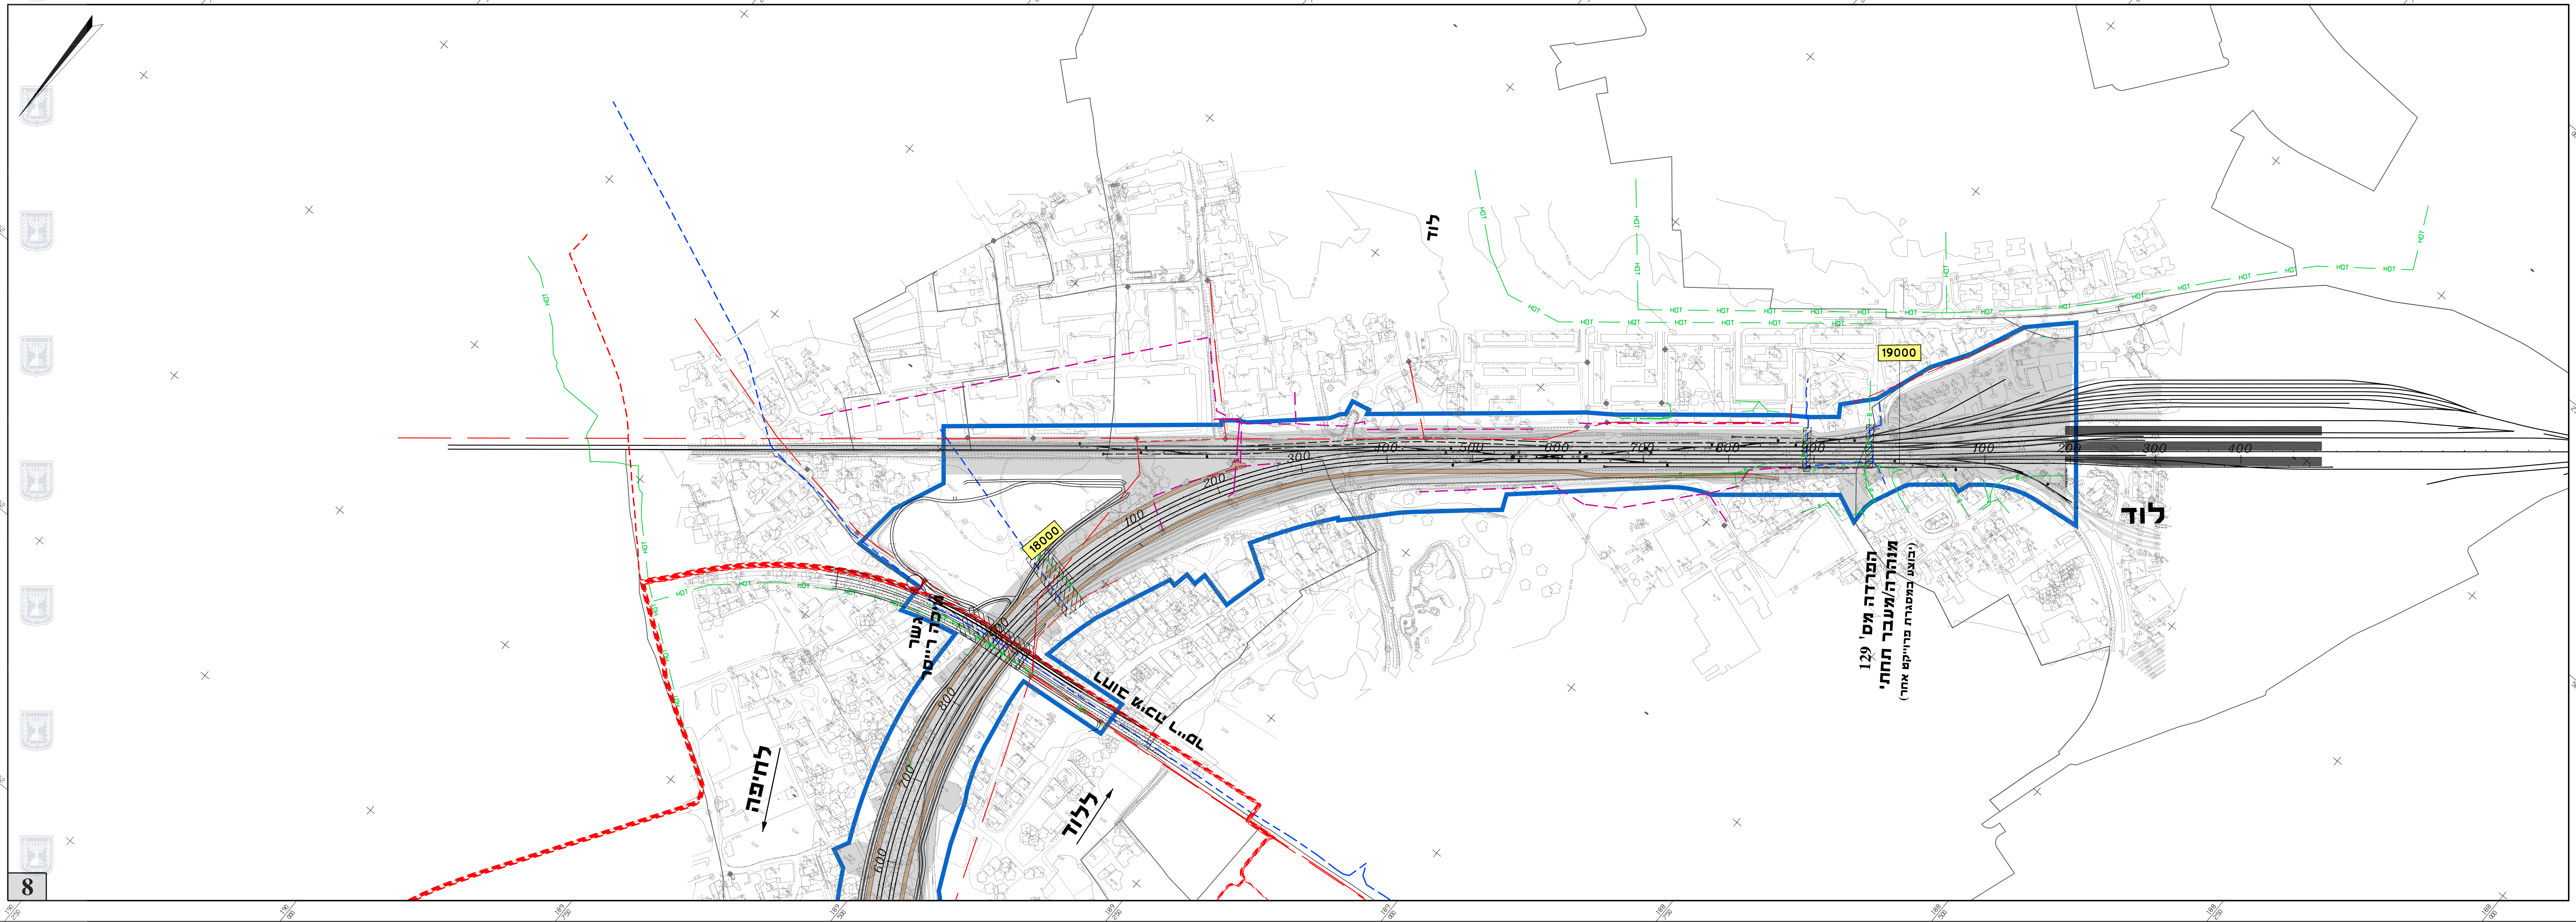

8

4-tash-7_8 25/04/2018 14:09:44 alinag S:\2080\SHEET\PD-FA\SP\Teum_Tashtiot_2080.dgn