רמפה מס' 1

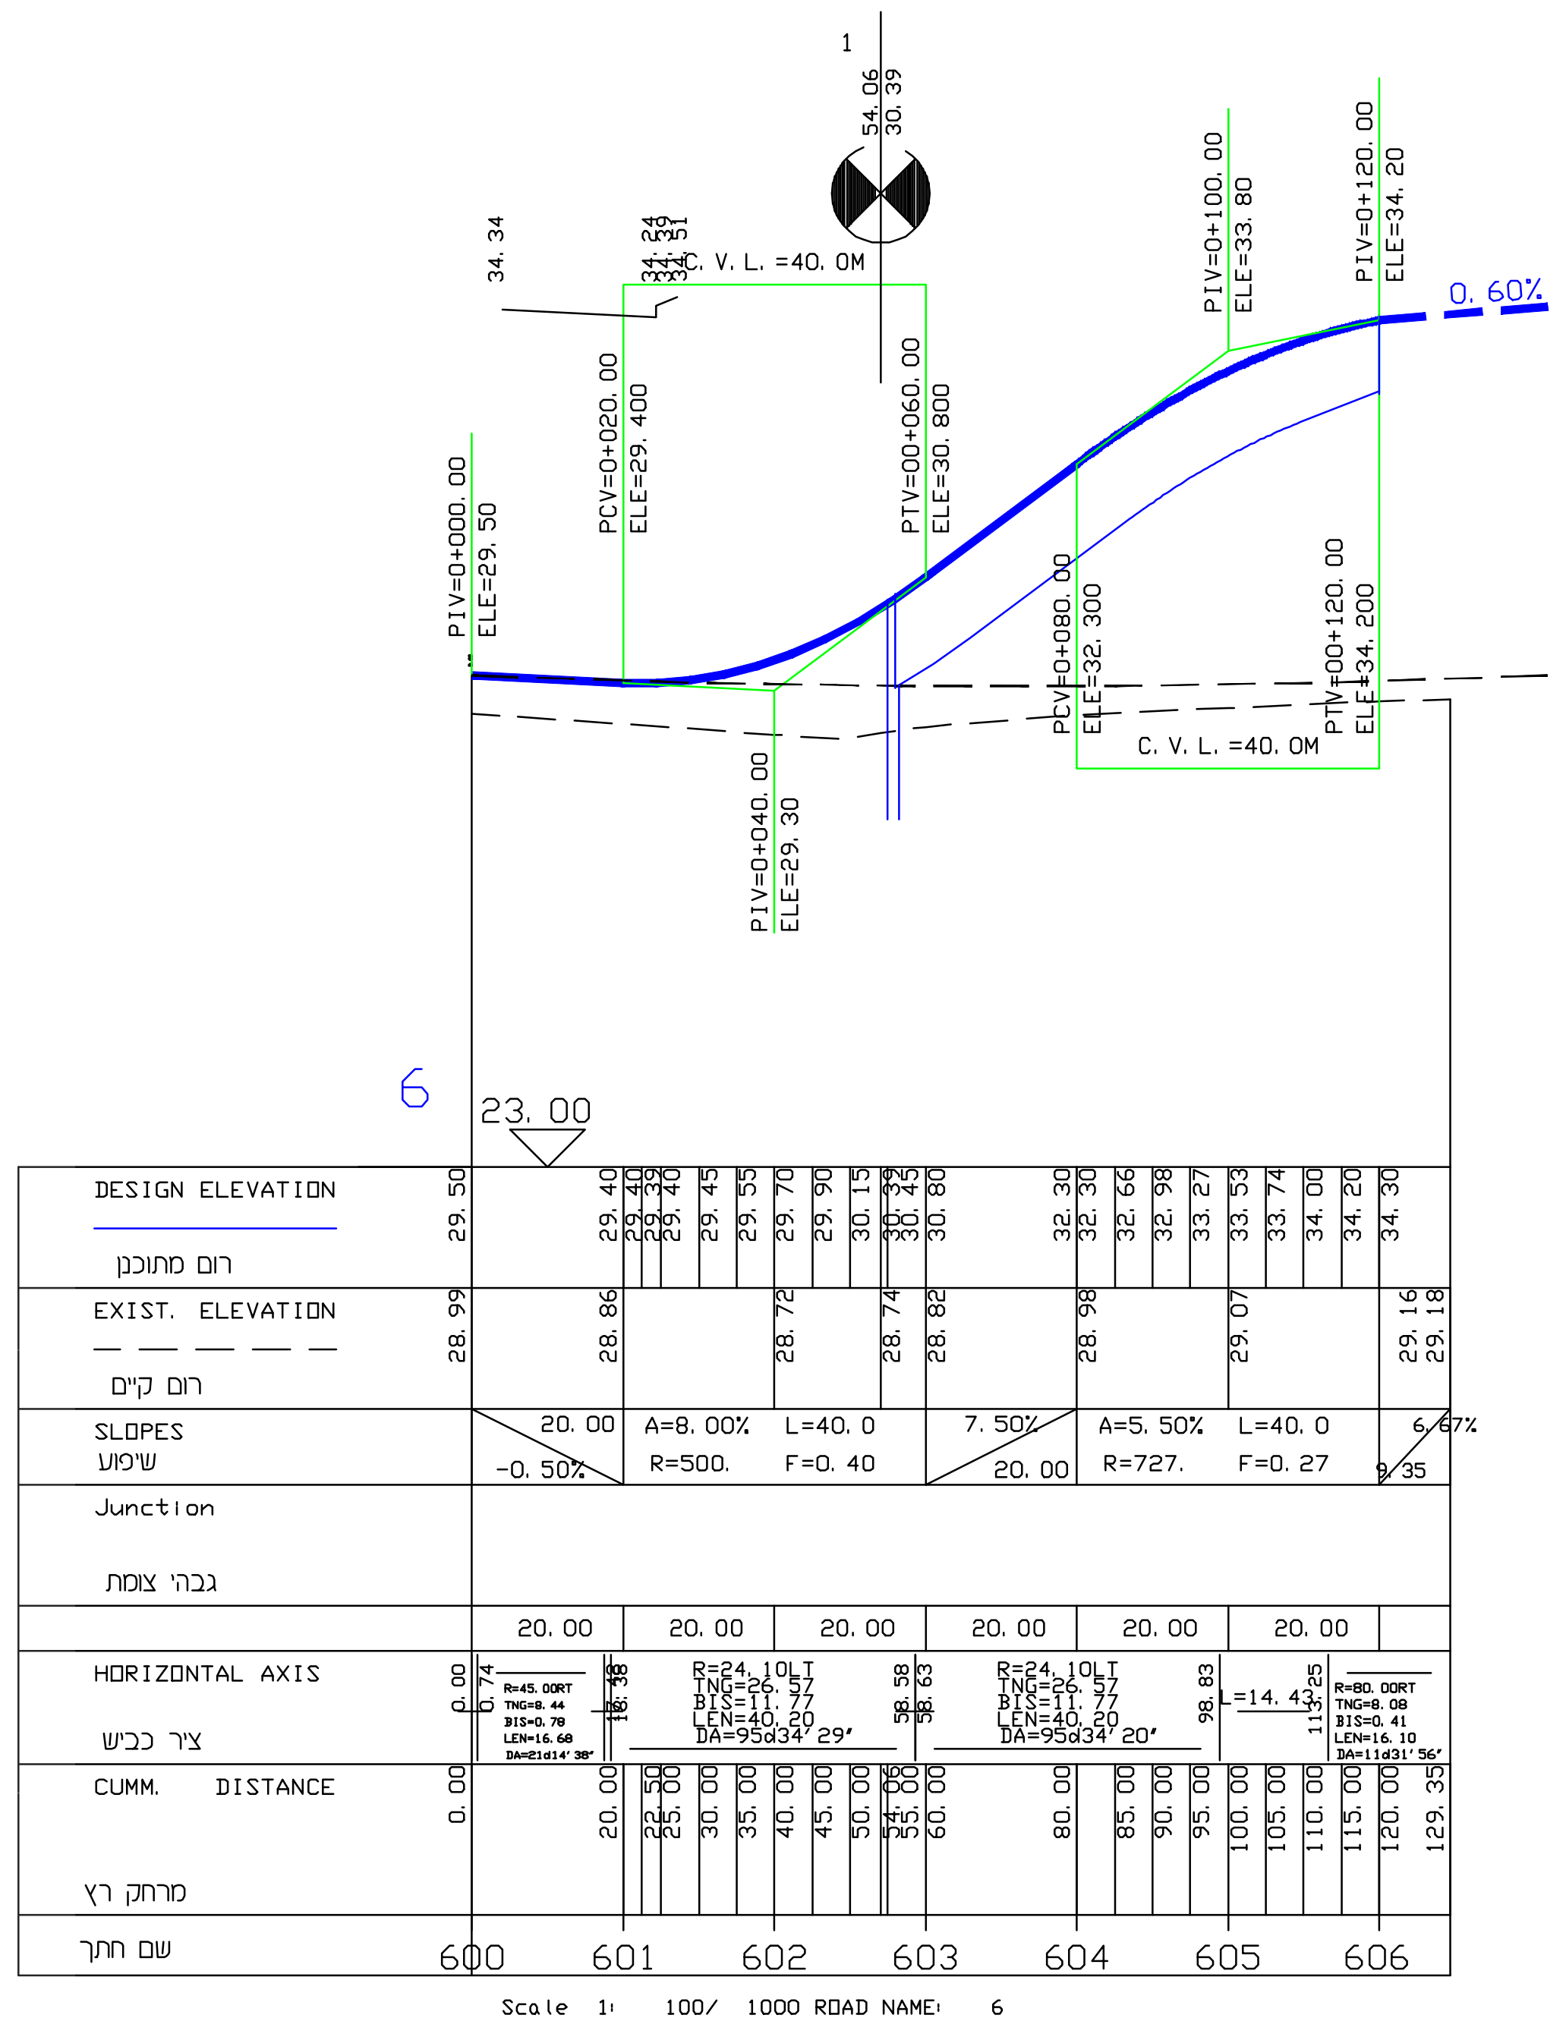

רמפה מס' 2

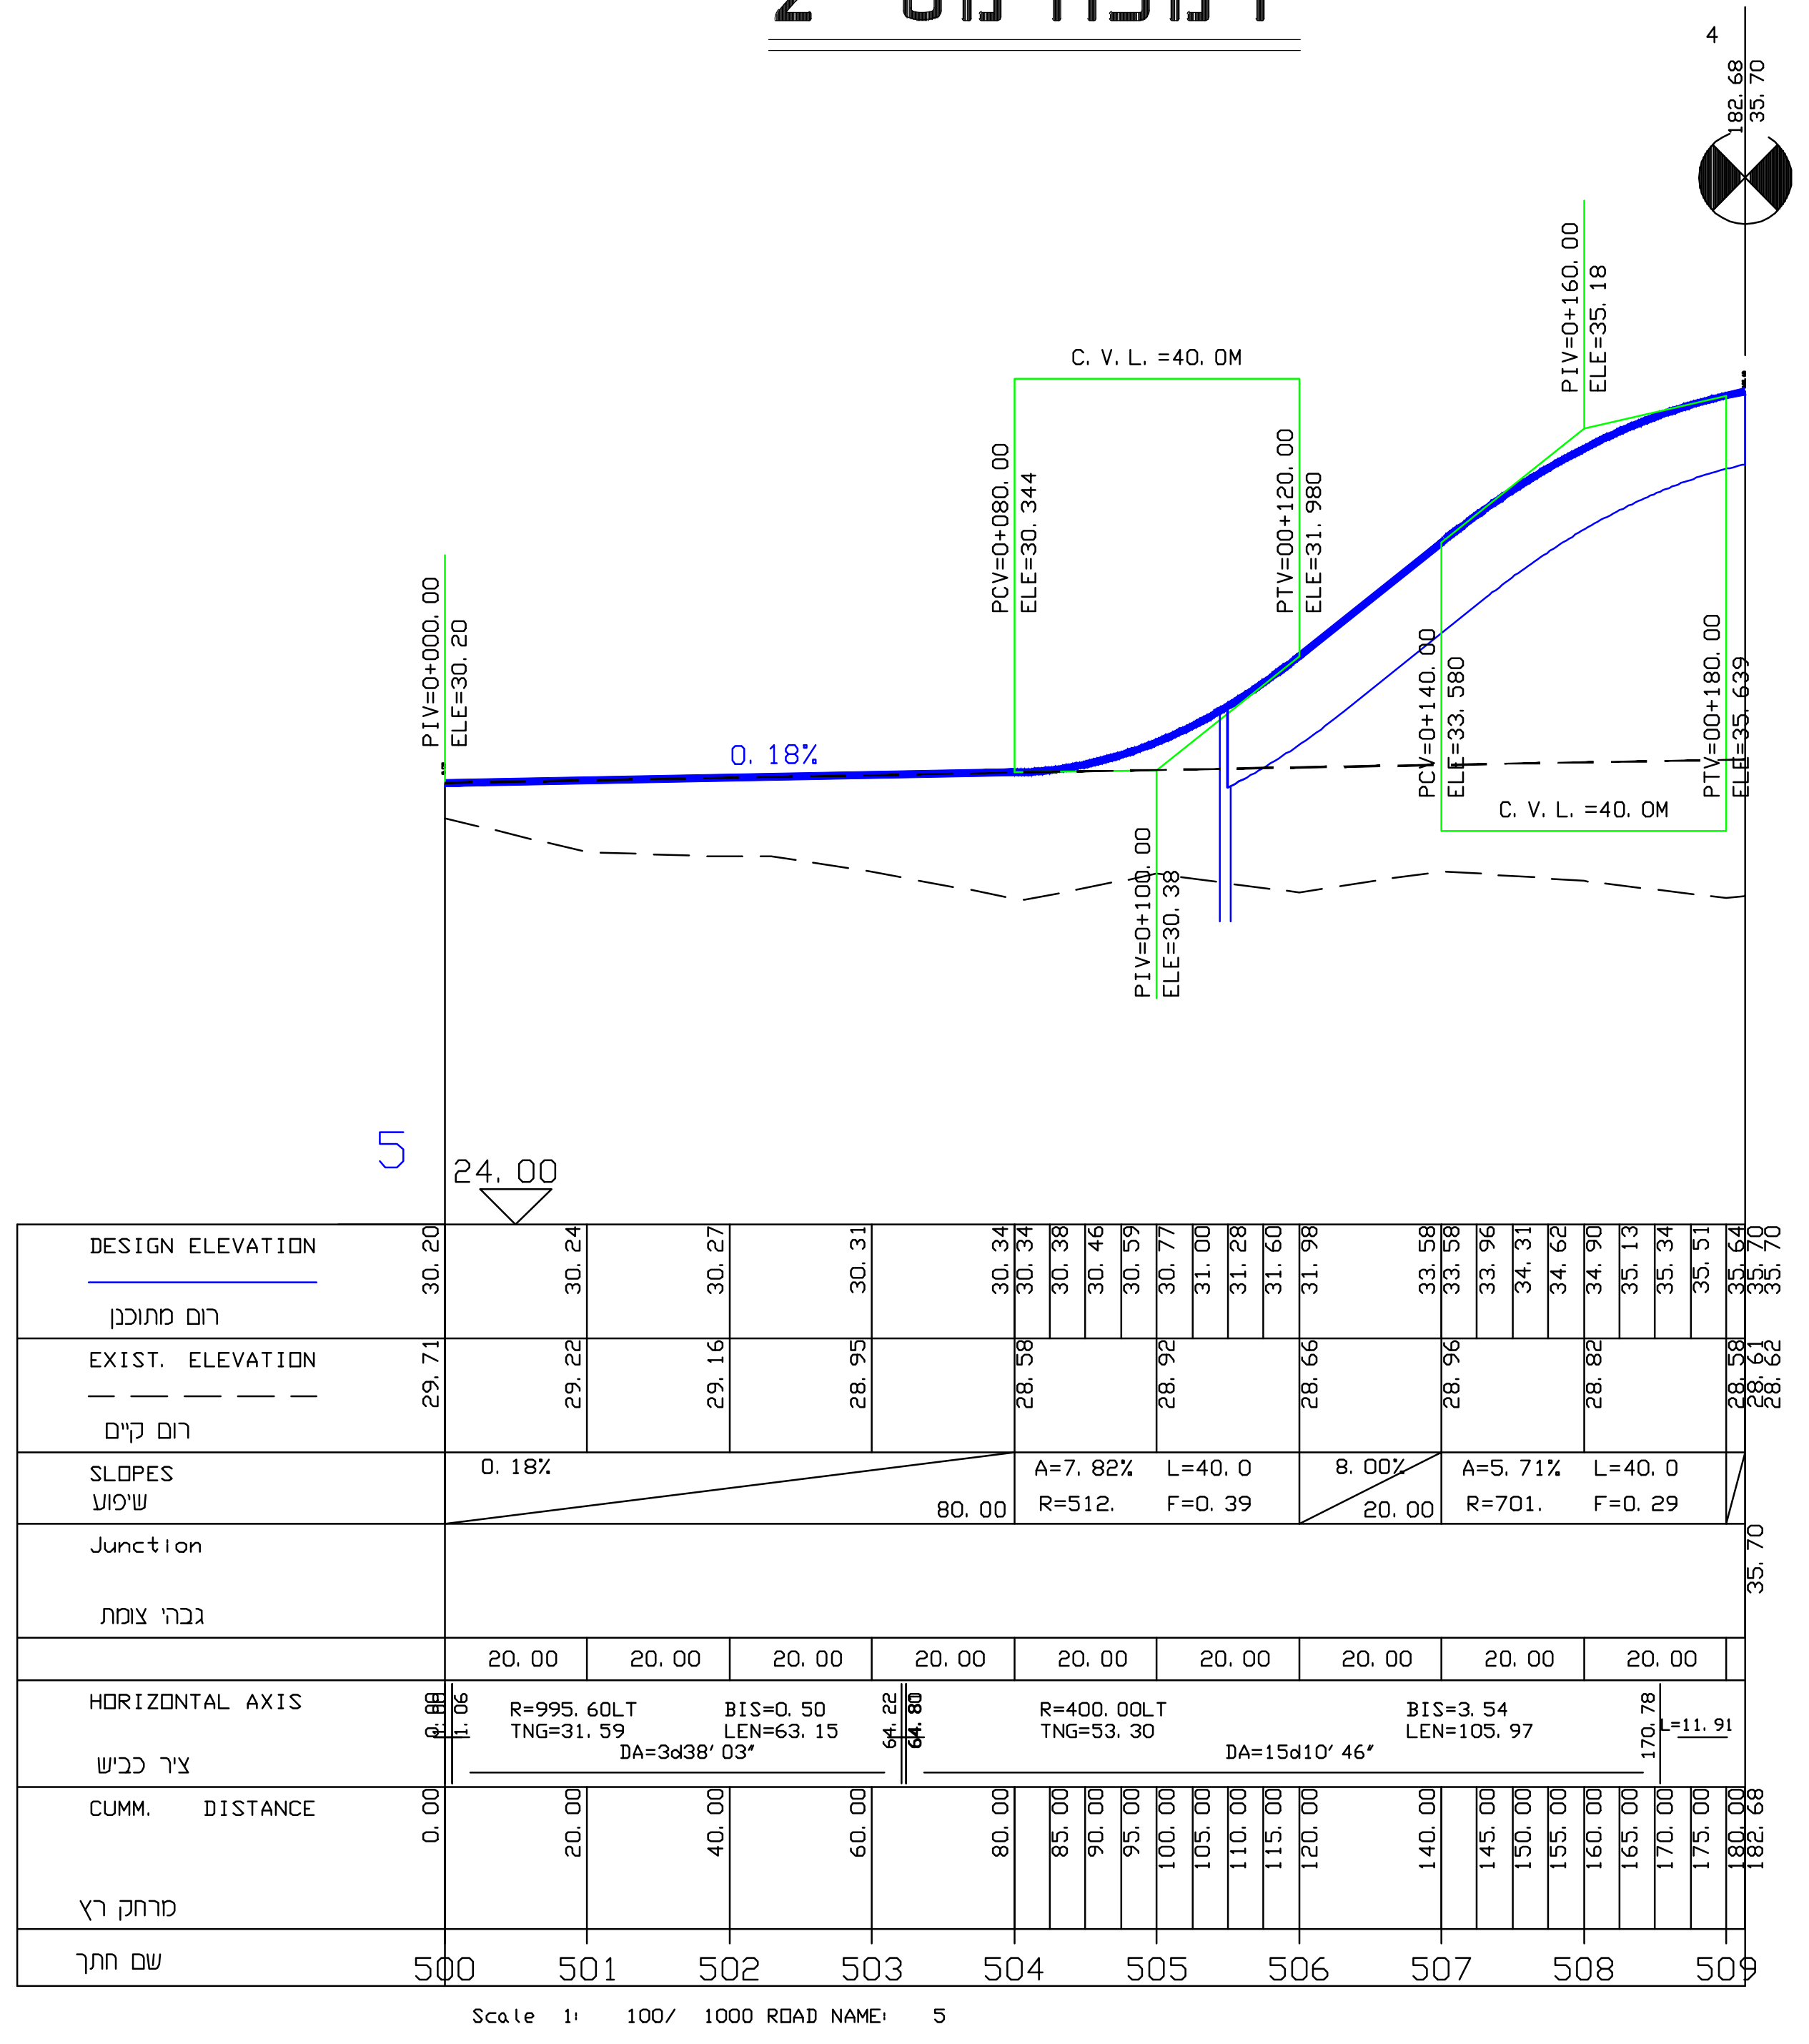

רמפה מס' 3

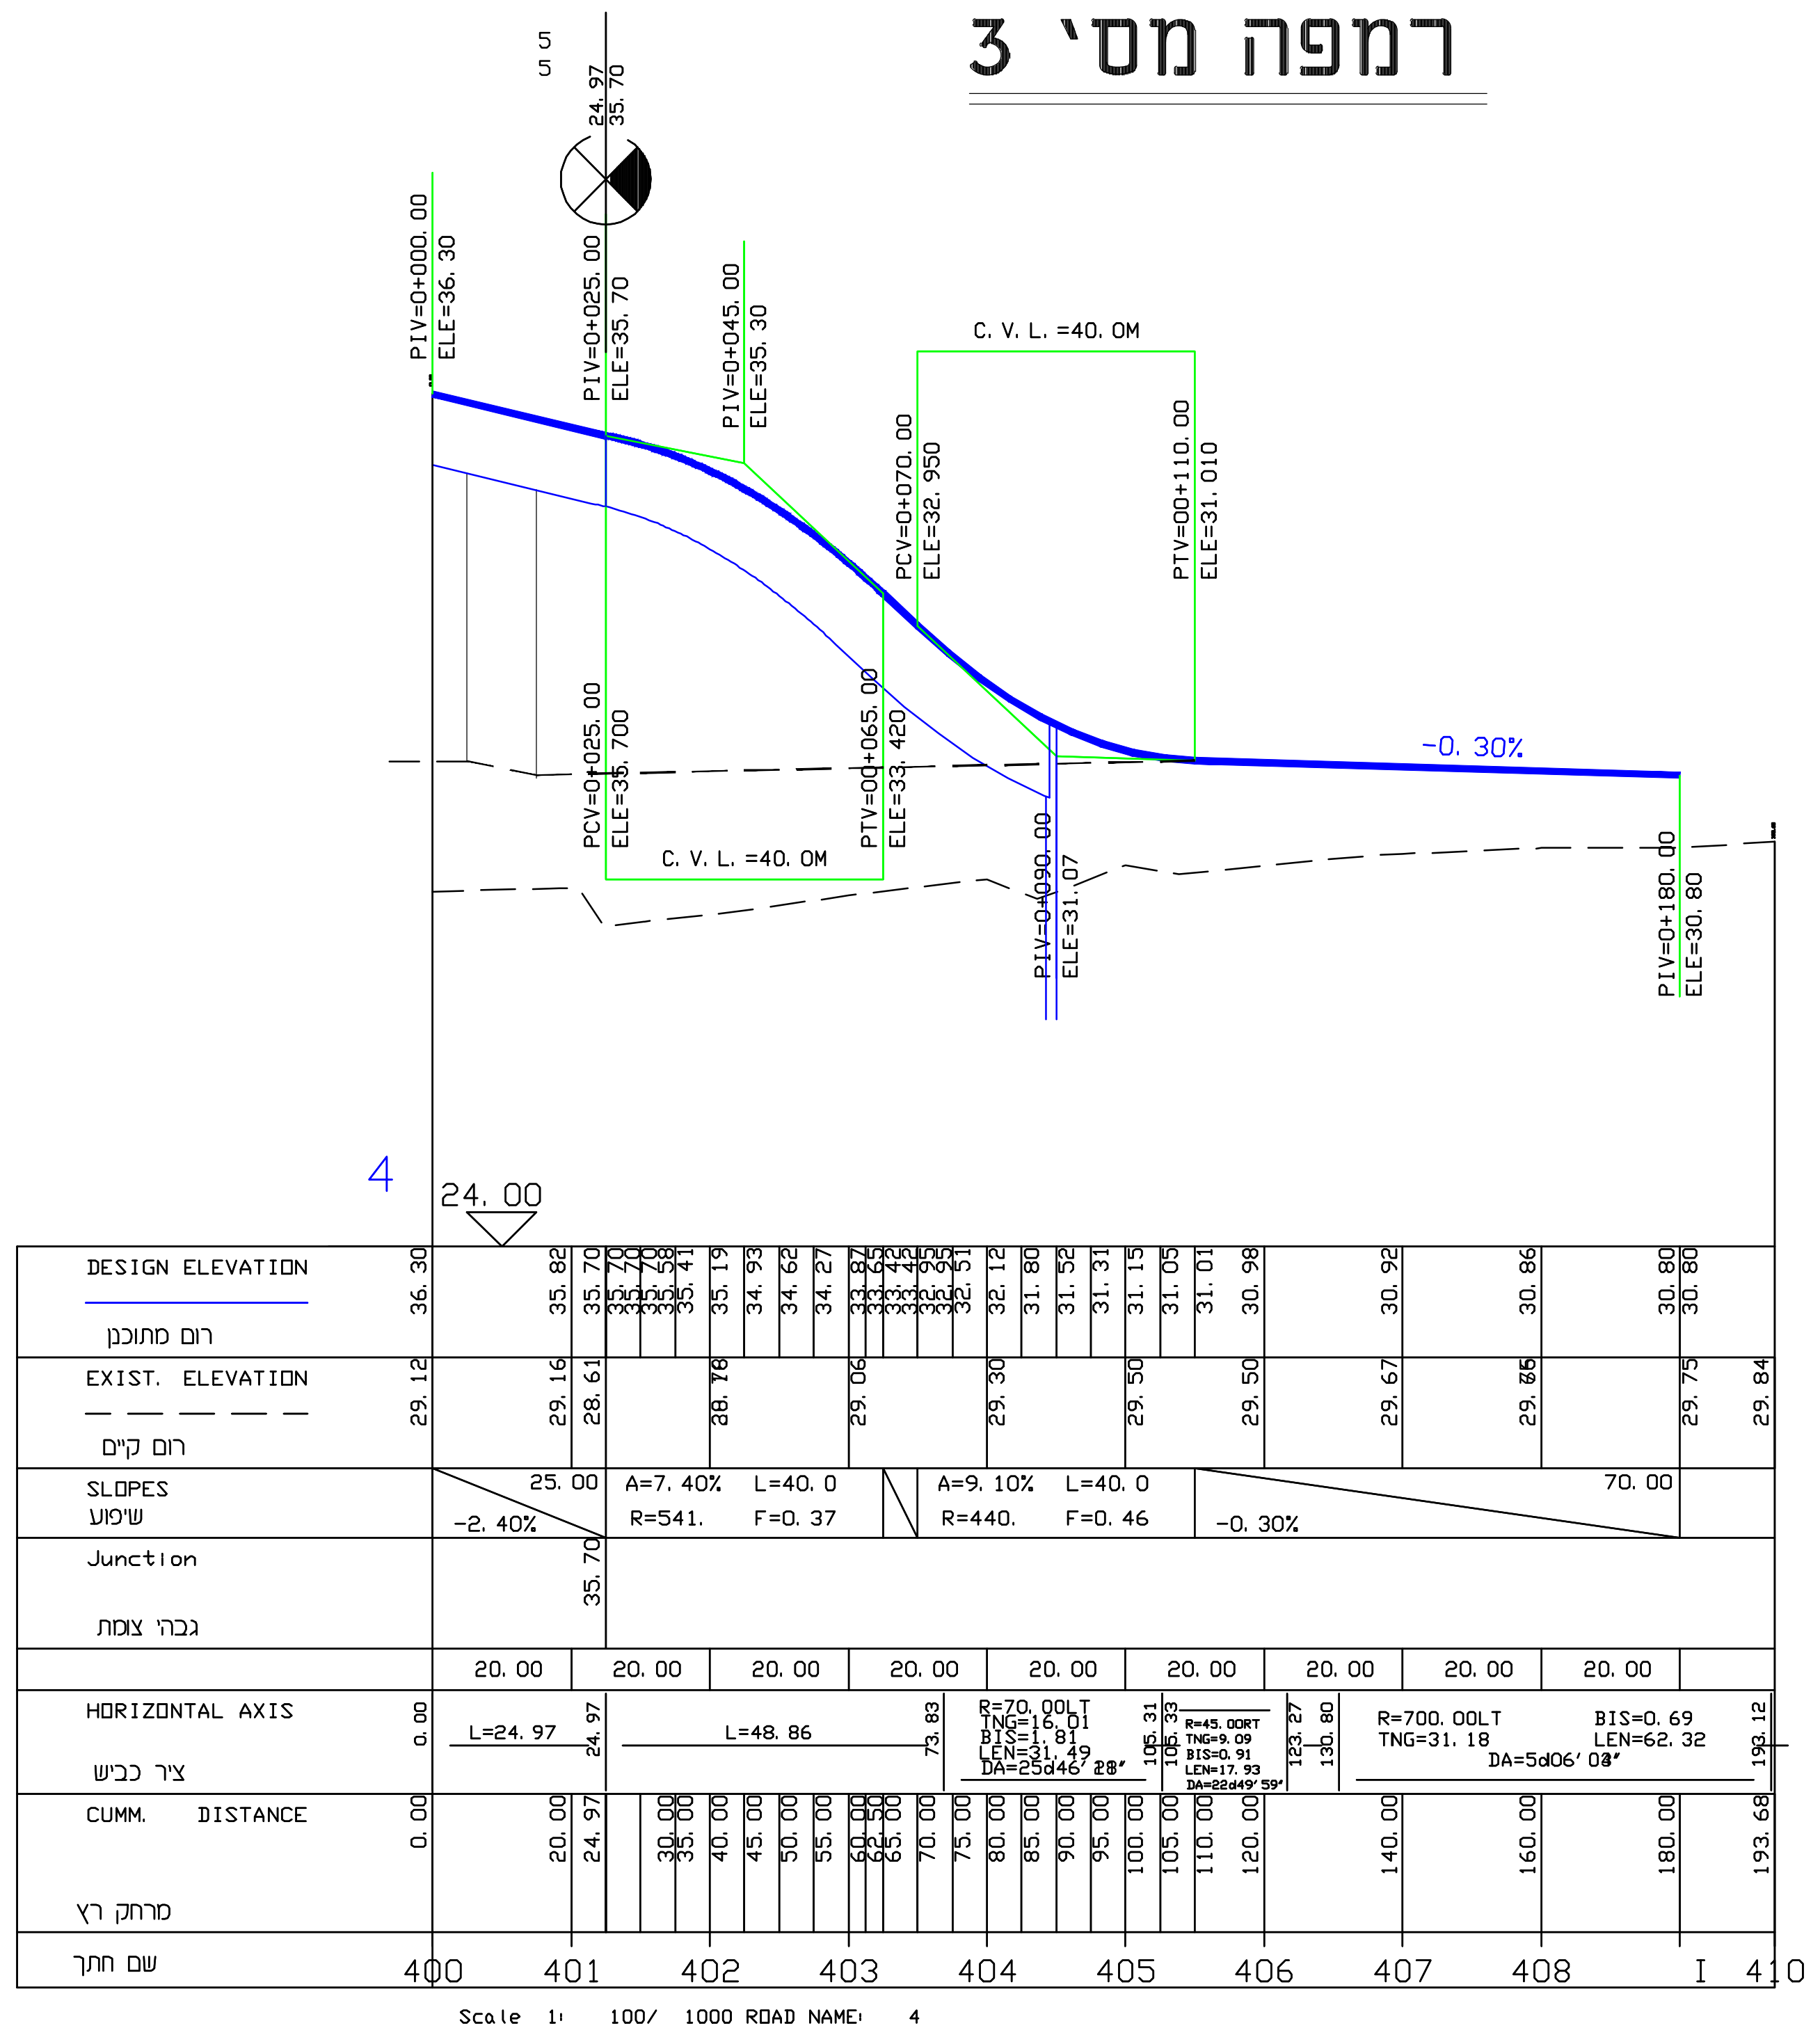

רמפה מס' 4

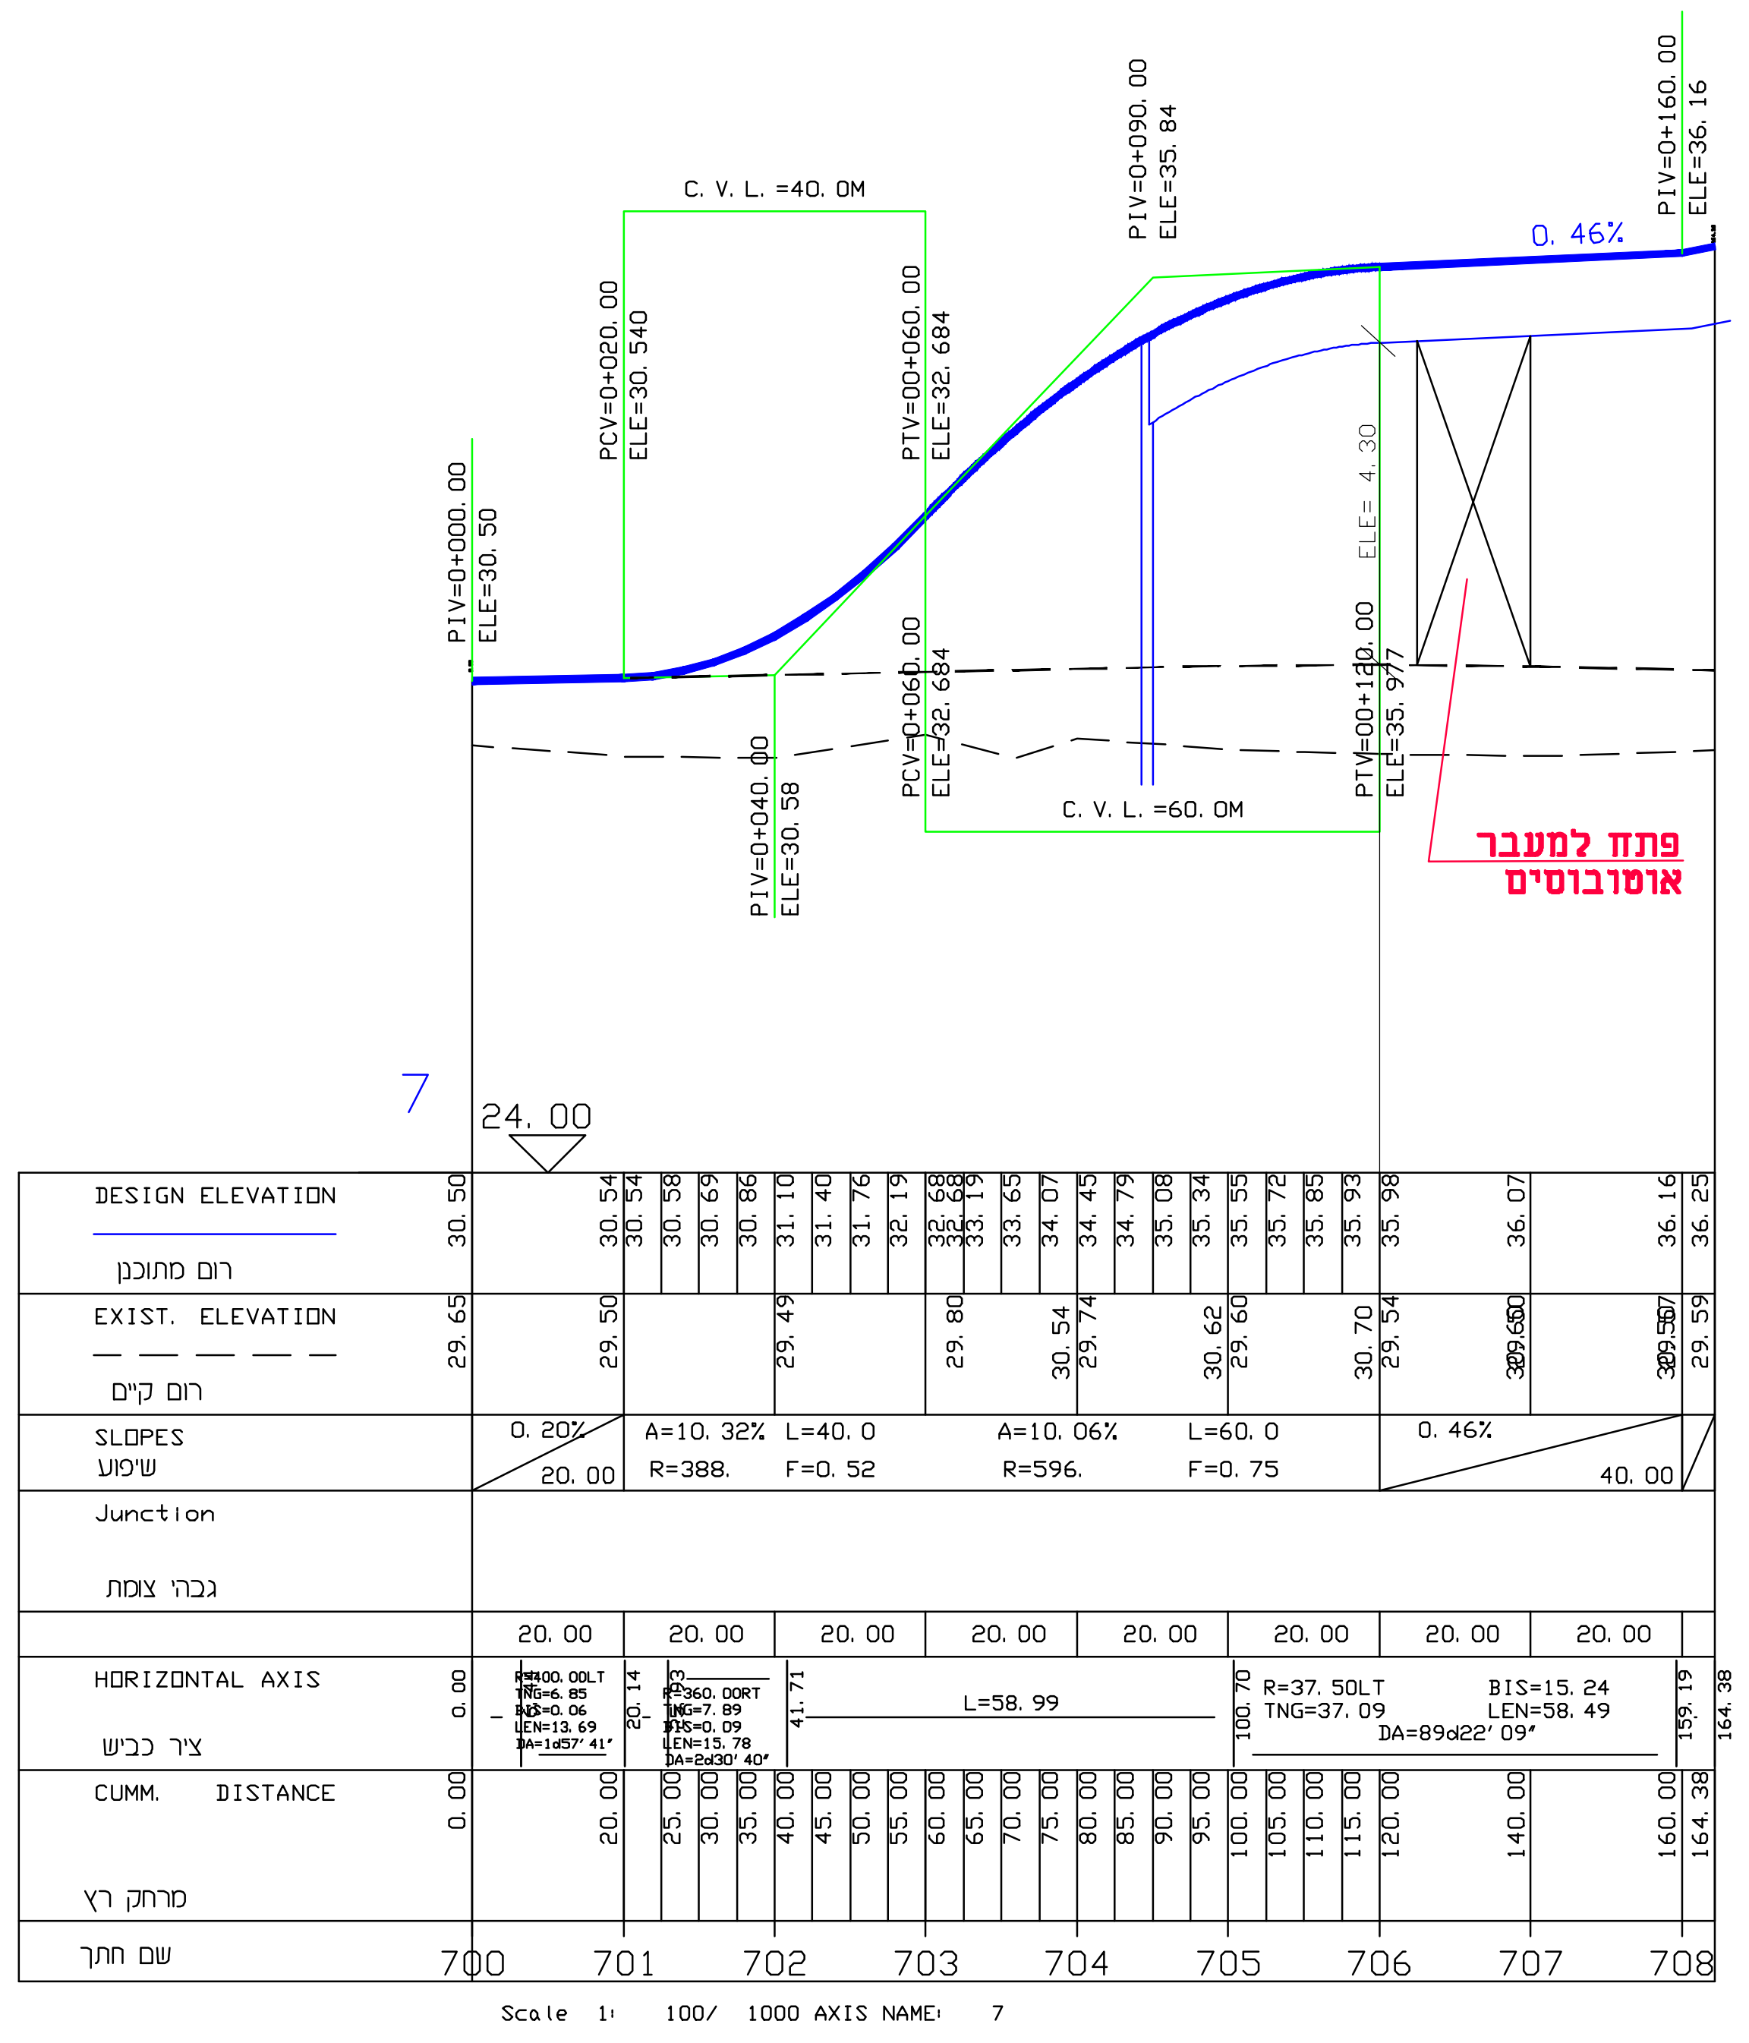

כביש מס' 1
ציר החניון

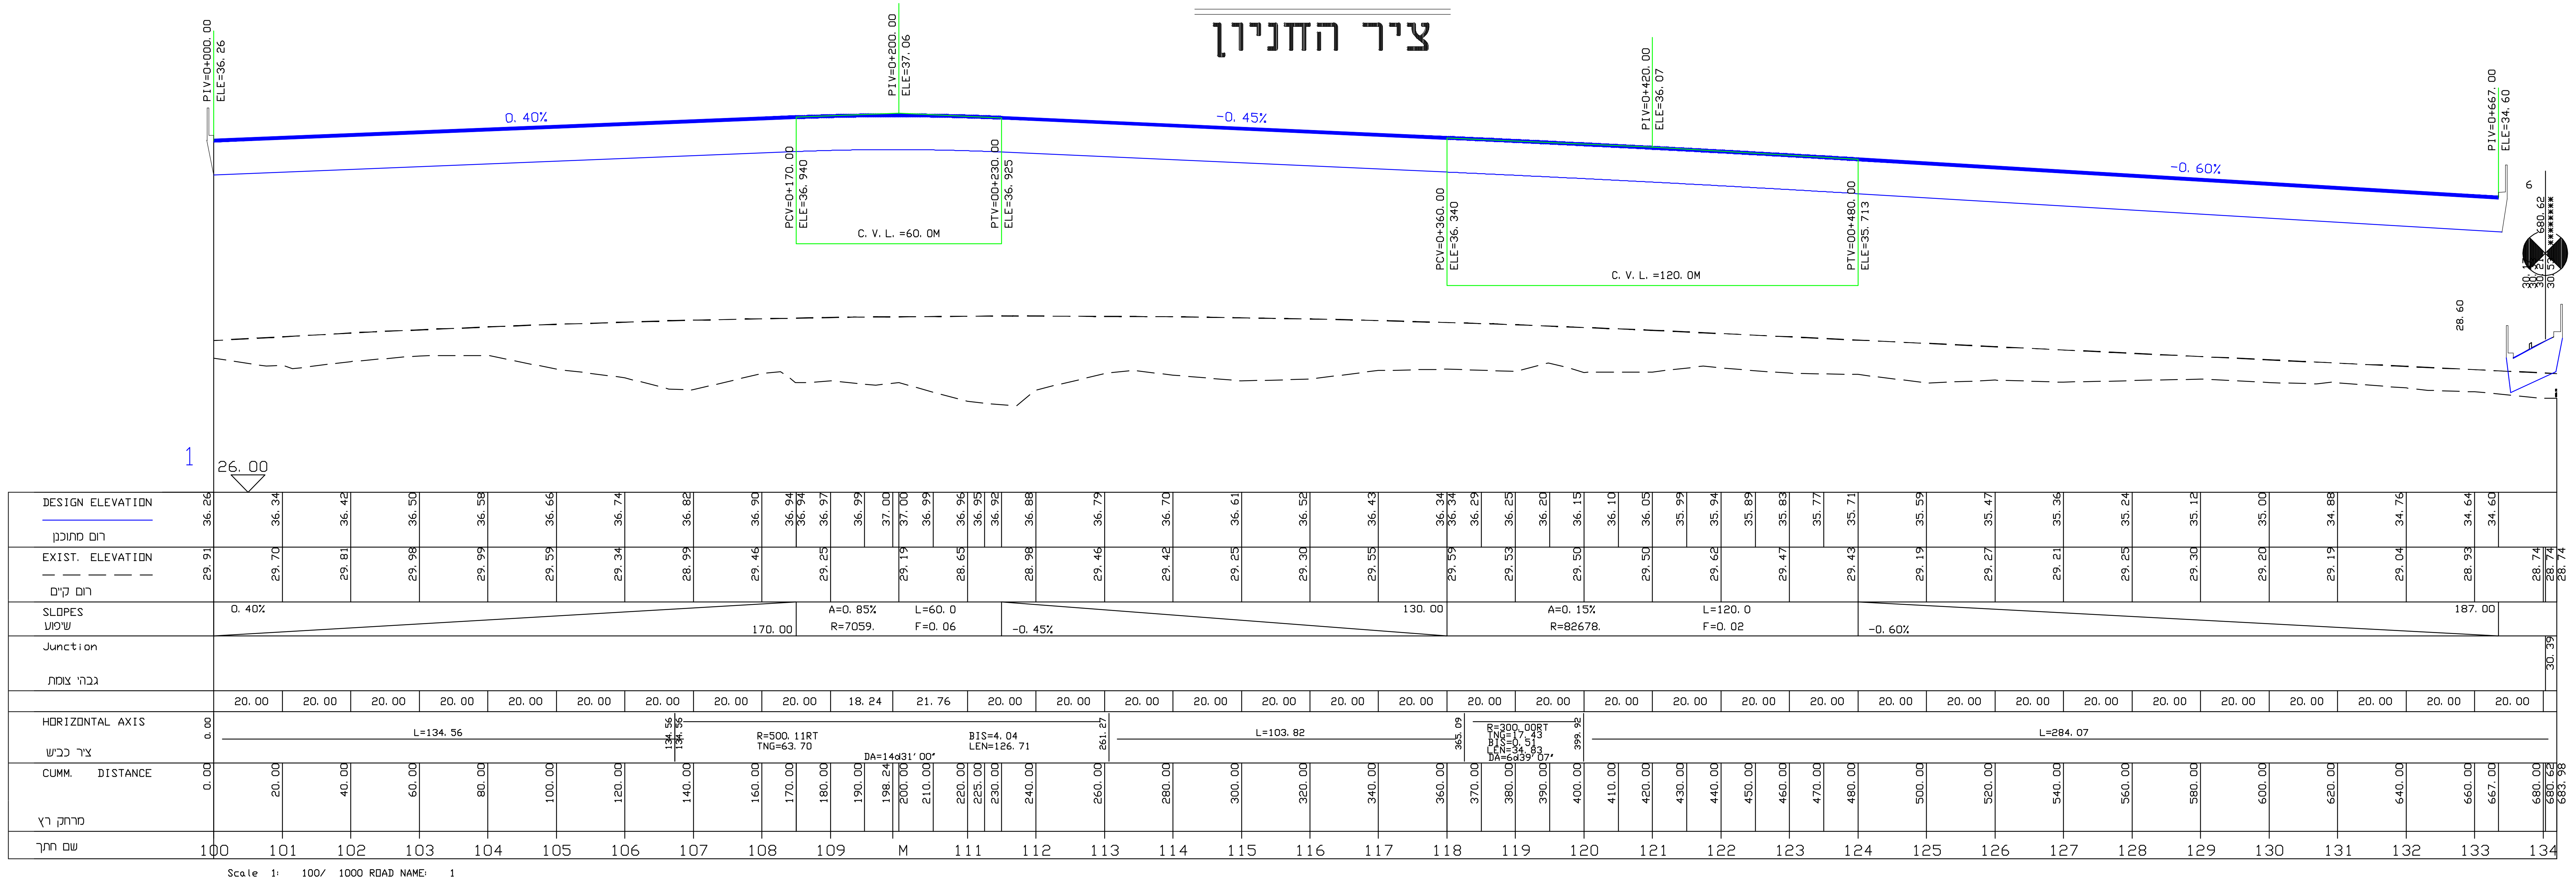

תנוחת צירים

ללא קנ"מ

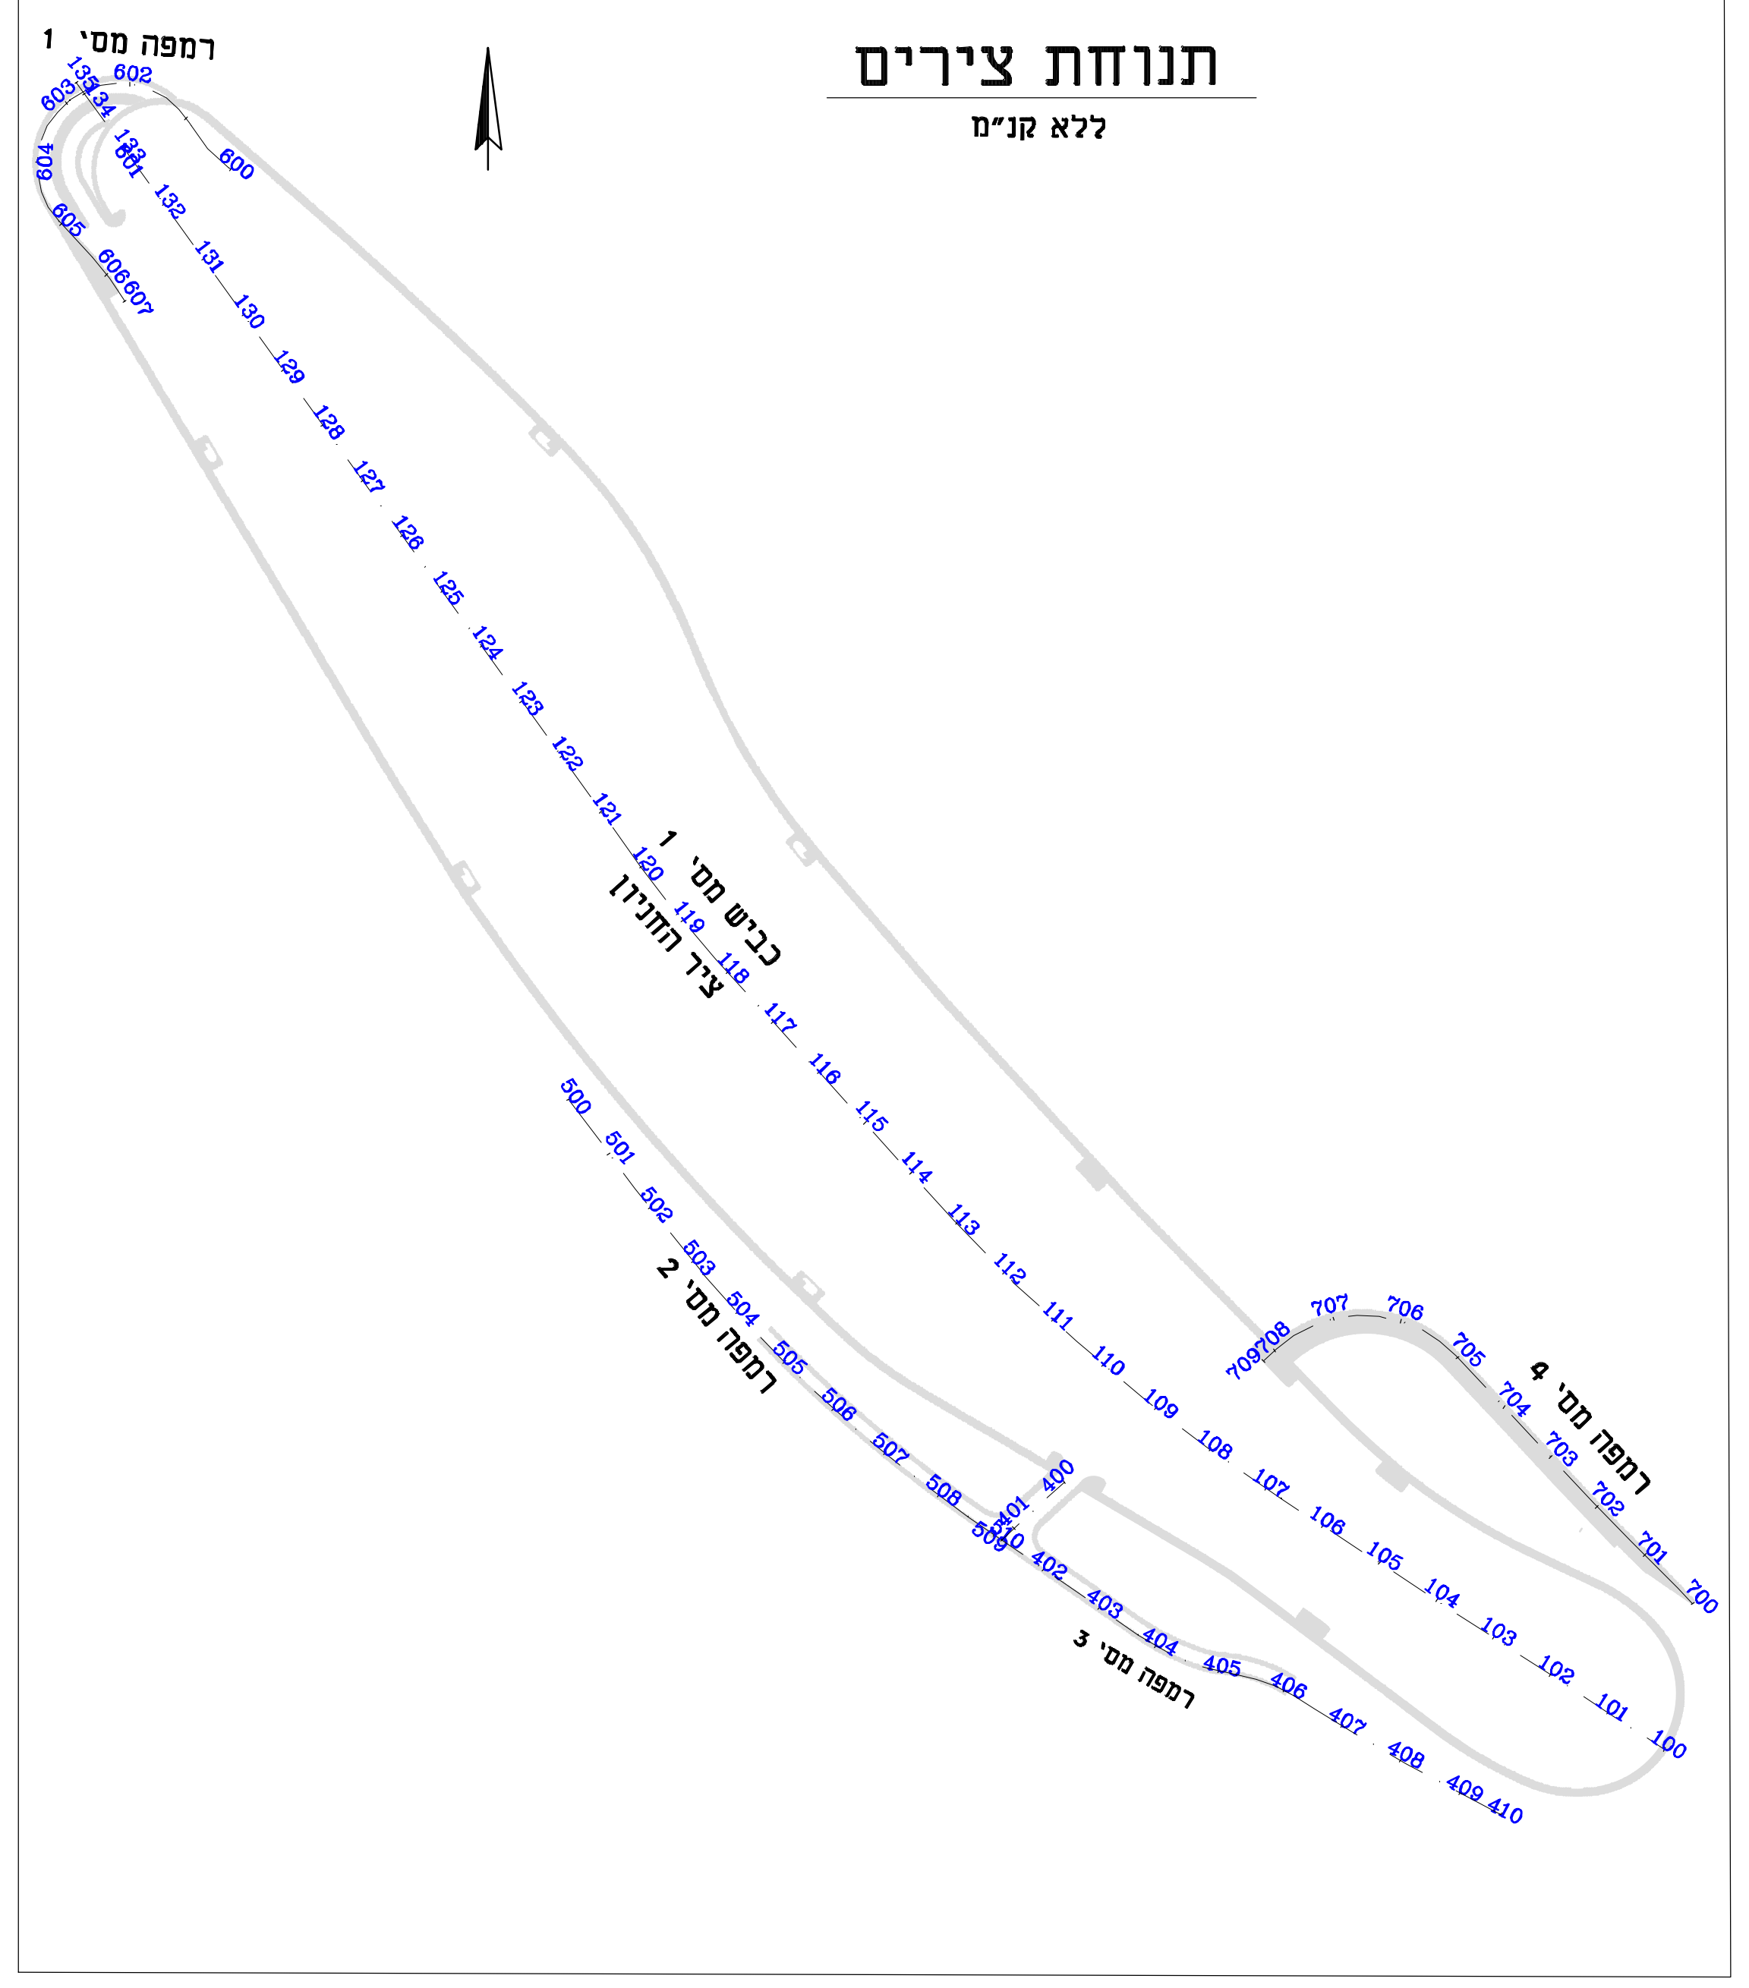

חוק התכנון והבנייה, התשכ"ח - 1965
תכנית לתשתית לאומית

תת"ל\66

"חנה וסע" שפירים

חתכים לאורך + רמפות גליון 1 מתוך 1

מחוז	המרכז
מרחב תכנון מקומי	עמק לוד, מצפה אפק
רשות מקומית	מועצה אזורית עמק לוד
ישוב	
תאריך	13/09/15

שם הנספח	קנ"מ
חתכים לאורך + רמפות	1:100:1000
תרשים סביבה	1:50,000

שמות וחתימות:

עורך התוכנית	שם: שלמה גלבר תאגיד: חלו"א חברה למדידות והנדסה אזרחית (1985) בע"מ	חתימה:

T:\6822 HANYON SHPIRIM-B\IZIK\TNU-LAHV-2014\OREH-OLL-03.dwg, Model, 06/10/2015 11:20:34,
DWG To PDF.pc3